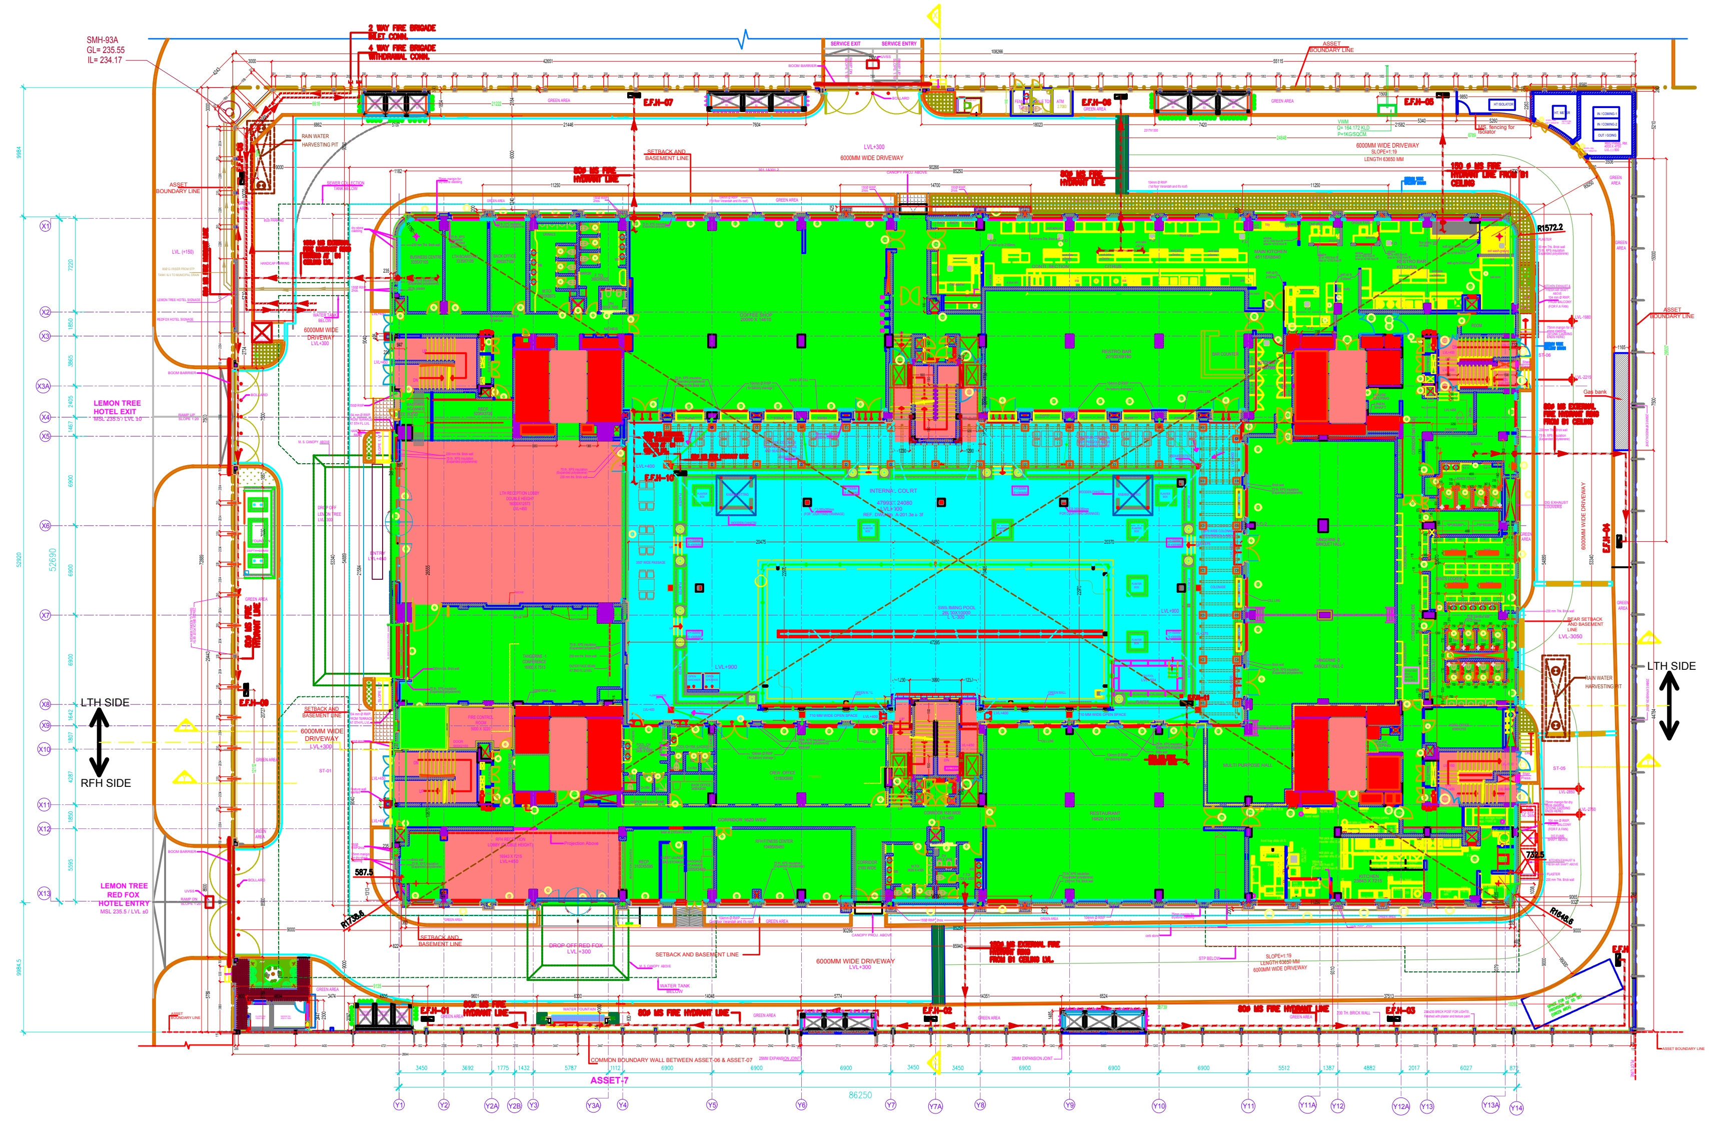

SANITARY REQUIREMENTS IN GROUND FLOOR					
FLOOR AREA IN SQ.M.	OCCUPANCY 10 SQ.M /P	MALE (2/3)	FEMALE 1/3)		
3604.76	360	240	120		
MALE	REQ.	PROVIDED	FEMALE	REQ.	PROVIDED
WC	**10**	**10**	**WC**	**8**	10
WB	**10**	**14**	**WB**	**5**	10
URINAL	**8**	**14**			

LEGEND

▮	FIRE CHECK DOOR
◪	FIRE HOSE CABINATE WITH 02 HOSE AND 01 BRANCH PIPE
●	WET RISER
⊕	HOSE REAL HOSE
■	MANUAL CALL POINT
●	4.5 KG. CO2 FIRE EXTINGUISHER
▲	9.0 LTS. WATER CO2 FIRE EXTINGUISHER
▬	YARD HYDRANTS

DRWG NO.
LTH/DL2/ 02 (R24/ 01/ 24)

NOTES AND REFERENCES

* All dimension are in mm.
* All dimension to be read not to be scaled.
* All levels are in mm. w.r.t MSL+235.0
* The building is centrally air conditioned, mechanically ventilated and fully sprinkled.

LEGENDS

- 🟥 SERVICE CUTOUTS AND LIFT SHAFTS AREAS
- 🟩 FAR AREAS
- 🟥 SERVICES AREA FREE OF FAR
- 🟦 COURTYARD

DOOR / WINDOW SCHEDULE

DOOR SCHEDULE

TYPE	CILL	SIZE	LINTEL	REMARKS
D1	±00	750X2100	+2100	TOILET
D2	±00	900X2100	+2100	KITCHEN / TOILET
D3	±00	1000X2100	+2100	OFFICE / PUBLIC TOILET
D3A	±00	1000X2100	+2100	CHANGING ROOM
D3b	±00	900X2100	+2100	KITCHEN
D3c	±00	830X2575	+2575	BAGGAGE SCANNER
D4	±00	1100X2100	+2100	HANDICAP TOILET(sliding door)
D5	±00	1200X2100	+2100	RON
D6	±00	1500X2100	+2100	COFFEE SHOP/RESTAURANT
D6a	±00	1500X2100	+2100	ENTRY CORRIDOR
D6b	±00	1500X2100	+2100	METER RM/HT BREAKER RM
D6c	±00	1500X2100	+2100	COFFEE SHOP
D6d	±00	1500X2100	+2100	KITCHEN
D7	±00	1650X2100	+2100	RFH FITNESS CENTRE
D8	±00	2250X2400	+2400	RECEPTION LOBBY
D8a	±00	1750X2700	+2700	RECEPTION LOBBY
D9	±00	2250X2775	+2775	REST./CREW LOUNGE
D9a	±00	2100X2400	+2400	RECEPTION LOBBY
D9b	±00	2100X2700	+2700	REV. DOOR RFH REC. LOBBY
D9c	±00	2250X2775	+2775	RFH CORRIDOR
D10	±00	1100X2100	+2100	HANDICAP ROOM, SWING DOOR
D11	+150	600X1950	+2100	SHAFT ACCESS DOOR
D11a	+150	525X1950	+2100	LV DOOR
D12	+900	600X1200	+2100	SHAFT ACCESS DOOR
D13	+150	900X1950	+2100	FHC DOOR
D14	±00	900X2100	+2100	CORRIDOR
FCD1	±00	1000X2100	+2100	HOUSE KEEPING
FCD2	±00	1500X2100	+2100	STAIRCASE
FCD3	±00	1650X2100	+2100	STAIRCASE
FCD4	±00	1800X2100	+2100	SERVICE LIFT LOBBY
FCD4a	±00	1800X2100	+2100	GUEST LIFT LOBBY
SCD1	±00	1500X2100	+2100	STAIRCASE
SCD2	±00	1650X2100	+2100	STAIRCASE
SD1	±00	1100X2100	+2100	HANDICAP ROOM TOILET
SD2	±00	1420X2100	+2100	RFH ROOM
SD3	±00	1650X2100	+2100	STAIRCASE
SD4	±00	1800X2100	+2100	LTH ROOM

NOTE:- FCD4a DOOR IN LTH & RFH GUEST LOBBY IS GLAZED FIRE DOOR

WINDOW / GLAZING SCHEDULE

TYPE	CILL	SIZE	LINTEL	REMARKS
W1	900	700 X 1200	2100	DG SHAFT
W2	1050	950 x 1650	2700	RFH TOILETS (F.F)
W3	825	828.5 X 1750	2575	LTH RECP AND STORE
W3a	1100	828.5 X 1025	2125	LTH office , RFH pantry
W4	2080	810X1445	AS/ ELE	STAIRCASE WINDOW
W5	900	1250 X 1200	2100	DG SHAFT
W6	1200	1250 X 1250	2450	KITCHEN
W6a	1200	1250 x1250	AS/ ELE	STAIRCASE WINDOW
W7	1200	1020 X 1250	2450	TOILET & TIME MACHINE
W8	815	1800 X 1320	2135	GUEST ROOM (LTH)
W8a	815	1420 X 1320	2135	GUEST ROOM (RFH)
W9	300	1650 X 2400	2700	KITCHEN / PUBLIC AREAS
W9a	2100	1720 X600	2700	CHANGING ROOM RFH
W9b	900	1650 X1800	2700	KITCHEN
W10	750	1420 X 1350	2100	GUEST ROOM
W11	300	1800 X 2400	2700	LTH REC. LOBBY
W11A	300	1800 X 900	1200	LTH REC. LOBBY
W12	2100	2100 X 1450	3550	CHANGING ROOM LTH
W13	300	2100 X 2400	2700	COFFEE SHOP/RON/REST.
W13A	450	2100 X2250	2700	
W13B	900	2100 X1800	2700	KITCHEN COFFEE SHOP, RON & RESTAURANTS
W13C	300	2100 X2400	2700	BAGGAGE SCANNER (AS/ELE)
W13D	1350	2100 X1350	2700	RFH REC. LOBBY
W14	2850	1800 X 450	3300	TOILETS
W15	2100	2100 X 600	2700	CHANGING ROOM RFH
W16	1175	3335 X 2375	3550	DG EXHAUST
W17	-50	3335 X 2750	2700	DG EXHAUST
W18	900	1020 X 1200	2100	CORRIDOR
W25	300	2100 X 2300	2600	OFFICE (COURTYARD SIDE)
W26	900	600 X 1200	2100	SHAFT (PLUMBING, LV)
W	900	450 X 1200	2100	SHAFT (PLUMBING, LV)
W30	815	2100 X 1885	2700	

PROJECT:

HOTEL BUILDING FOR LEMON TREE AND RED FOX HOTEL
AT ASSET-6, IN HOSPITALITY DISTRICT,DIAL, IGI AIRPORT, DELHI

OWNER:
HYACINTH HOTELS PRIVATE LTD.
Reg. Off.: B-6/17, Safdarjung Enclave, New Delhi-110029, INDIA
Corp. Off: 201, Okhla Industrial Estate, Phase-III, New Delhil-20, INDIA

Architect / Consultants

Owner / Client

Drawing Title :
GROUND FLOOR
MSL +235.95 M

Drawing Status:
REVISED COMPLETION PLAN

Scale: 1 : 100

Dated : 30.11.2023

North
N

Dwg No.
LTH / DL2 / 02

Rev No.
R24

Sanctioning Authority