


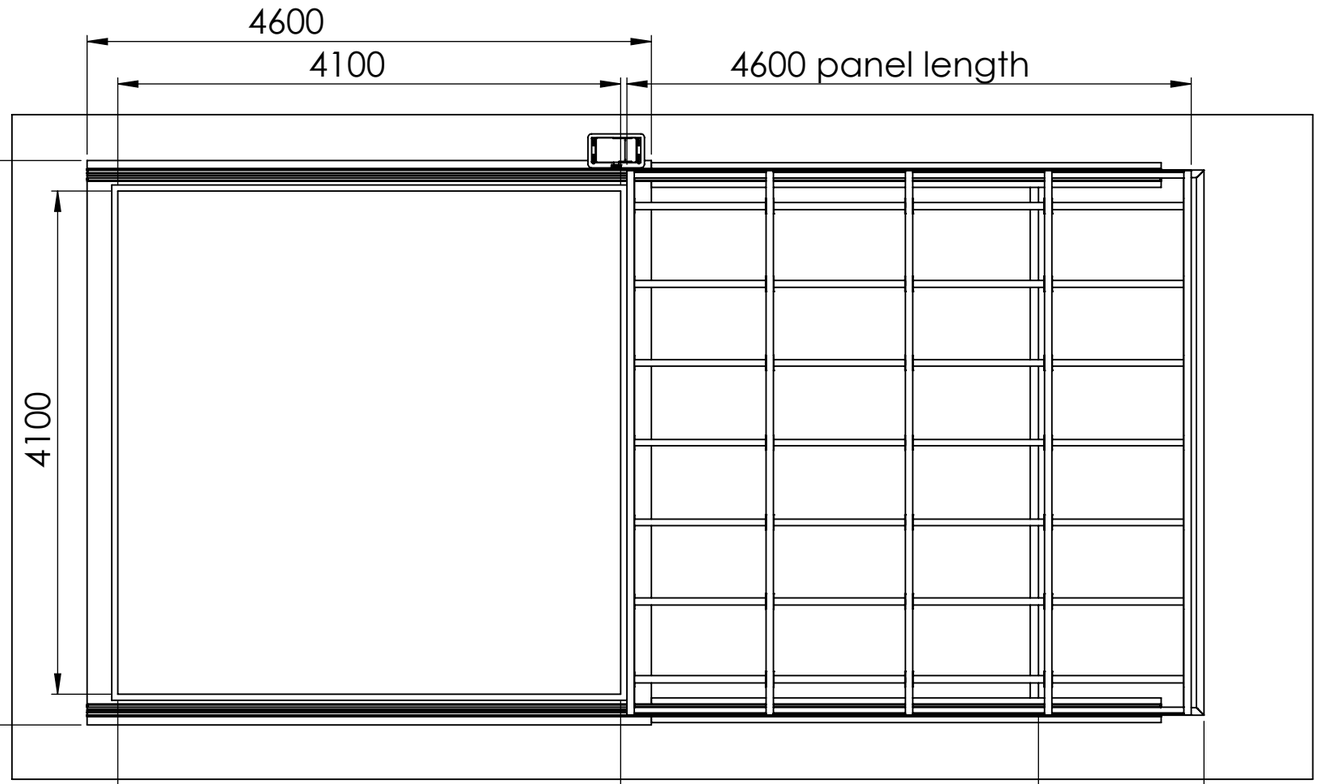


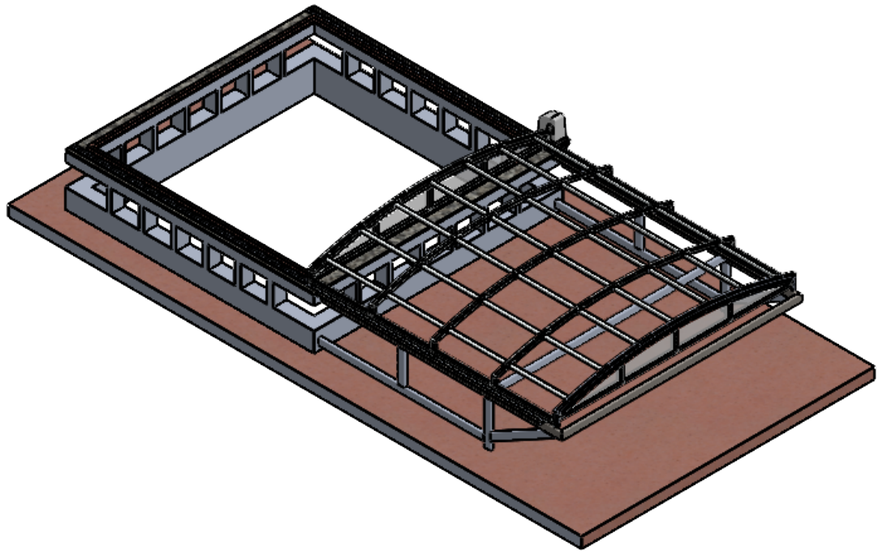


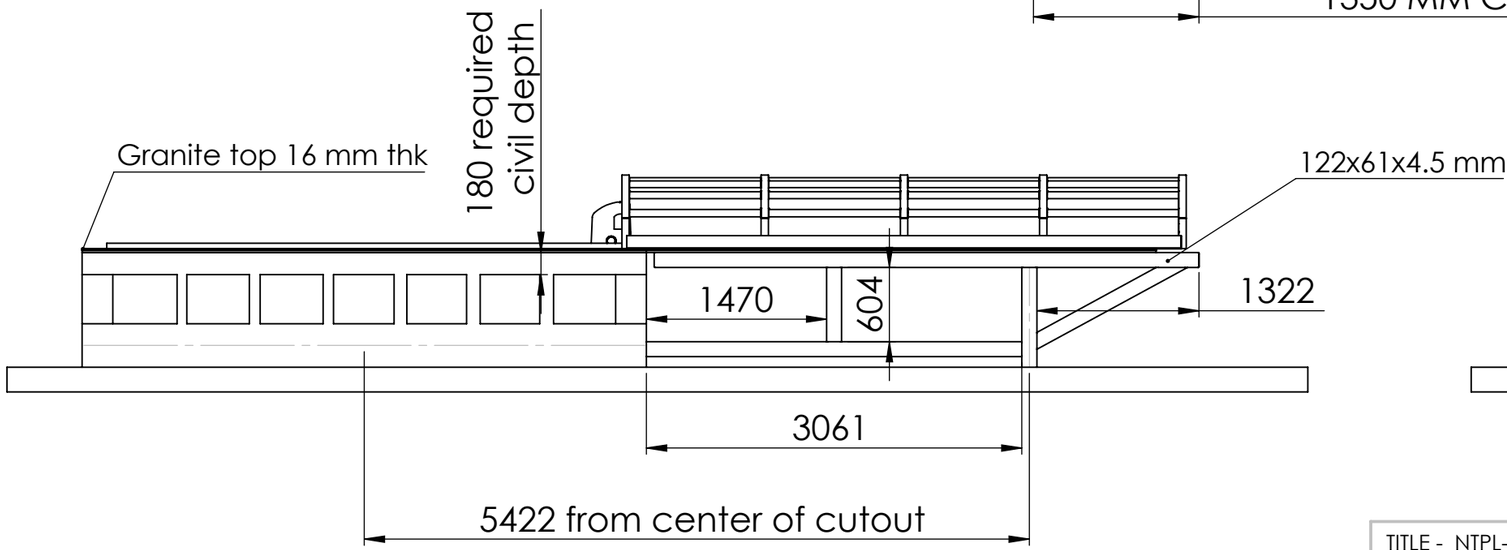


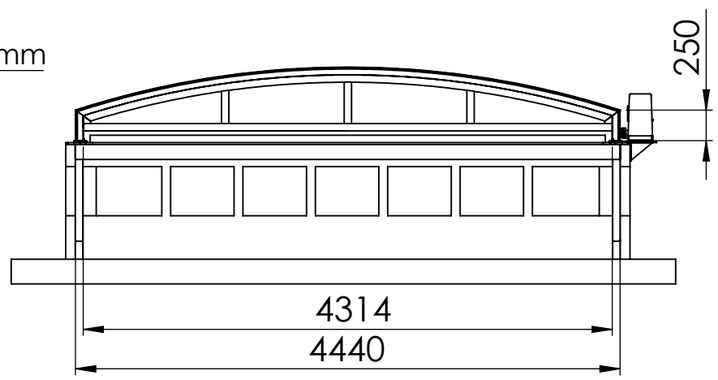


Note :
1) Top civil depth is shown as 100 mm in given autocad drawing and must be increased upto 180 mm for mounting of track
2) top surface shoud be of granite 16 mm thick
3) clear opening is 3812 mm
4) ms plate and granite top surface must be on same level for Track mounting

TITLE - NTPL-183 UPDATED OPENING GA				NIHVA TECHNOLOGIES PVT.LTD.PUNE Website - www.nihva.com
	NAME	SIGNATURE	DATE	PROJECT NO - NTPL 183-HP
DRAWN	H.B.		17.08.2023	PRODUCT - RETRACTABLE ROOF
CHK'D	P.M.		17.08.2023	SITE LOCATION - Ahmedabad
APPV'D	V.T.		17.08.2023	
if any queries contact - supportautomation@nihva.com				REVISION -
ALL DIMENSION ARE IN mm			A3	SCALE - SHEET 1 OF 2

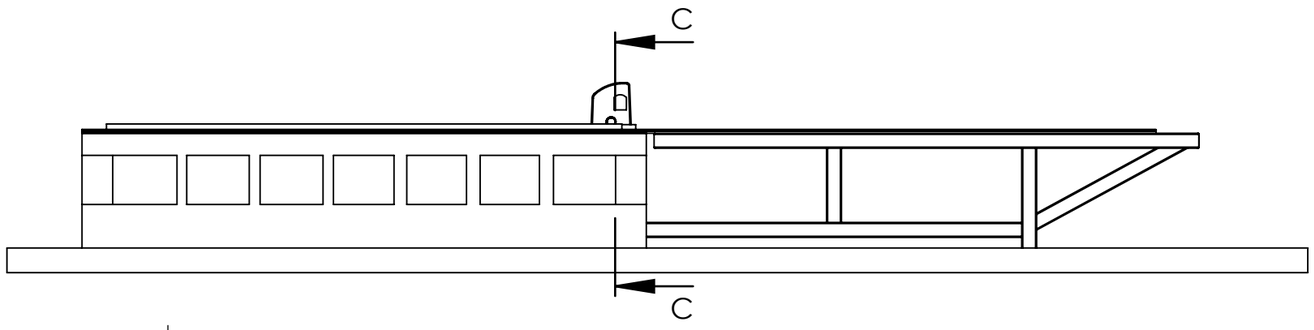


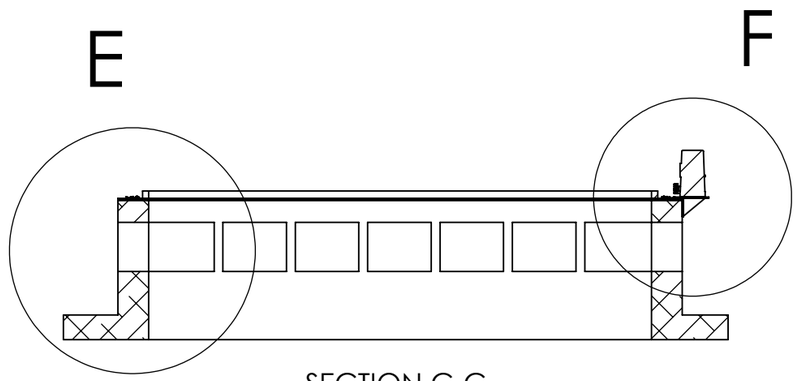

SECTION C-C

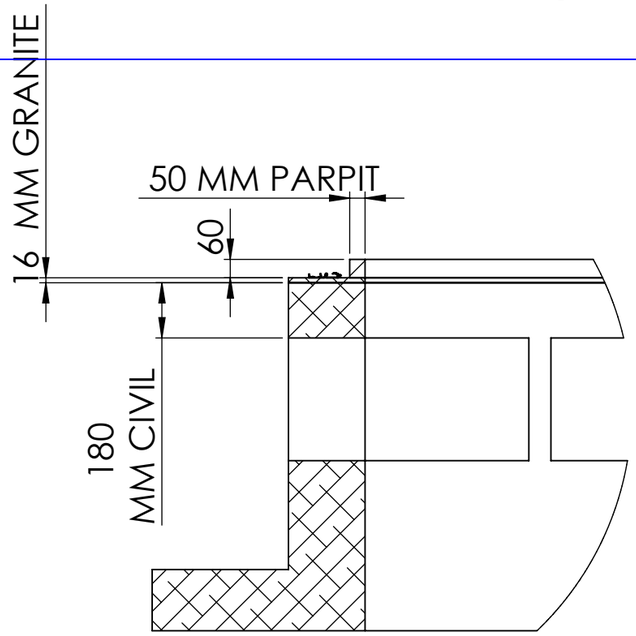

DETAIL E

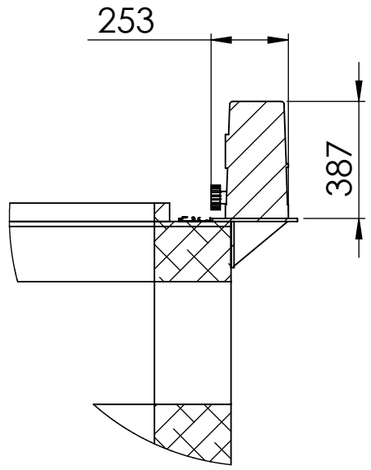

DETAIL F

MOTOR SPECIFICATIONS

1. MODEL - NICE RUN1800
2. CAPACITY - 1800KG
3. MOTER SUPPLY- 230V AC SINGLE PHASE
4. CABLE - 2.5 SQ MM 4 CORE
5. SIZE - 400X387X253 MM

TITLE - CIVIL CROSS SECTION AND MOTER				NIHVA TECHNOLOGIES PVT.LTD.PUNE Website - www.nihva.com
DWG NO - NTPL183-CIVIL				
	NAME	SIGNATURE	DATE	PROJECT NO - NTPL 183-HP
DRAWN	H.B.		17.08.2023	PRODUCT - RETRACTABLE ROOF
CHK'D	P.M.		17.08.2023	SITE LOCATION - AHMEDABAD
APPV'D	V.T.		17.08.2023	
if any queries contact - supportautomation@nihva.com				REVISION -
ALL DIMENSION ARE IN mm		A3		SCALE - SHEET 2 OF 2