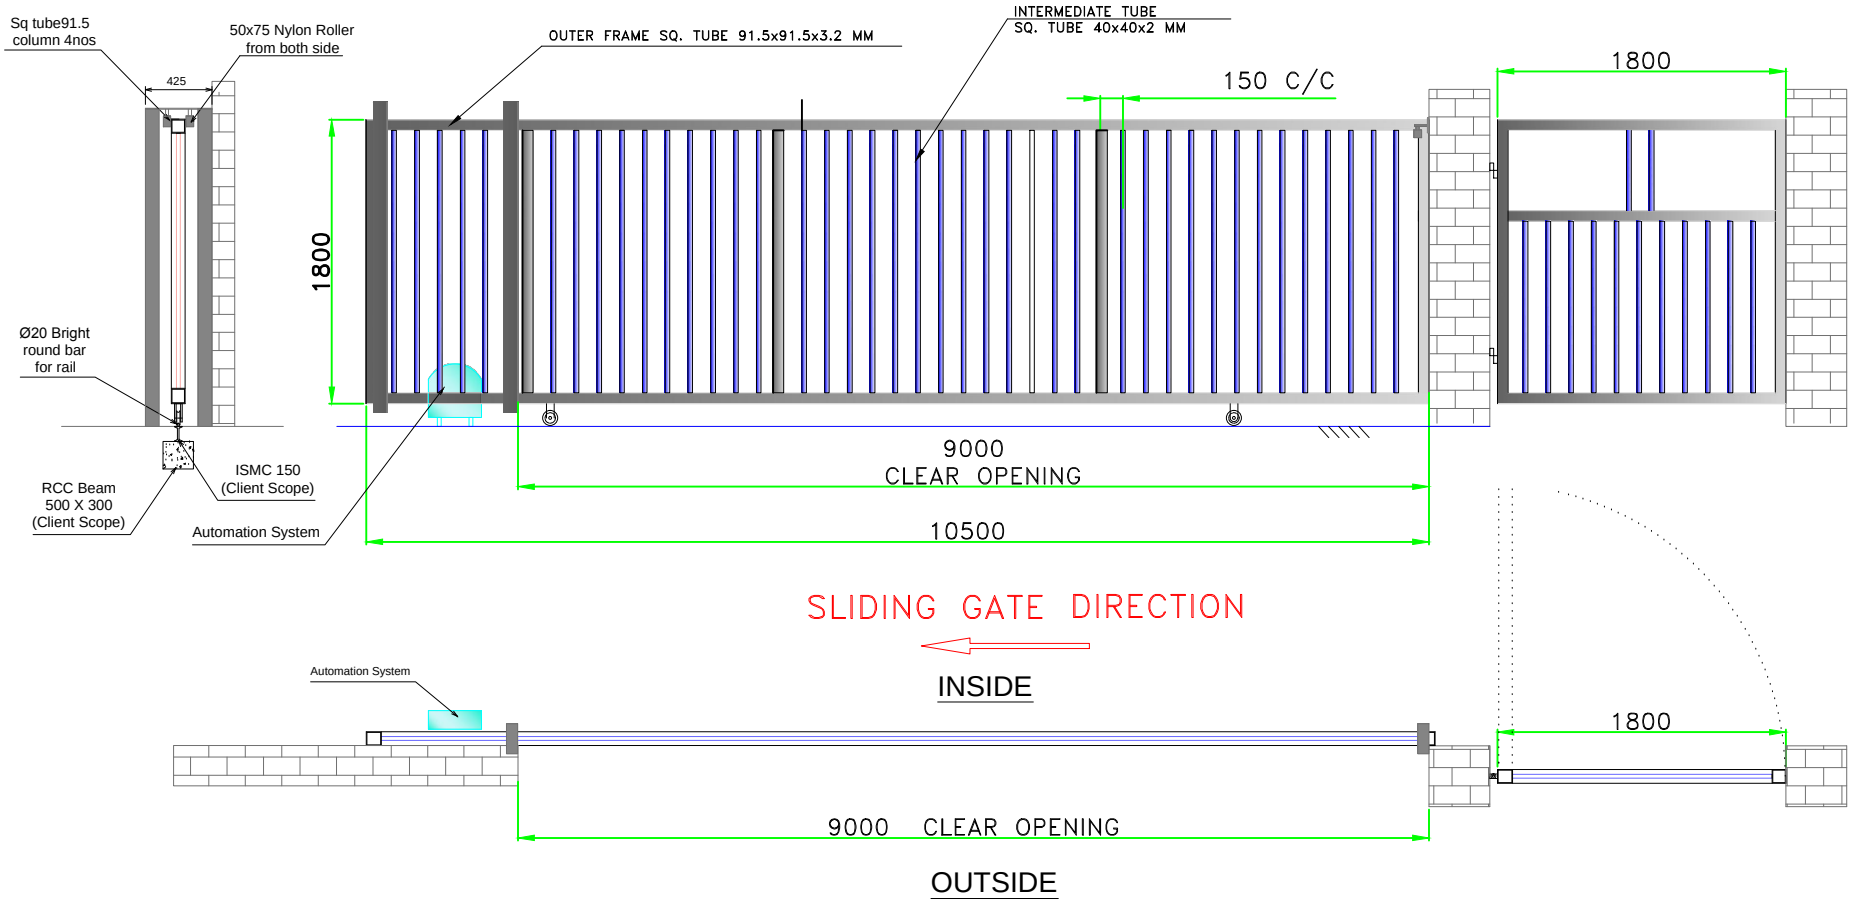


SLIDING GATE SIZE = 10500 (W) X 1800 (H), QTY = 1NOS.
CLEAR OPENING = 9,000 (W) X 1800 (H)
WICKET GATE SIZE = 1800(W) X 1800 (H), QTY = 1NOS.
.OUTER FRAME = 91.5 X 91.5 X 3.2 mm
INNER FRAME = 40 X 40 X 2 mm
GAP B/W FRAME = 150 c/c
C' COLUMN VERTICAL SUPPORT = 4 NOS.
ALL DIMENSIONS ARE IN MM

This drawing & designing is the property of NIHVA TECHNOLOGIES. Not be sold or copy to any other concern.

TITLE	ALL DIMENSION ARE IN mm			NIHVA TECHNOLOGY PVT. LTD. PUNE
SLIDING GATE		SIGN	DATE	NIHVA TECHNOLOGIES PVT. LTD.
	DRAWN	ABHIJIT	11/12/14	CLIENT - REWARD CONSTRUCTION
CLIENT APPROVAL	CHECK	ANIL	11/12/14	PROJECT -INGRERSOLL RAND
	REV.	04		SITE -NARODA , GUJRAT
	APPRD.			DWG. NO. - NVA/REWARD/D1/
	MFG			SCALE: 01 | WT: | SHEET: 01
	Ref. No.			If any queries contact : projects@nihva.com

Tel : 020 66304033
Email:- info@nihva.com
Website:- www.nihva.com