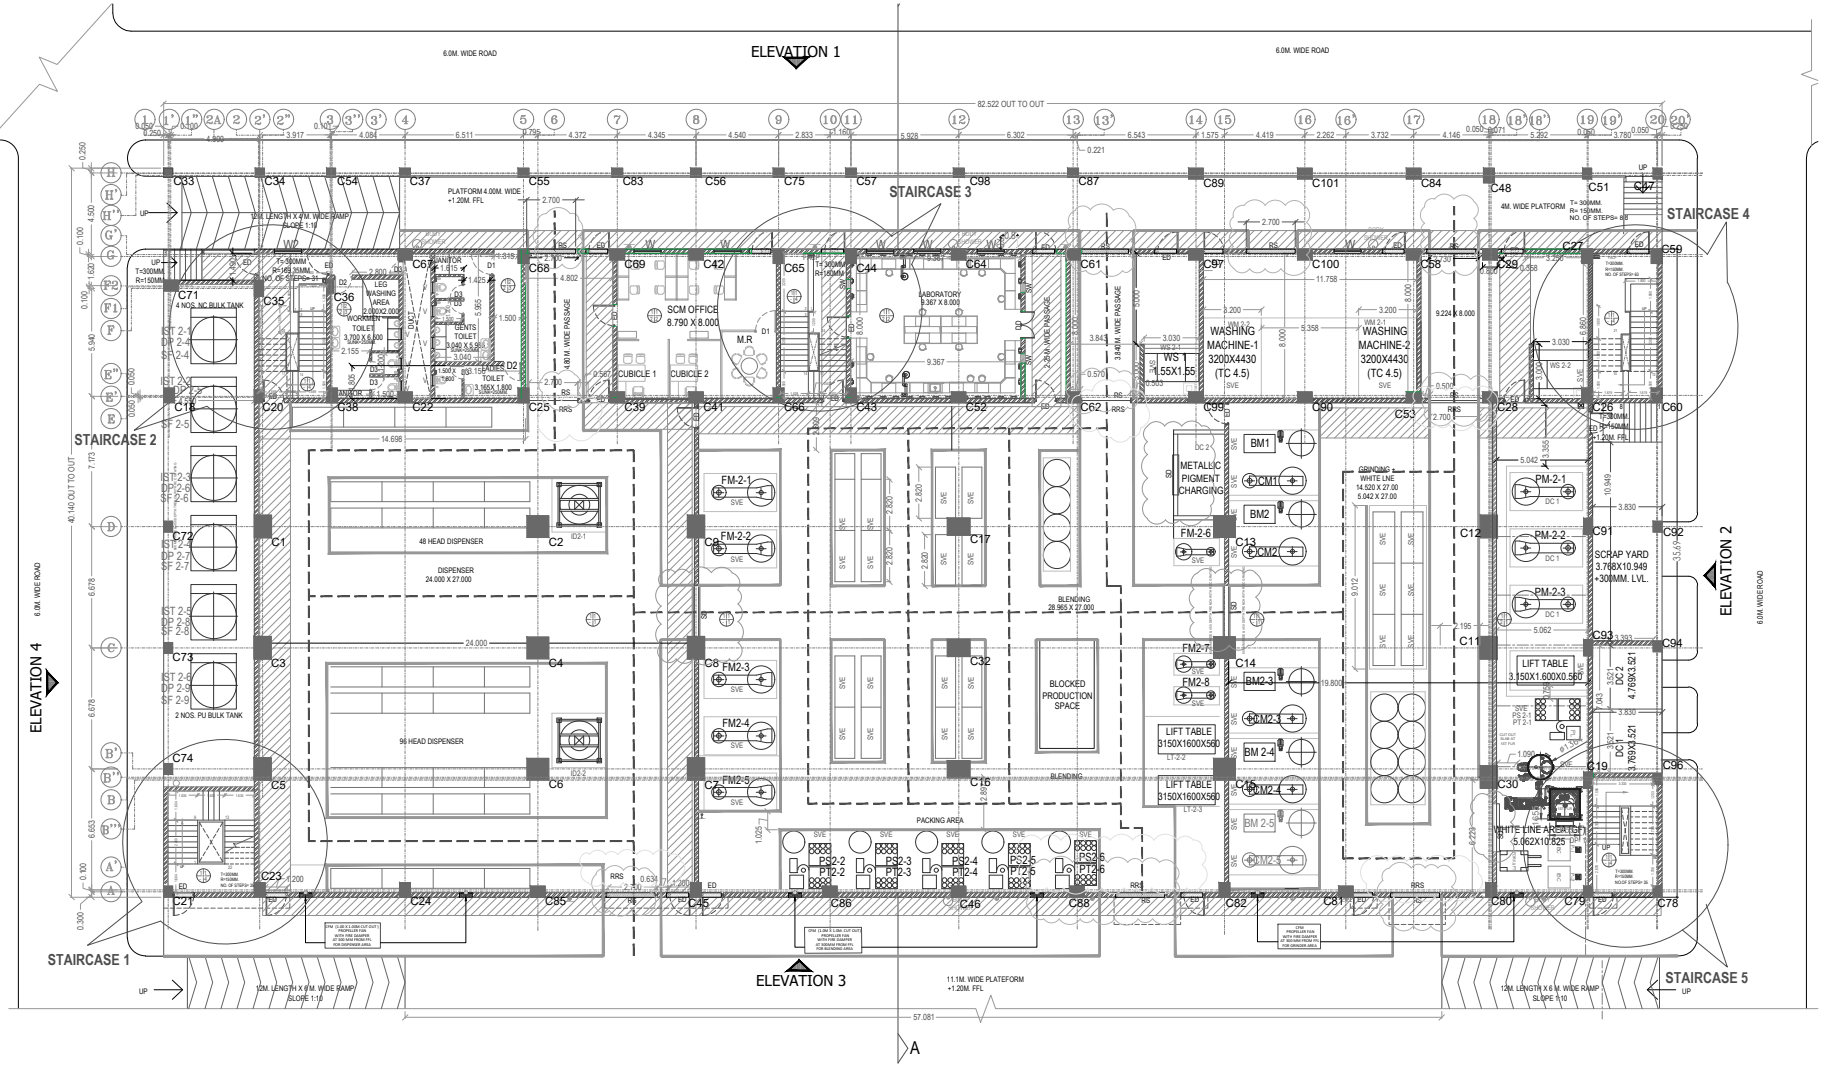


FIRE RATED BUILDING

DOOR & WINDOW SCHEDULE

S.NO.	SYMBOL	TYP.	SIZE	DESCRIPTION	SILL	LINTEL	QTY
1		RS	2700 X 3500	FIRE RATED MOTORIZED ROLLING SHUTTER	000	3500	4
2		RRS	2700 X 3500	FIRE RATED RAPID ROLL UP SHUTTER	000	3500	6
3		SD	2200 X 3000	FIRE RATED SLIDING DOOR	000	3000	4
4		ED	1200 X 2100	FIRE RATED EMERGENCY DOOR WITH VISION PANEL & PANIC BAR	000	2100	39
5		DD	1500 X 2400	FIRE RATED EMERGENCY DOUBLE DOOR WITH VISION PANEL & PANIC BAR	000	2400	6
6		D1	1200 X 2100	SINGLE SHUTTER SOLID CORE FLUSH DOOR	000	2100	5
7		D2	1000 X 2100	SINGLE SHUTTER SOLID CORE FLUSH DOOR	000	2100	5
8		D3	750 X 2100	SINGLE SHUTTER SOLID CORE FLUSH DOOR	000	2100	7
9		W	1500 X 900	FIRE RATED HMPS FRAME FIXED GLASS WINDOW	1200	2100	12
10		W1	1500 X 1000	FIXED GLASS WINDOW AS PER SPECS	6150	7150	17
11		W2	1500 X 1200	FIXED FIRE RATED GLASS WINDOW AS PER SPECS AT STAIRCASE	900	2100	5
12		EX1	1300X 950	EXHAUST FAN CUT OUT ON WALL FROM BEAM BOTTOM AT GR. FLOOR	3600	4550	3
13	CFM		1000 X 1000	EXHAUST CFM CUT OUT @ 300 MM. FFL	300	1300	6
14			1000 X 1000	EXTERNAL WALL CUT OUT @ MEZZANINE BEAM BOTTOM IN PANEL ROOM	2150	3150	2
15		V1	1500 X 900	LOUVERED VENTS AT MEZZANINE	900	2100	3
16		V	600 X 750	LOUVERED VENTS	1350	2100	11