

DRAWING

CLOSE VIEW

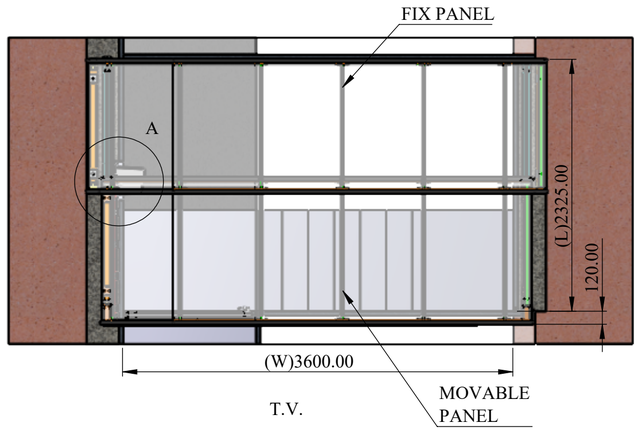


T.V.


OPEN VIEW

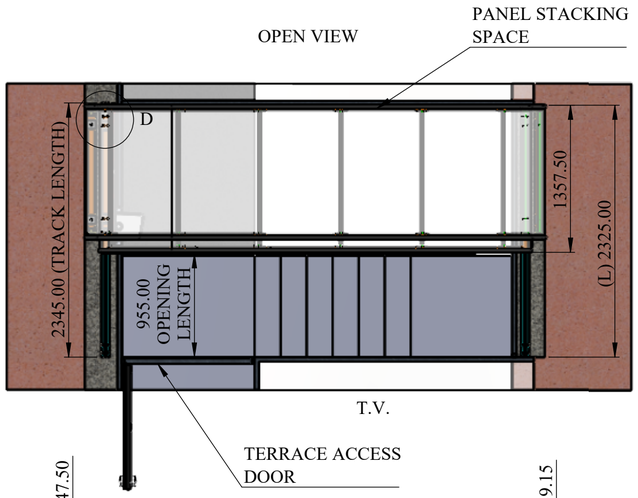


T.V.

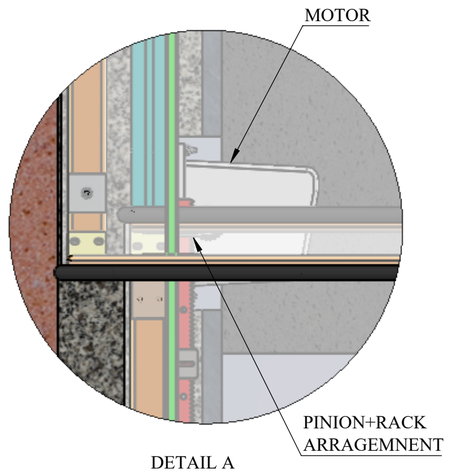


DETAIL A
SCALE 1 : 9

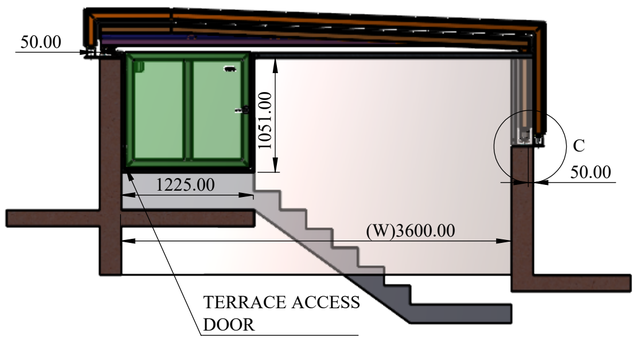


F.V.

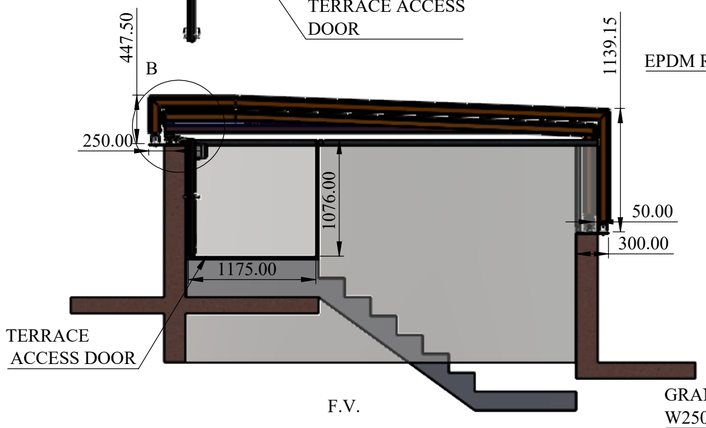

F.V.

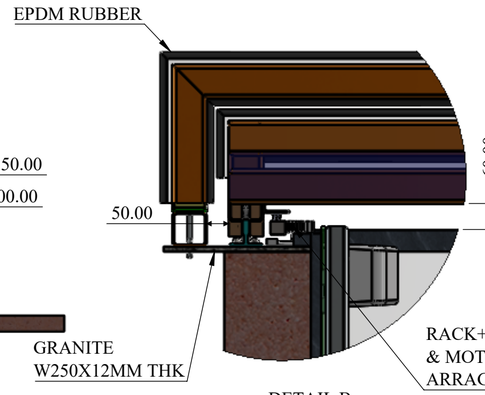


DETAIL B
SCALE 1 : 10

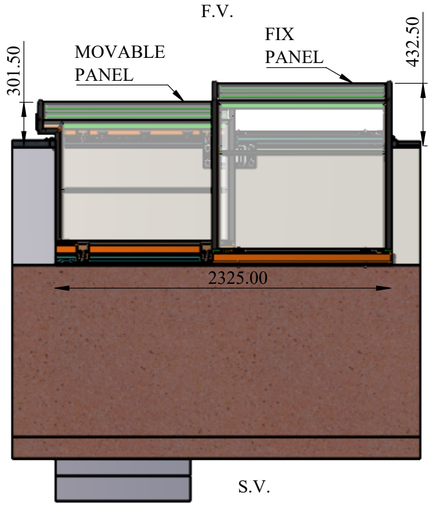


S.V.

CLOSE VIEW

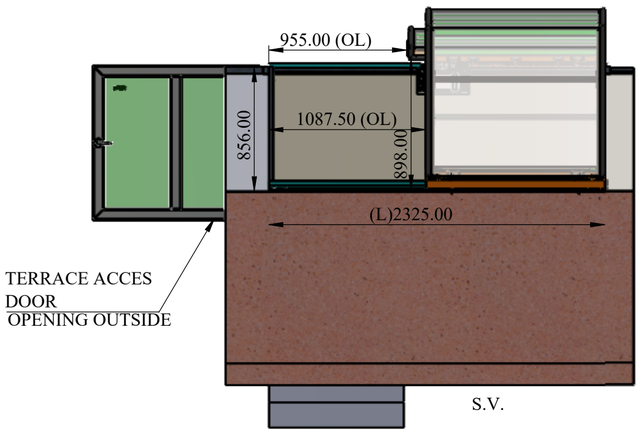


S.V.

OPEN VIEW

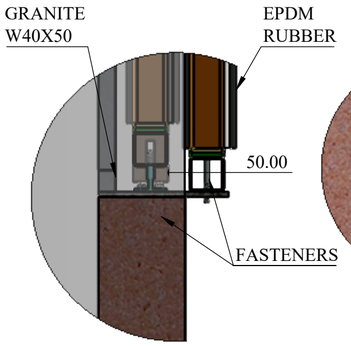

DETAIL C
SCALE 1 : 10

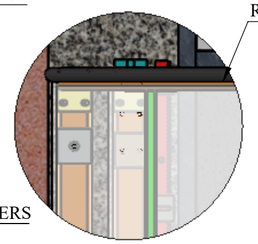

DETAIL D
SCALE 1 : 10

REV DESCRIPTION	DATE	REV NO
	13-10-2026	REV 00
1.		

NOTE :

THIS DRAWING IS FOR CLIENT APPROVAL
REQ TRACK MOUNTING BASE STRUCTURE IN CLIENT SCOPE
EPDM RUBBER FLAPPER ARE PROVIDED FOR PROPER WATER SEAL & AIR SEAL
TOTAL SYSTEM WEIGHT IS - 2,040KG.

SPECIAL INSTRUCTION'S :

This drawing & design is the property of NIHVA TECHONOLOGIES PVT. LTD. Not to be sold or copied to any other concern

TITLE - ROOF AUTOMATION

DWG NO - NTPL-

NIHVA Technologies Pvt. Ltd.


NIHVA TECHNOLOGIES PVT.LTD.PUNE
Website - www.nihva.com


	NAME	SIGNATURE	DATE
DRAWN	V.W.		13-10-2026
CHK'D	S.P.		15-10-2026
APPV'D	V.T.		15-10-2026


PRODUCT - L SHAPE ENCLOSURE
CLIENT NAME - LODHA GROUP.
SITE LOCATION - MUMBAI - VIKROLI.
MATRIAL - QTY - 1


If any queries contact - info@nihva.com
ALL DIMENSION ARE IN mm
A2
PROJECTION METHOD:
SCALE :
SHEET 1 OF 2


DRAWING

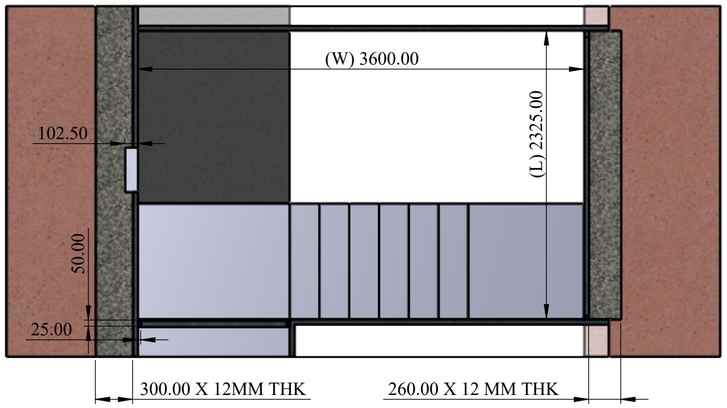

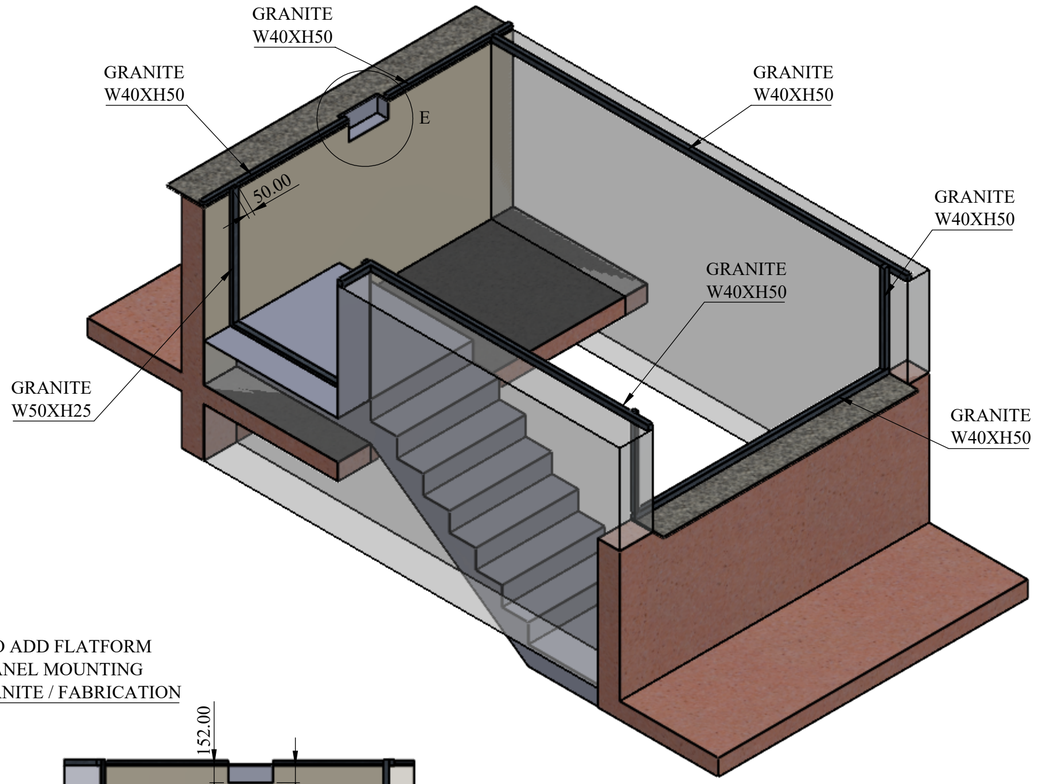

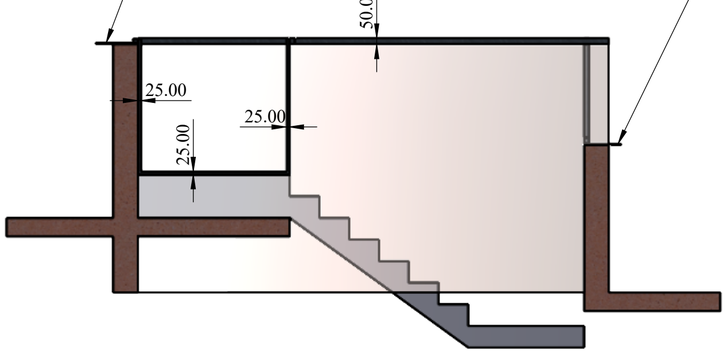

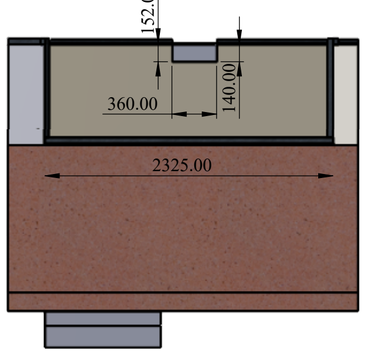

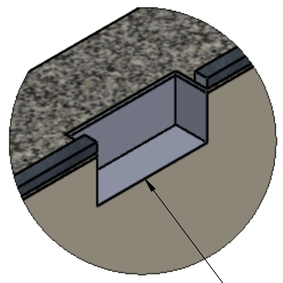

DETAIL E
SCALE 1 : 10

REV DESCRIPTION	DATE	REV NO
	13-10-2026	REV 00
1.		

NOTE :

CIVIL DRAWING
BASE STRUCTURE IN CLIENT SCOPE

SPECIAL INSTRUCTION'S :

REQ TO ADD FLATFORM FOR PANEL MOUNTING
IN GRANITE / FABRICATION
IT IS IN CLIENT SCOPE.

This drawing & design is the property of NIHVA TECHONOLOGIES PVT. LTD. Not to be sold or copied to any other concern

TITLE - ROOF AUTOMATION

DWG NO - NTPL-

NIHVA TECHNOLOGIES PVT.LTD.PUNE
Website - www.nihva.com

	NAME	SIGNATURE	DATE
DRAWN	V.W.		13-10-2026
CHK'D	S.P.		15-10-2026
APPV'D	V.T.		15-10-2026

PRODUCT - L SHAPE ENCLOSURE
CLIENT NAME - LODHA GROUP.
SITE LOCATION - MUMBAI - VIKROLI.
MATRIAL -
QTY - 1
If any queries contact - info@nihva.com
PROJECTION METHOD:
SCALE :
ALL DIMENSION ARE IN mm
A2
SHEET 2 OF 2