

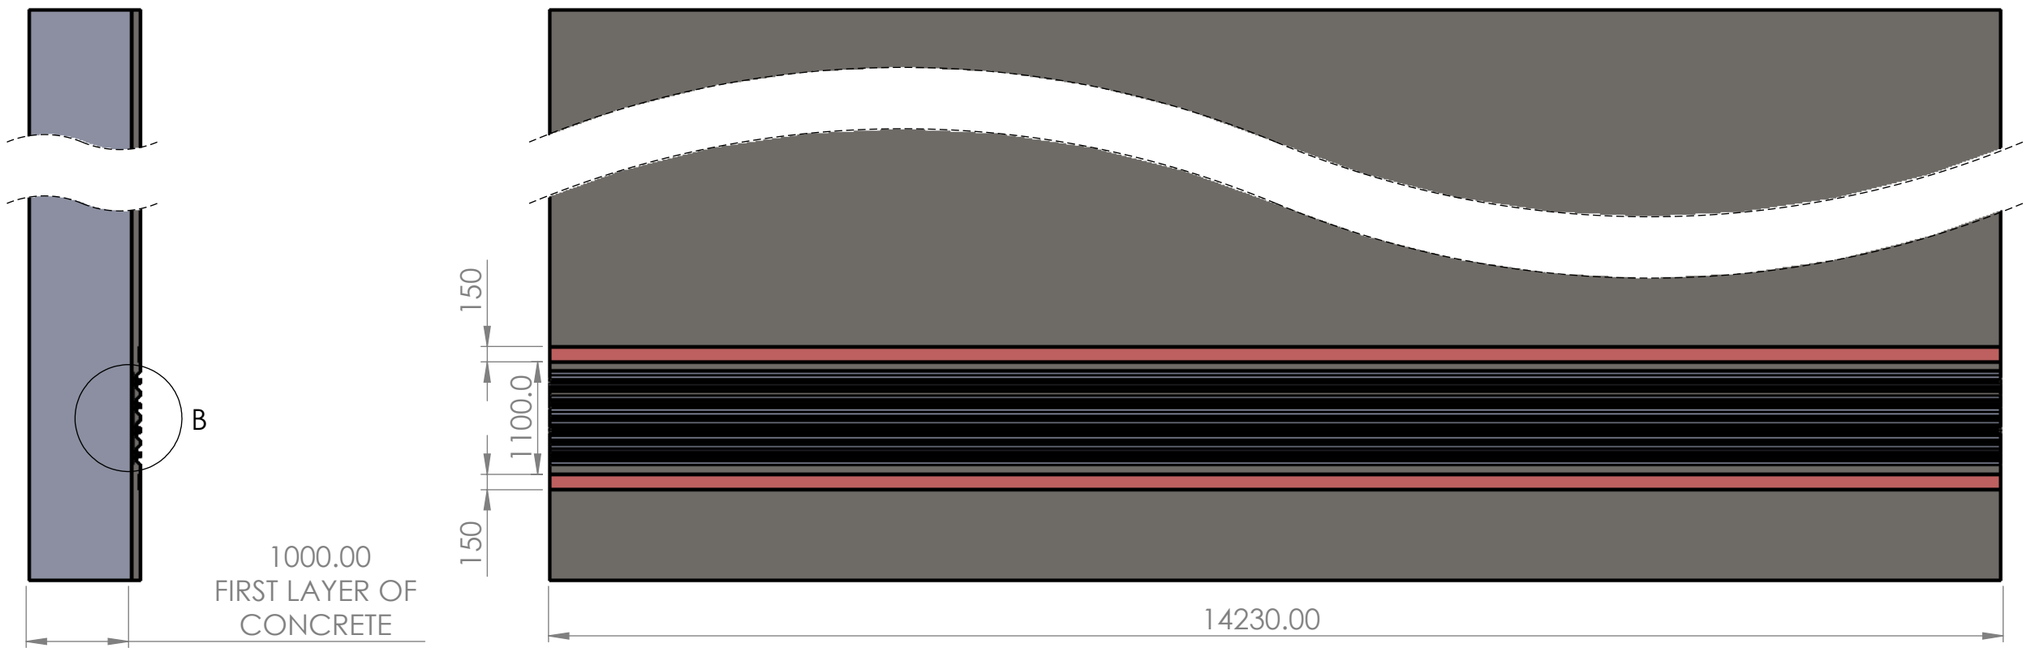


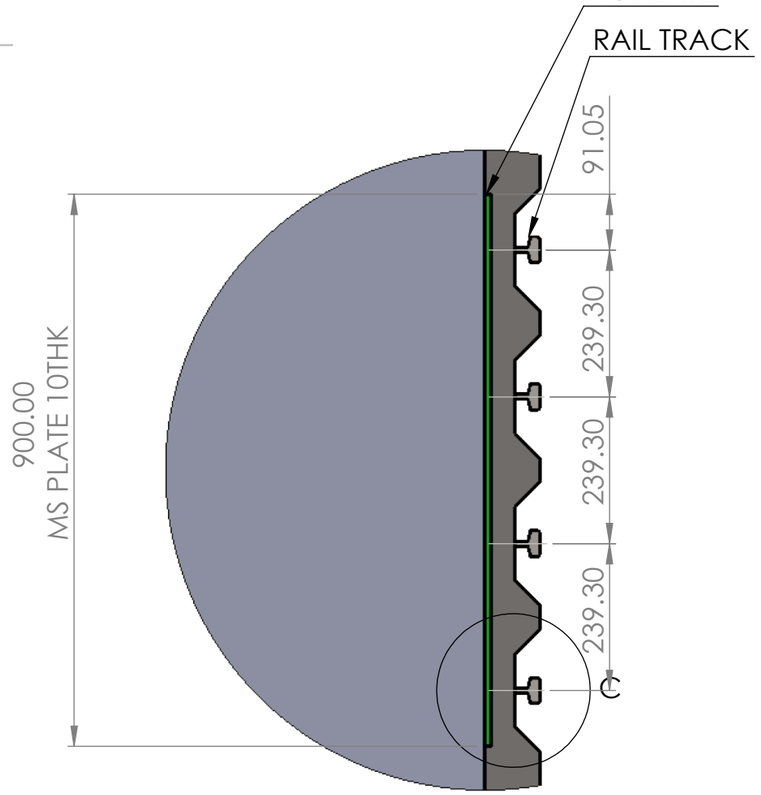

DETAIL B
SCALE 1 : 10

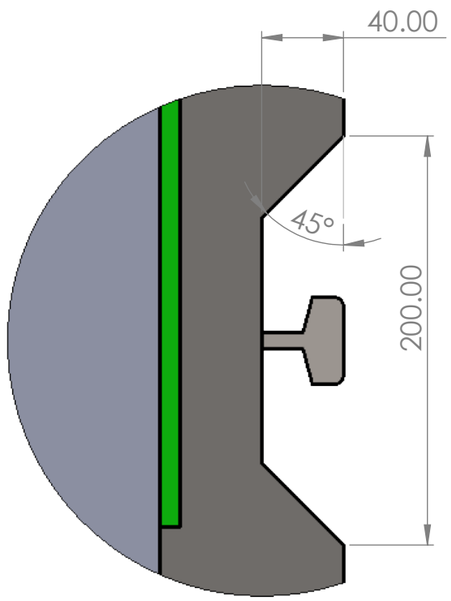

DETAIL C
SCALE 1 : 3

NOTE -

1) CREATE 1000 MM CONCRETE LAYER.
2) ABOVE CONCRETE PUT MS PLATE GIVEN AS PER OUR LAYOUT DRAWNG.
3) ABOVE MS PLATE WELD THE RAIL TRACK AS PER DRAWING.
4) AFTER RAIL TRACK WELDING THEN SECOND LAYER OF CONCRETE IS CREATED AS PER DRAWING.

TITLE : FOUNDATION DRAWING

NIHVA TECHNOLOGIES PVT LTD

	NAME	SIGNATURE	DATE
DRAWN	SURAJ.W		21-01-2025
CHK'D	SURAJ.W		21-01-2025
APPV'D	VIJAY T.		21-01-2025

DIMENSIONS ARE IN MILLIMETERS

CLIENT NAME : ISRO ALUVA, KERAL

PRODUCT NAME : TELESCOPIC HANGER SLIDING DOOR

SITE LOCATION : ALUVA,KERAL

DWG NO. FOUNDATION DRAWING — A3

REVISION : 0

SCALE:

SHEET 1 OF 1