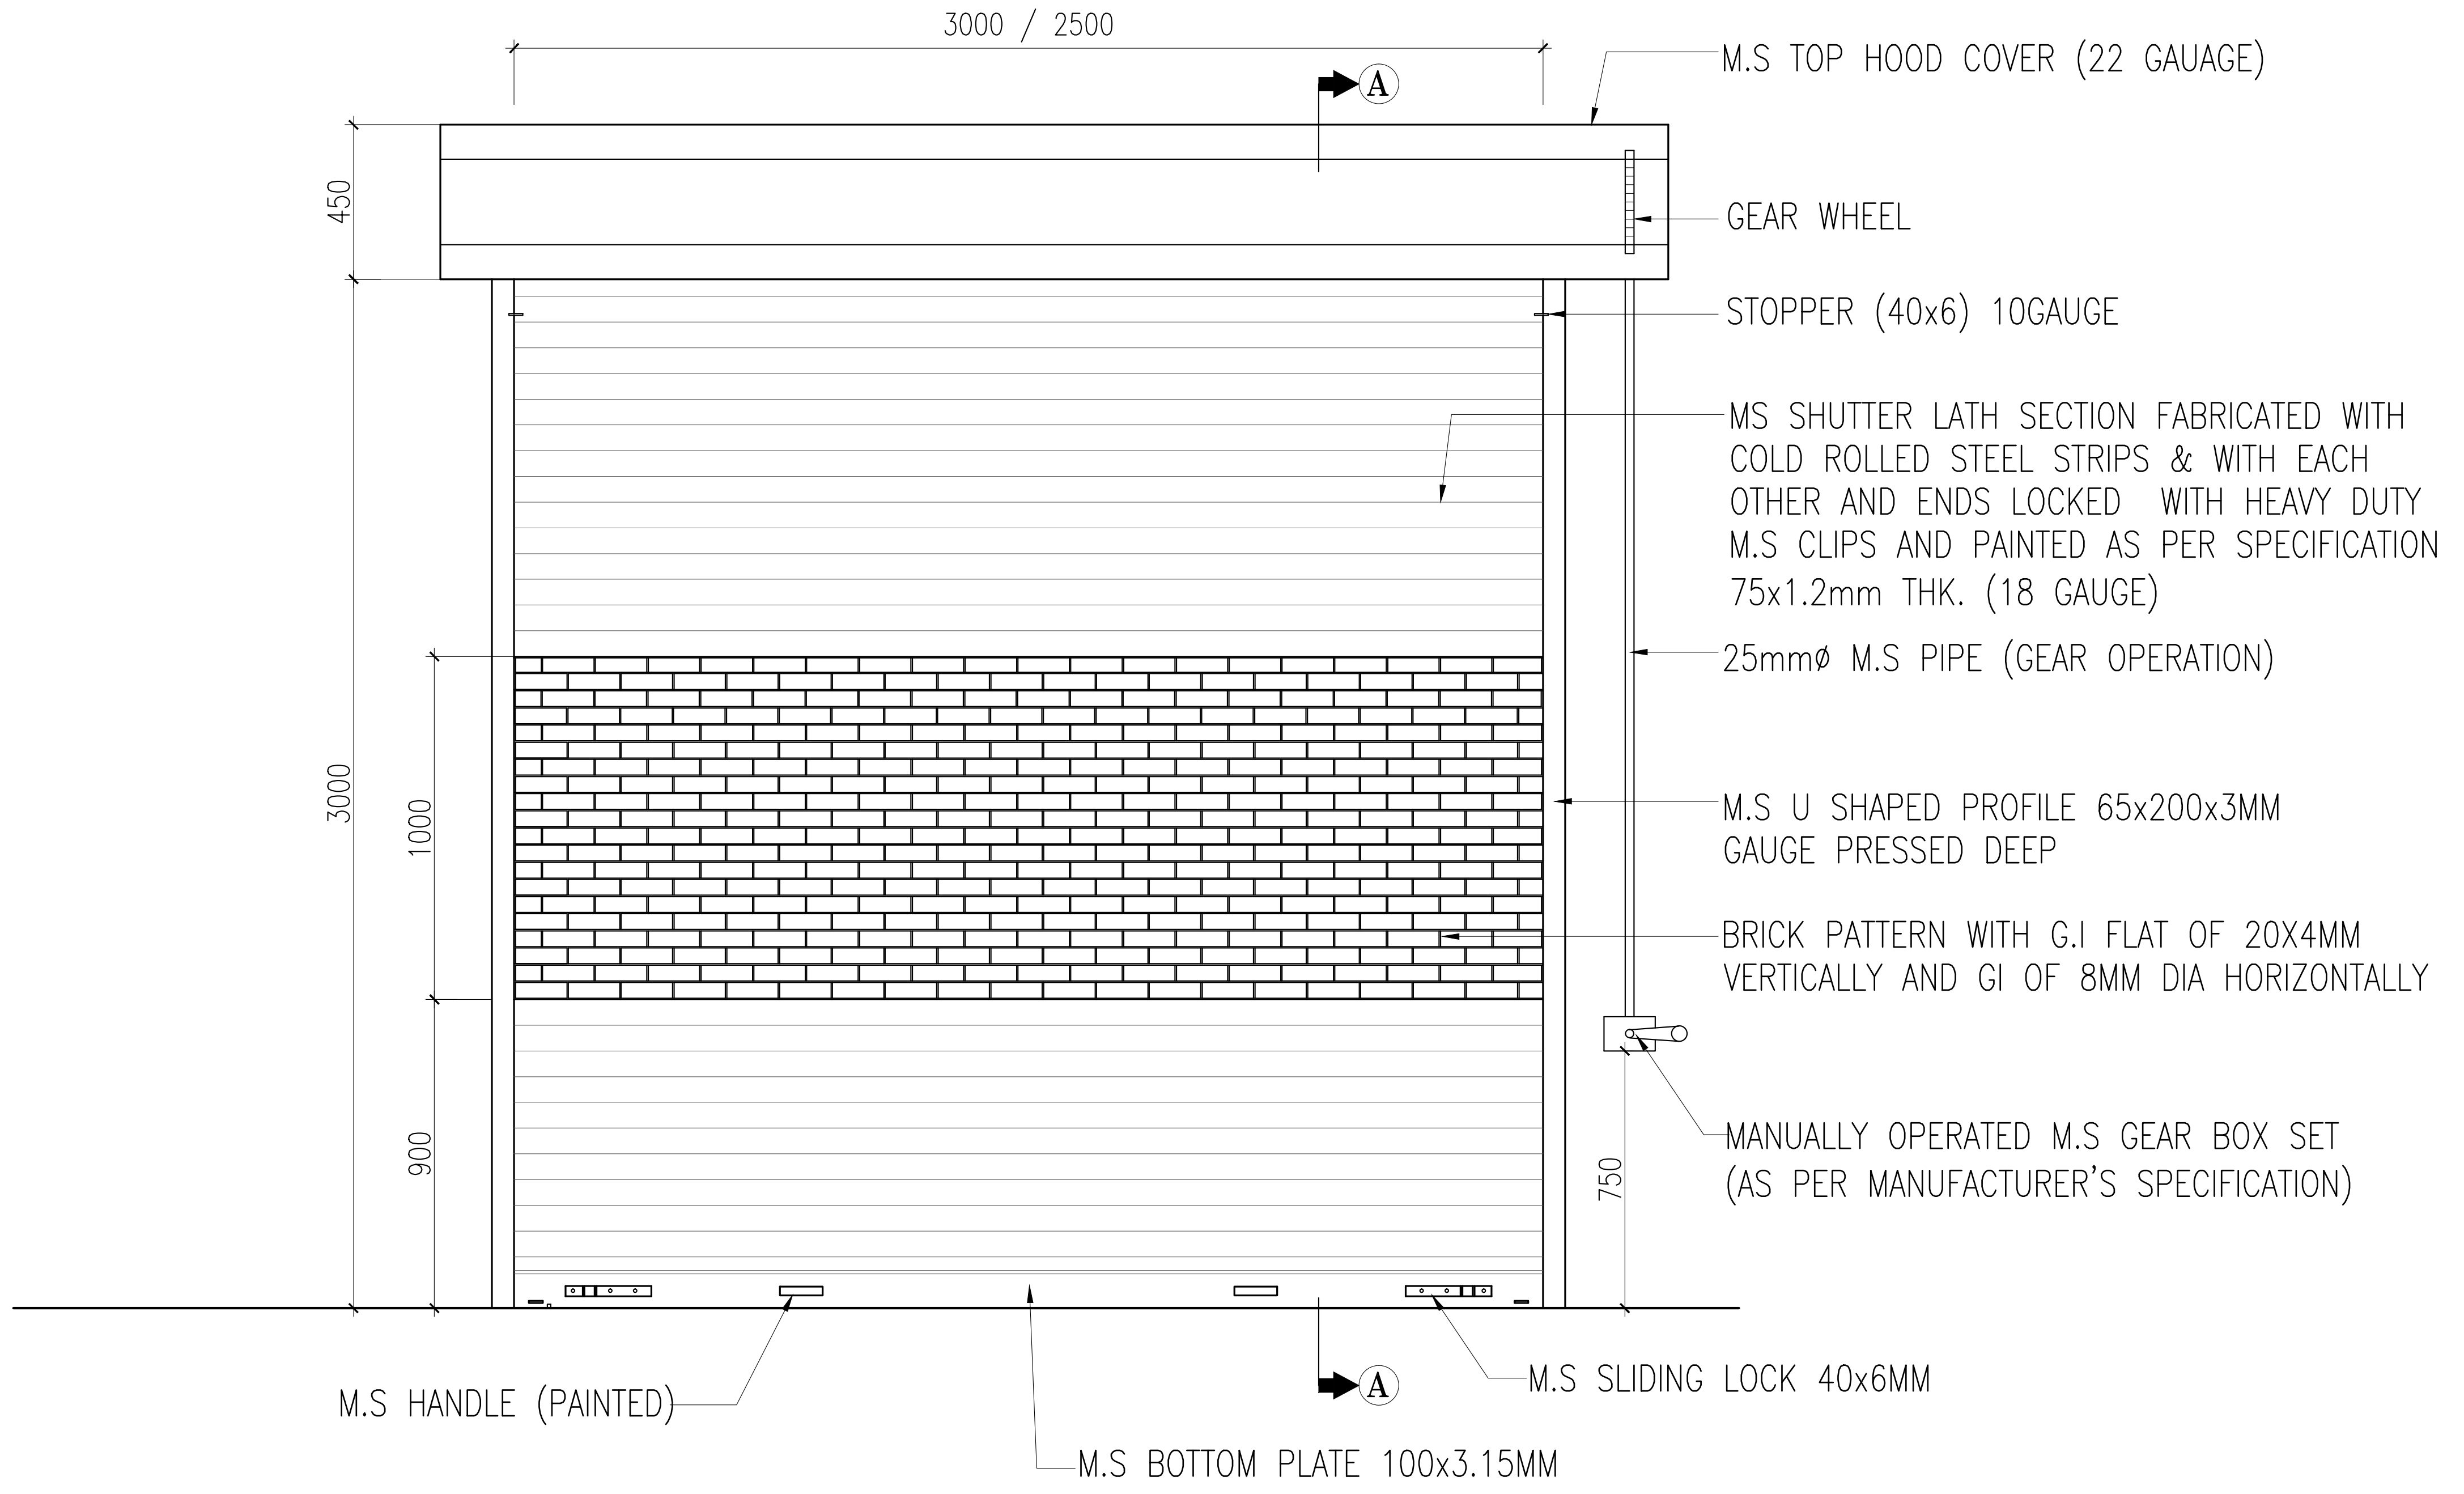
3000 / 2500
A
M.S TOP HOOD COVER (22 GAUAGE)
450
GEAR WHEEL
STOPPER (40x6) 10GAUGE
MS SHUTTER LATH SECTION FABRICATED WITH COLD ROLLED STEEL STRIPS & WITH EACH OTHER AND ENDS LOCKED WITH HEAVY DUTY M.S CLIPS AND PAINTED AS PER SPECIFICATION 75x1.2mm THK. (18 GAUGE)
25mmø M.S PIPE (GEAR OPERATION)
3000
1000
M.S U SHAPED PROFILE 65x200x3MM GAUGE PRESSED DEEP
BRICK PATTERN WITH G.I FLAT OF 20X4MM VERTICALLY AND GI OF 8MM DIA HORIZONTALLY
900
750
MANUALLY OPERATED M.S GEAR BOX SET (AS PER MANUFACTURER'S SPECIFICATION)
M.S HANDLE (PAINTED)
A
M.S SLIDING LOCK 40x6MM
M.S BOTTOM PLATE 100x3.15MM

ELEVATION OF GRILLED ROLLING SHUTTER

SUBSTATION - 3000X3000 2500X3000

FIRE SUMP - 3000X3000

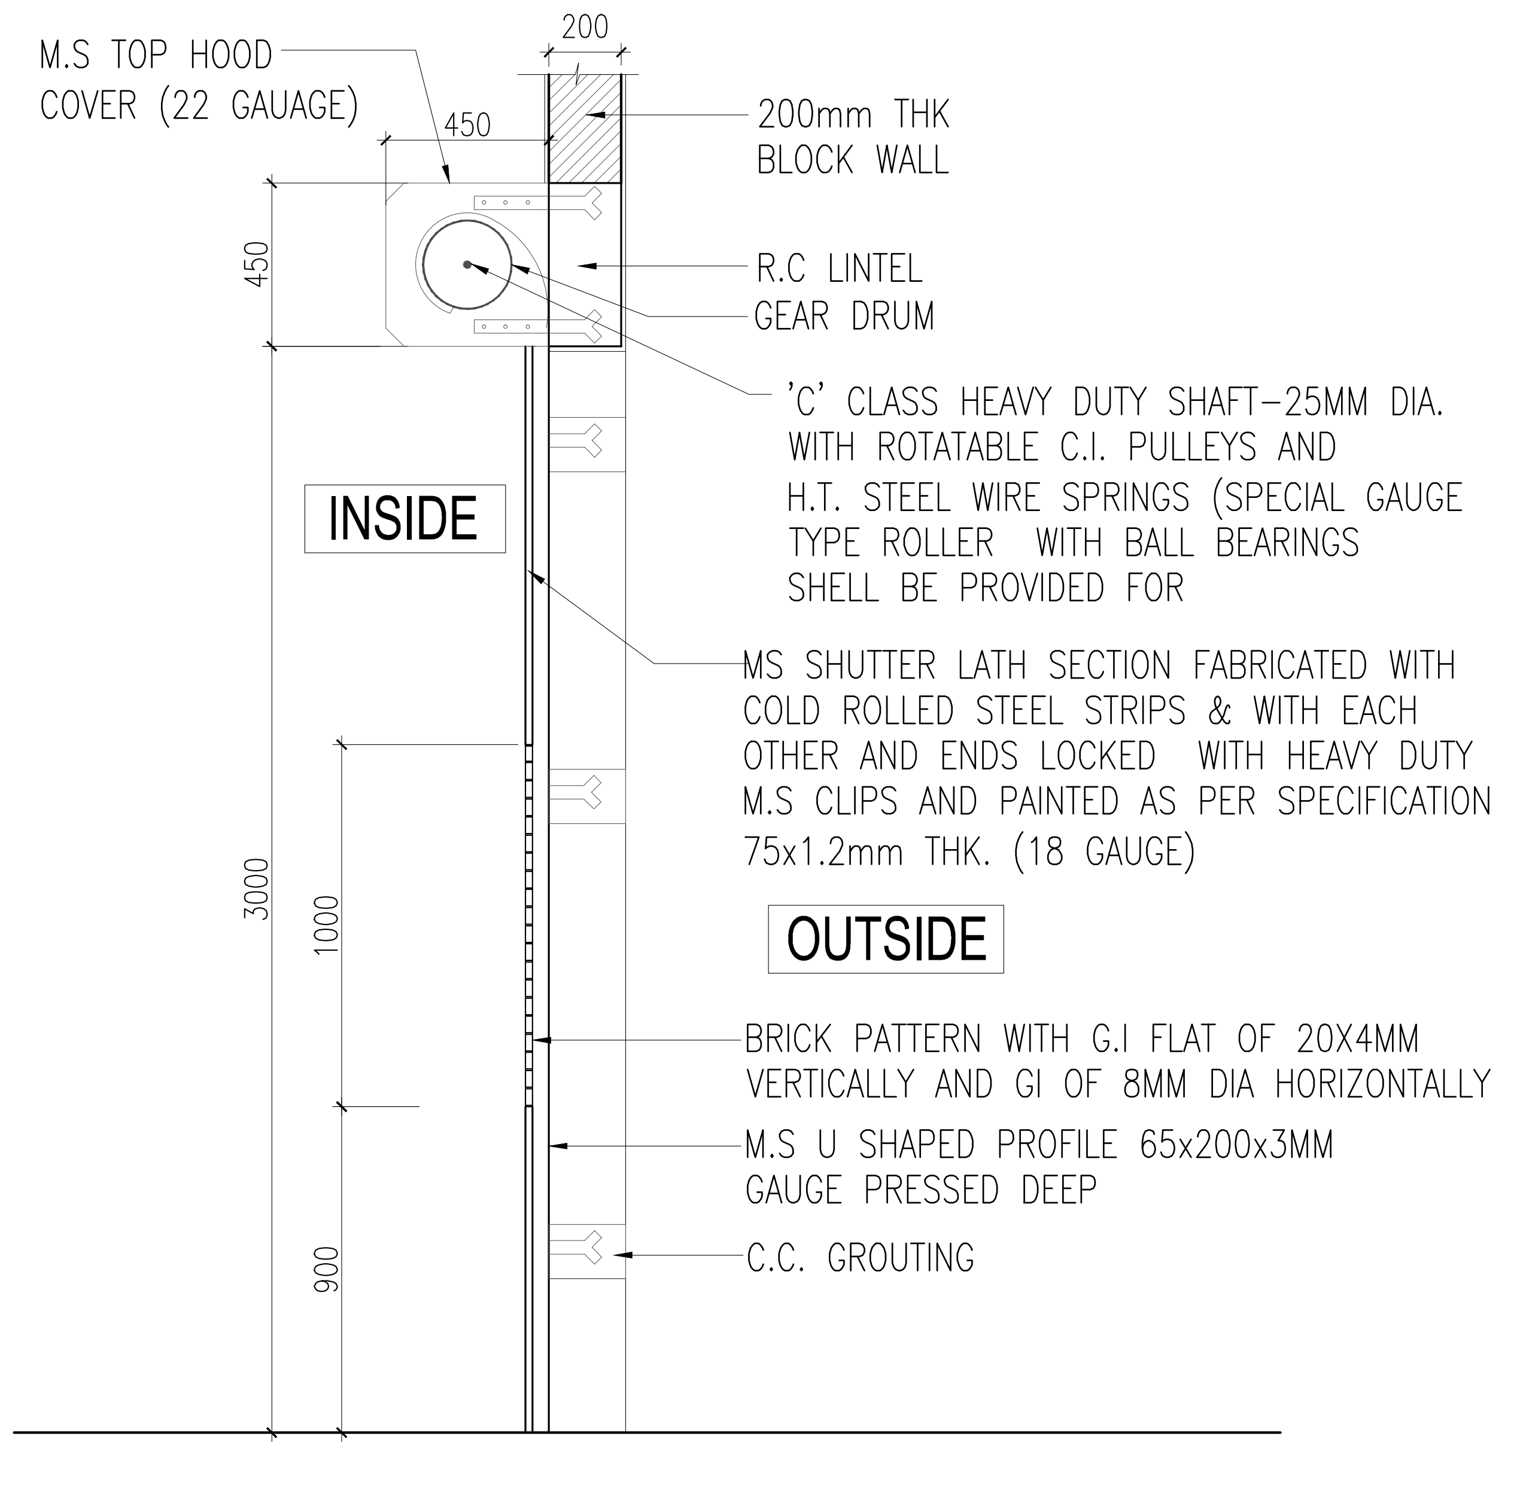
M.S TOP HOOD COVER (22 GAUAGE)
200
450
200mm THK BLOCK WALL
450
R.C LINTEL
GEAR DRUM
'C' CLASS HEAVY DUTY SHAFT-25MM DIA. WITH ROTATABLE C.I. PULLEYS AND H.T. STEEL WIRE SPRINGS (SPECIAL GAUGE TYPE ROLLER WITH BALL BEARINGS SHELL BE PROVIDED FOR
INSIDE
MS SHUTTER LATH SECTION FABRICATED WITH COLD ROLLED STEEL STRIPS & WITH EACH OTHER AND ENDS LOCKED WITH HEAVY DUTY M.S CLIPS AND PAINTED AS PER SPECIFICATION 75x1.2mm THK. (18 GAUGE)
OUTSIDE
3000
1000
BRICK PATTERN WITH G.I FLAT OF 20X4MM VERTICALLY AND GI OF 8MM DIA HORIZONTALLY
M.S U SHAPED PROFILE 65x200x3MM GAUGE PRESSED DEEP
900
C.C. GROUTING

SECTION AT AA

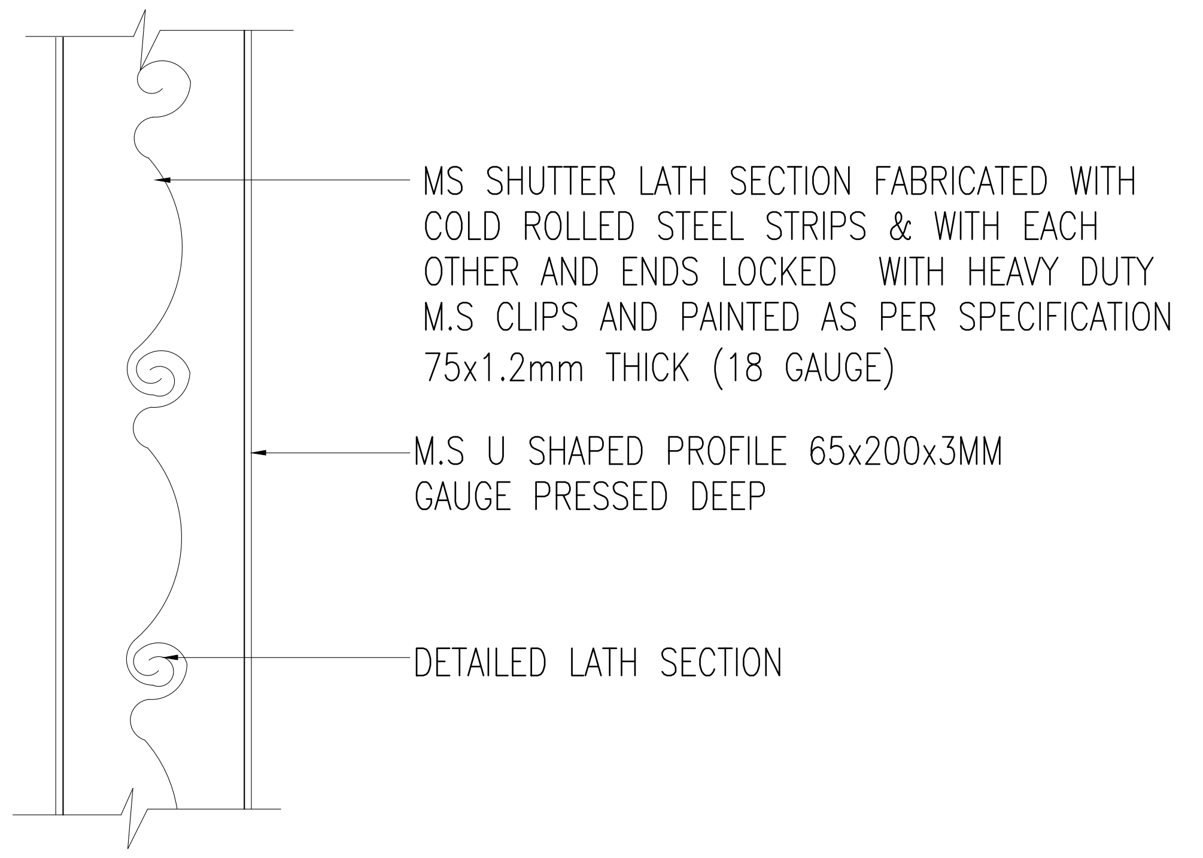
MS SHUTTER LATH SECTION FABRICATED WITH COLD ROLLED STEEL STRIPS & WITH EACH OTHER AND ENDS LOCKED WITH HEAVY DUTY M.S CLIPS AND PAINTED AS PER SPECIFICATION 75x1.2mm THICK (18 GAUGE)
M.S U SHAPED PROFILE 65x200x3MM GAUGE PRESSED DEEP
DETAILED LATH SECTION

DETAIL-A

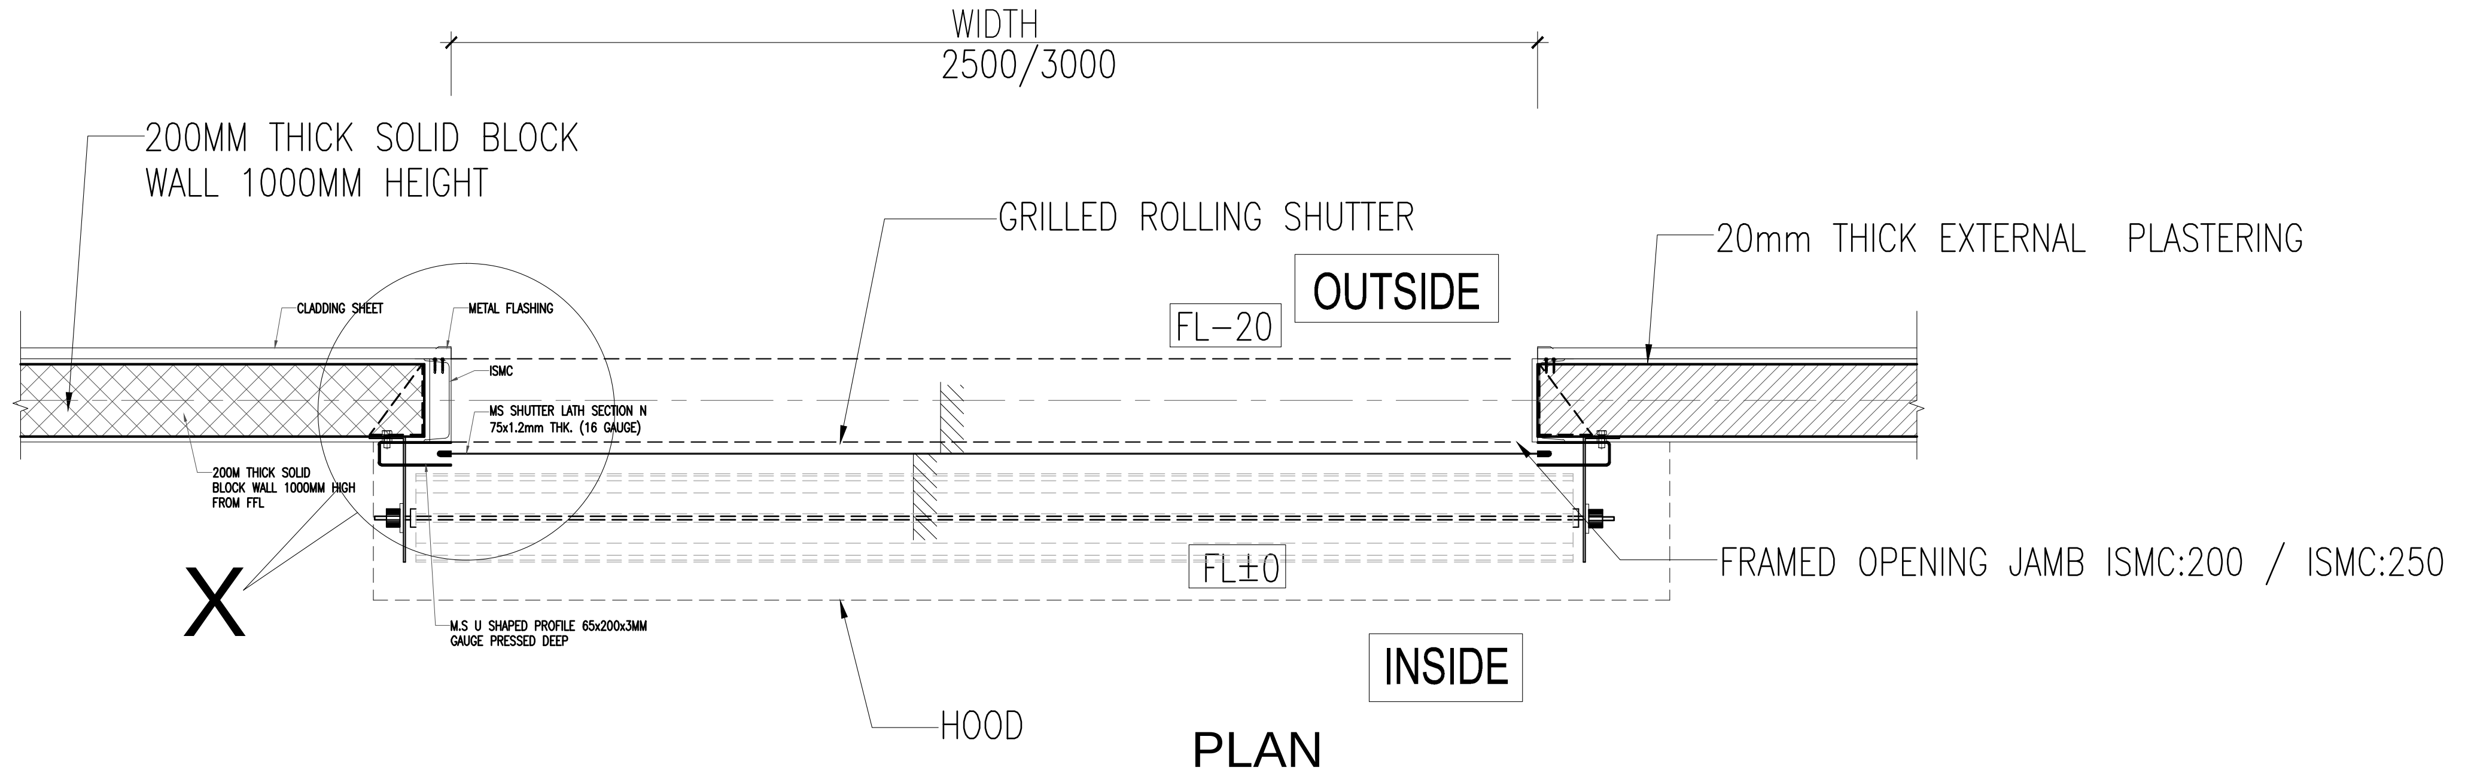
WIDTH
2500/3000
200MM THICK SOLID BLOCK WALL 1000MM HEIGHT
GRILLED ROLLING SHUTTER
20mm THICK EXTERNAL PLASTERING
OUTSIDE
FL-20
CLADDING SHEET
METAL FLASHING
ISMC
MS SHUTTER LATH SECTION N 75x1.2mm THK. (16 GAUGE)
200M THICK SOLID BLOCK WALL 1000MM HIGH FROM FFL
X
M.S U SHAPED PROFILE 65x200x3MM GAUGE PRESSED DEEP
FL±0
FRAMED OPENING JAMB ISMC:200 / ISMC:250
INSIDE
HOOD

PLAN

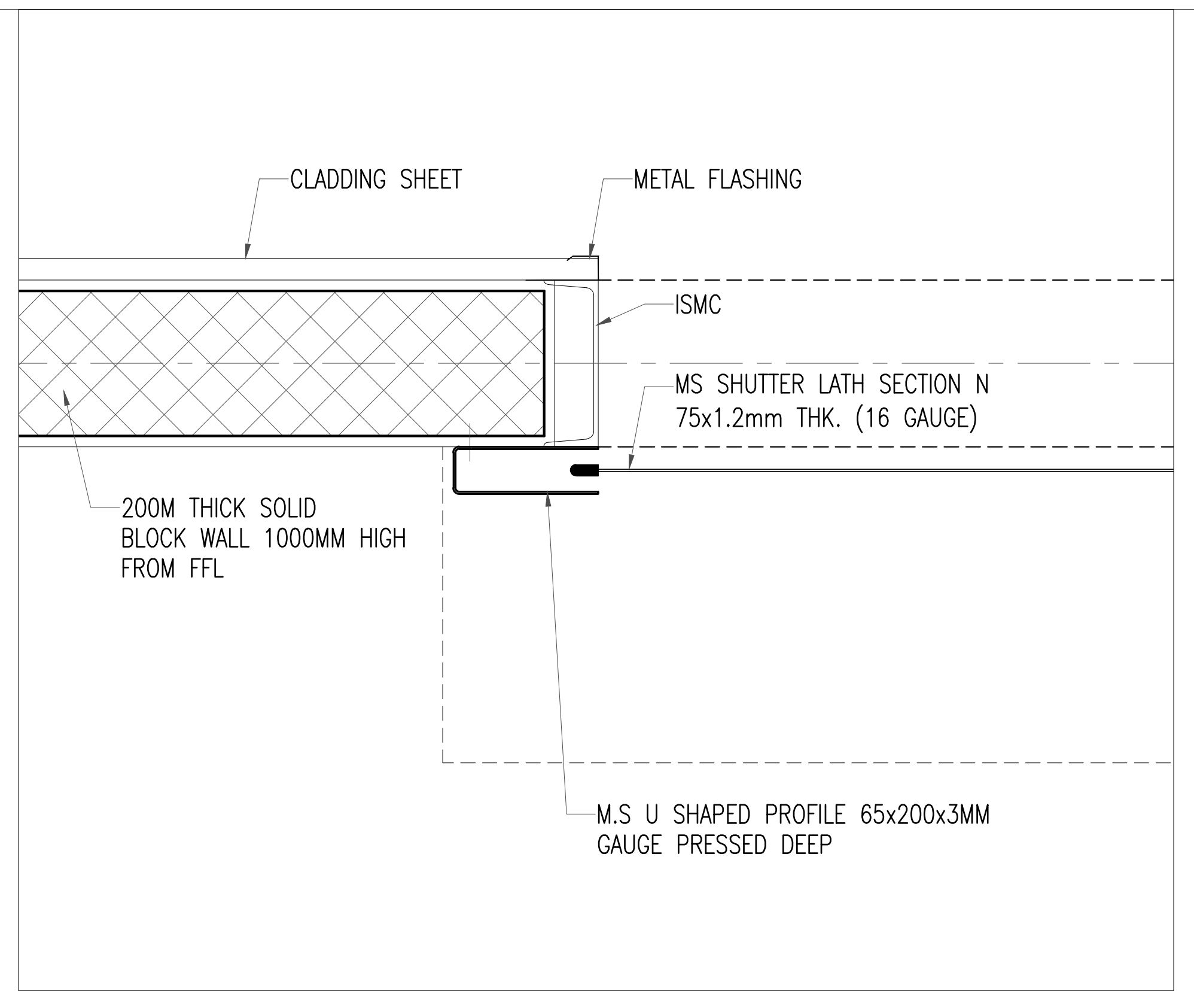
CLADDING SHEET
METAL FLASHING
ISMC
MS SHUTTER LATH SECTION N 75x1.2mm THK. (16 GAUGE)
200M THICK SOLID BLOCK WALL 1000MM HIGH FROM FFL
M.S U SHAPED PROFILE 65x200x3MM GAUGE PRESSED DEEP

DETAIL-X

KEY PLAN

LEGEND :-

GENERAL NOTES :

ALL DIMENSIONS ARE IN MILLIMETRES AND ARE UNFINISHED DIMENSIONS UNLESS OTHERWISE SPECIFIED.

ALL LEVELS ARE IN METRES AND ARE UNFINISHED LEVELS UNLESS OTHERWISE SPECIFIED.

DO NOT SCALE DRAWINGS. ONLY WRITTEN DIMENSIONS SHALL BE FOLLOWED, ANY DISCREPANCIES NOTED SHALL BE BROUGHT TO THE NOTICE OF THE ARCHITECT PRIOR TO EXECUTION.

REV.	DESCRIPTION	DATE	BY	CHD.
T1	ISSUED FOR CIVIL TENDER	15.03.14	KM	GBK

AMENDMENT

GRAPHIC SCALE:

0 1M 4M 8M

1M 0 2M 6M 10M

CLIENT:

M/S. INGERSOLL RAND (INDIA) LTD.

PROJECT:

PROPOSED FACTORY FOR INGERSOLL RAND (INDIA) LIMITED AT AHMEDABAD

DRAWING TITLE:

SUB STATION
GRILLED ROLLING SHUTTER DETAIL

SCALE : 1:20
DRAWN : KM
DATE : 11.03.14
CHKD : BERNARD

DRAWING NO:

IRA-FAC-AR10-GR-01-177307

T1

ARCHITECTURE ◦ INTERIOR DESIGN ENGINEERING PLANNING CONSTRUCTION MANAGEMENT

CRN

C R NARAYANA RAO

10, KARPAGAMBAL NAGAR,
MYLAPORE, CHENNAI-600 004

B.Arch. (Hons.), M.Arch., (Calif.), F.I.I.A., Intl.Assoc.A.I.A.,
Registered Architect.

FACTORY

Construction work shall be executed only as per the latest revision drawing. Once a revision drawing is issued, the validity of the previous revision drawing stands cancelled and as such construction shall not be carried out as per superseded revisions. The Contractor is expected to:
1. Maintain a register of Drawing Receipts, listing drawing number & revision number, title, from whom received, date received, number of copies received, details of transmittal from the issuer & any other relevant details to be advised from time to time.
2. Archive all previous revision issues immediately upon receipt of a new revision and no superseded drawing shall remain in the site of works except in the Contractor's archives for record and reference purposes only.
3. While archiving superseded drawing, the Contractor is expected to stamp all previously issued drawings / prints appropriately, mentioning the date and revision number of the new revision on account of which the previous revision is archived.
4. The Contractor shall allow the representative of Client / PMC / Architect to inspect Contractor's archives for ensuring compliance.
5. Any work carried out by the Contractor using a superseded drawing after the issue of a new revision is liable for rejection and reinstatement as per new revision at Contractor's risk and cost without any entitlement to extension of time

THESE DRAWINGS ARE UNDER COPYRIGHT AND ARE THE PROPERTY OF CRN. NONE OF THE DRAWINGS AND RELATED DOC-
-UMENTS CAN BE REPRODUCED, COPIED IN WHOLE OR IN PART WITHOUT PRIOR EXPRESSED WRITTEN CONSENT OF CRN.
THESE DRAWINGS CANNOT BE HANDED OVER TO A THIRD PARTY OR USED FOR ANY PURPOSE, OTHER THAN THAT FOR
WHICH IT HAS BEEN LOANED. AFTER FULFILLING THE PURPOSE OF ISSUE THE DRAWINGS SHALL BE RETURNED TO CRN.