


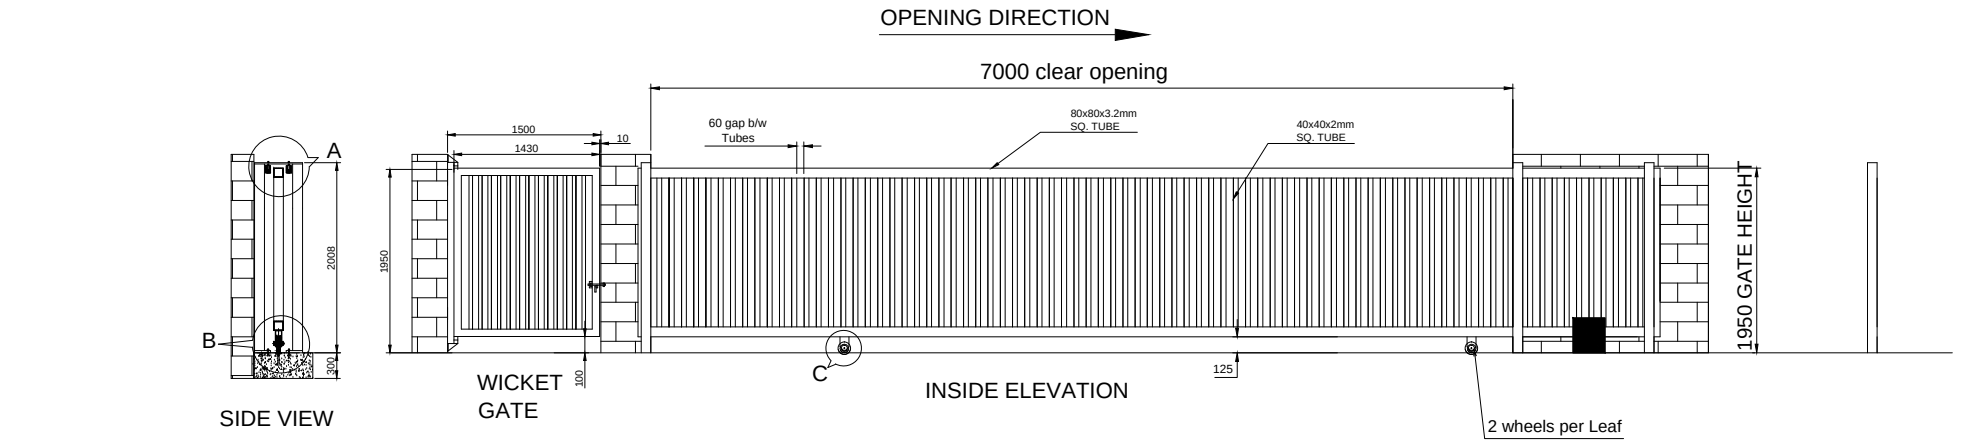


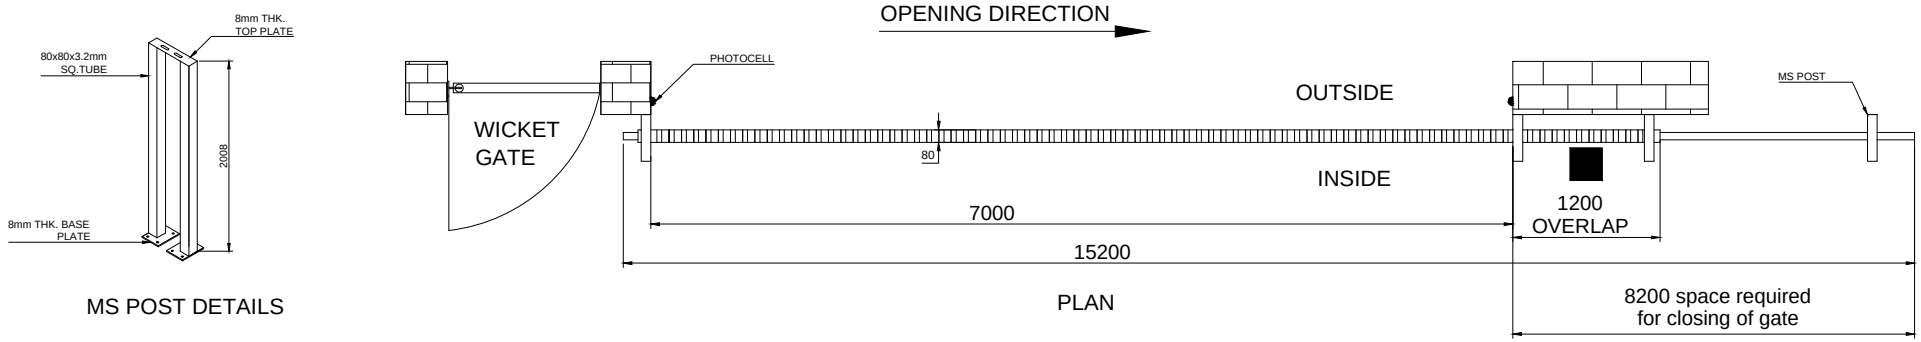


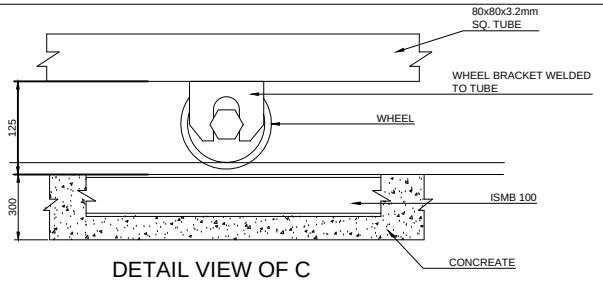

DETAIL VIEW OF C

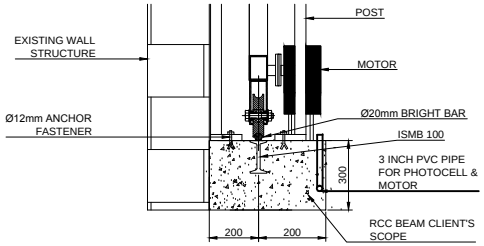

DETAIL VIEW OF B

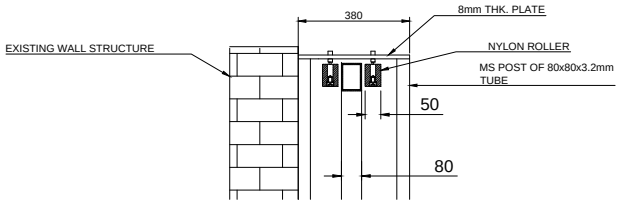

DETAIL VIEW OF A

MOTORISED SINGLE LEAF SLIDING GATE & WICKET GATE				
DESCRIPTION	CLEAR WIDTH	OVERALL WIDTH	CLEAR HEIGHT	QTY.
SLIDING GATE	7000	8200	1950	1 NOS
WICKET GATE	1500		1950	1 NOS
NOTE- ALL REQUIRED CIVIL WORK WILL BE IN CLIENT'S SCOPE.				

This drawing & designing is the property of NIHVA TECHNOLOGIES. Not be sold or copy to any other concern.

TITLE	SINGLE LEAF MOTORIZED SLIDING GATE	NIHVA TECHNOLOGIES PVT. LTD.	NIHVA TECHNOLOGY PVT. LTD. PUNE Tel : 020 66304033 Email:- info@nihva.com Website:- www.nihva.com
	SIGN	DATE	
DRAWN	OMKAR	21/06/16	CLIENT - MAHENDRA WINDOOR SOLUTIONS
CHECK	ANIL	21/06/16	PROJECT - AUROBINDO PHARMA LIMITED
REV.	01		SITE -
APPROVAL			DWG. NO. : NIHVA/16-17/0026/R01
If any queries contact : projects@nihva.com			SCALE: NTS / WT: / SHEET: 01 OF 01
ALL DIMENSION ARE IN mm			