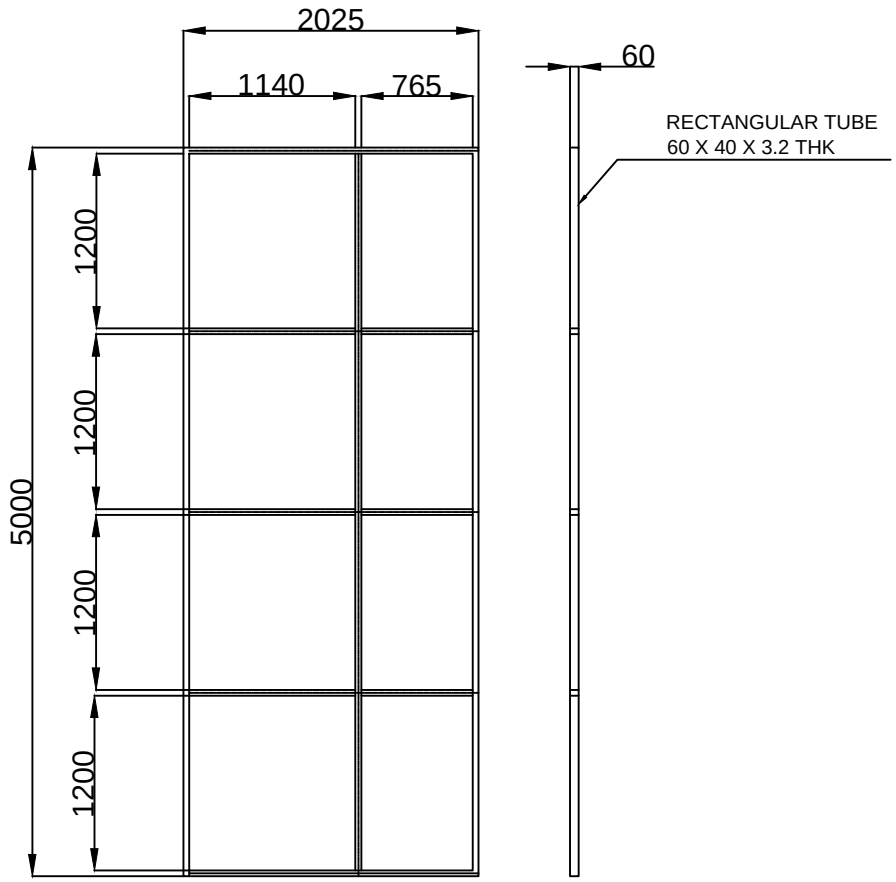

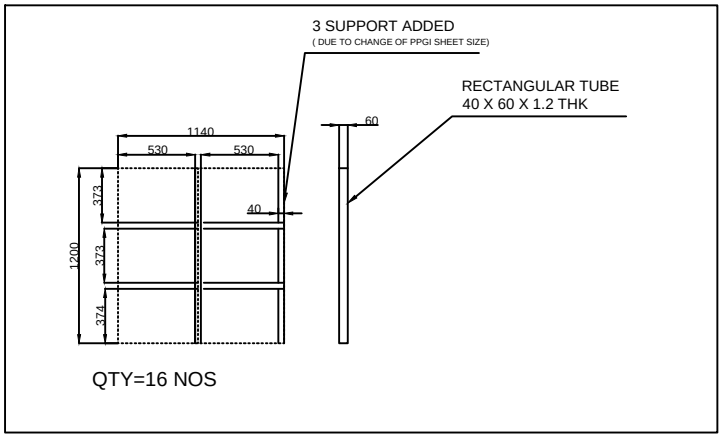

QTY=16 NOS

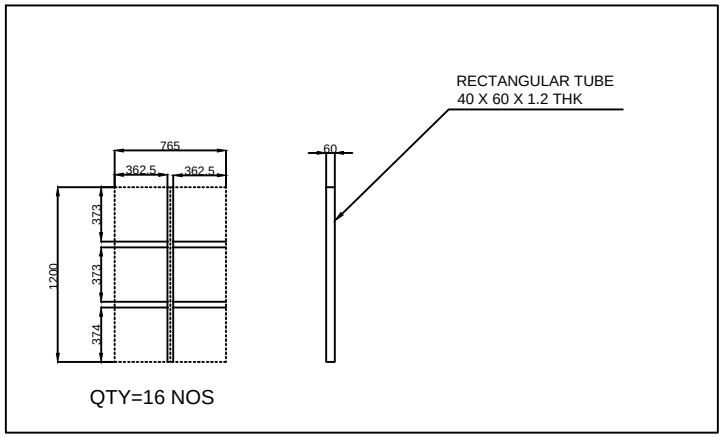

QTY=16 NOS

QTY=04 NOS

CRM DOOR 01

		Date	Revised By

This drawing & design is the property of NIHVA TECHNOLOGIES. Not to be sold or copied to any other concern.

TITLE:- 4 LEAF RH CRM DOOR 01				NIHVA TECHNOLOGIES PVT. LTD. PUNE Tel : 020 66304033 Email:- info@nihva.com Website:- www.nihva.com	
	NAME	DATE	SIGN		
DRAWN	KISHAN	03/05/2022		CLIENT - LESTECH	
CHECK	M.SUTAR	03/05/2022		LOCATION - POSCO MANGAON	
APPRD.				PRODUCT - SLIDING DOOR	
If any queries contact : design@nihva.com				DWG NO:-NIHVA/22-23/MFG/0011	REV- 0
ALL DIMENSION ARE IN mm				SCALE: NTS	SCALE:-- 1:1 SHEET: 01 OF 01