
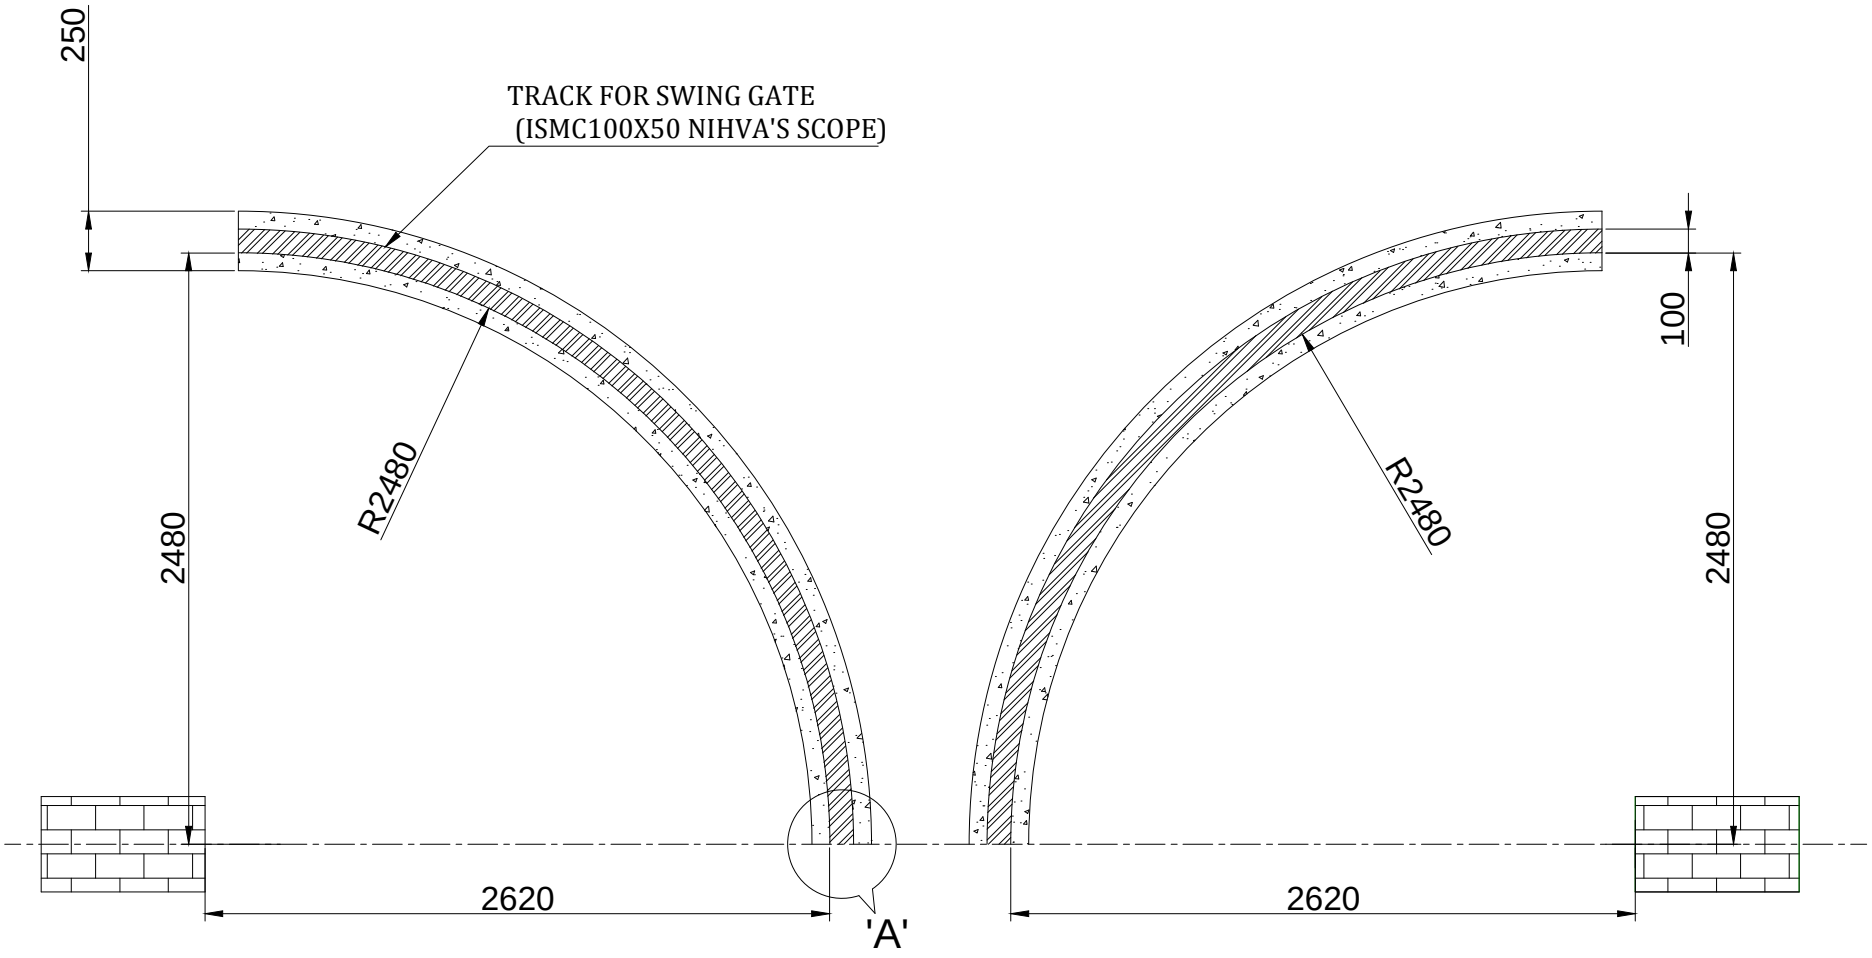


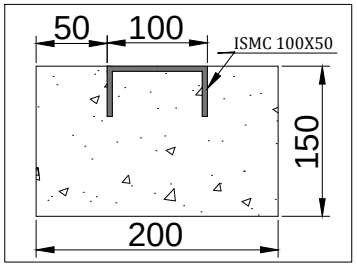

DETAIL VIEW OF 'A'

This drawing & design is the property of NIHVA TECHNOLOGIES. Not to be sold or copied to any other concern.

TITLE
FOUNDATION OF MANUAL
SWING GATE 6X1.8m

NIHVA TECHNOLOGIES PVT. LTD.
NIHVA TECHNOLOGIES
PVT. LTD. PUNE
Tel : 020 66304033
Email:- info@nihva.com
Website:- www.nihva.com

	SIGN	DATE
DRAWN	SURAJ	18/05/17
CHECK	SAGAR P.	18/05/17
REV.		
APPROVAL	S.S	18/05/17

CLIENT - TATA PROJECT
PROJECT - ALSTOM
SITE LOCATION -MADHEPURA,BIHAR
DWG. NO. : NIHVA/17-18/0085

If any queries contact : projects@nihva.com

SCALE: NTS | WT: | SHEET: 01 OF 01

ALL DIMENSION ARE IN mm