




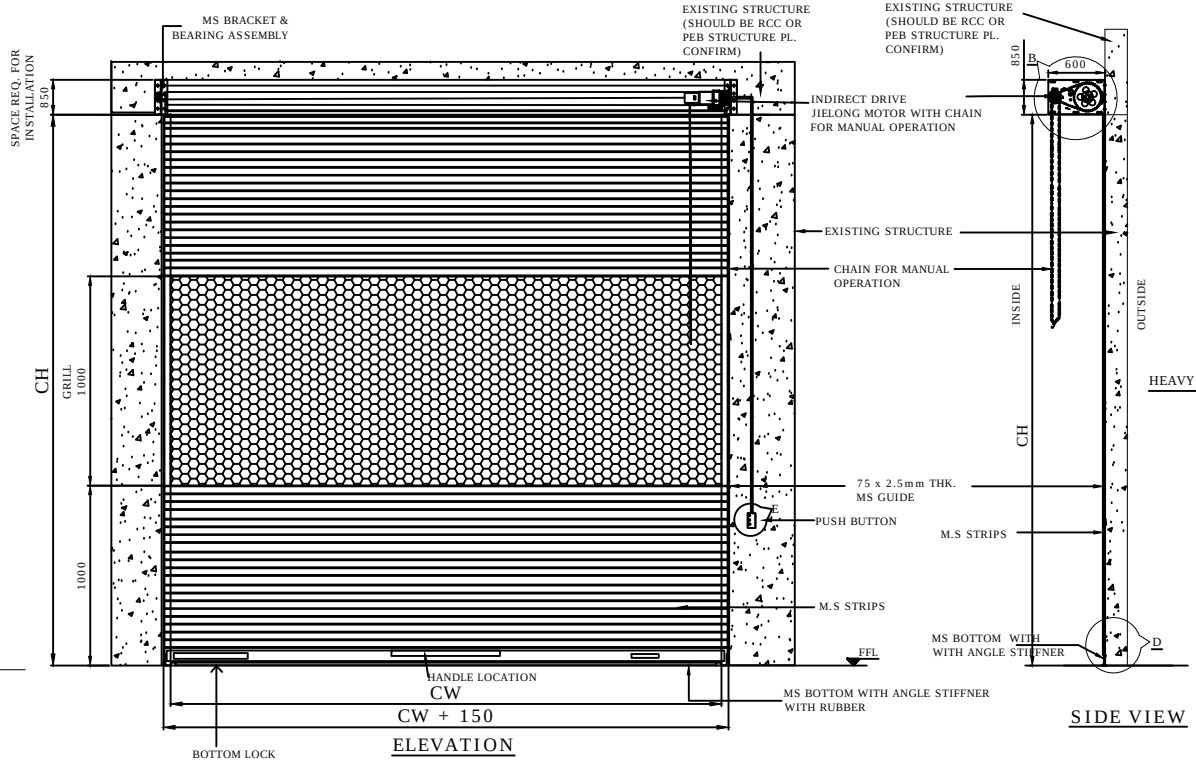


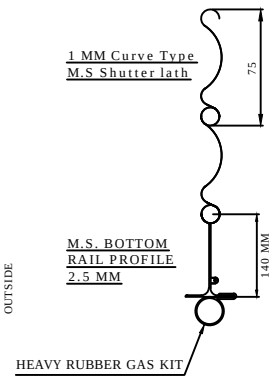


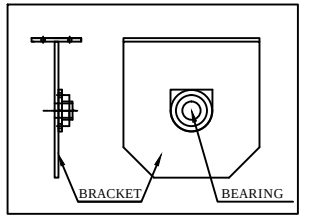

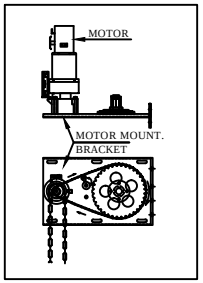

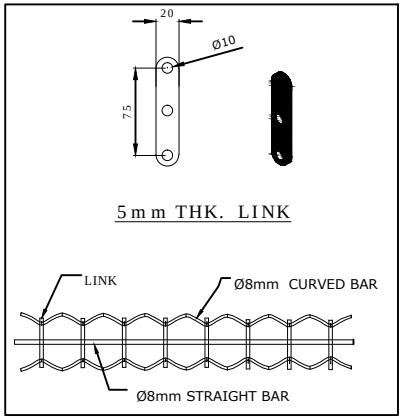

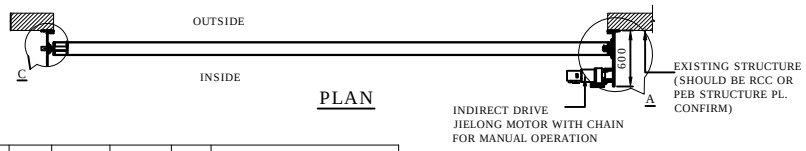

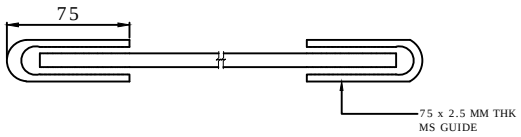

(NOTE: REQUIRED TECHANICAL STRUCTURE FOR SHUTTER IN CLIENT SCOPE)

CLEAR WIDTH (CW)	CLEAR HEIGHT (CH)	QUANTITY
3000	3500	1
3850	3600	1
3000	3600	7
2000	3000	2
4000	3660	2

SR NO	LOCATION	TYPE	CLEAR WIDTH	CLEAR HEIGHT	QTY	SIDE WALL/ SUPPORTING STRUCTURE
6	UTILITY BUILDING	RS2	3000	3600	1	BW
			3000	3600	1	BW
			3000	3600	1	BW
			3000	3600	1	BW
			3000	3600	1	BW
5	DOCK LEVELLER	RS2	3000	3600	2	PEB
4	WARE HOUSE	RS2A	3850	3600	1	PEB
3	PUMP ROOM	RS3	3000	3500	1	PEB
2	OUTGOING SHED	RS5	2000	3000	1	PEB
		RS1	4000	3660	1	PEB
1	INCOMING SHED	RS5	2000	3000	1	PEB
		RS1	4000	3660	1	PEB

This drawing & design is the property of NIHVA TECHNOLOGIES. Not to be sold or copied to any other concern.

TITLE: MOTORIZED ROLLING SHUTTER

	NAME	SIGN	DATE
DRAWN	P.A		05.02.2020
CHECK	G.J		05.02.2020
APPRD.			

If any queries contact : design@nihva.com

ALL DIMENSION ARE IN mm

NIHVA TECHNOLOGIES PVT. LTD.

NIHVA TECHNOLOGIES PVT. LTD. PUNE
Tel : 020 66304033
Email:- info@nihva.com
Website:- www.nihva.com

CLIENT -

PROJECT -

SITE LOCATION -

DWG. NO. : NIHVA/19-20/VDR/308 | REV- R00

SCALE: NTS | WT: | SHEET: