




SECTION A-A'

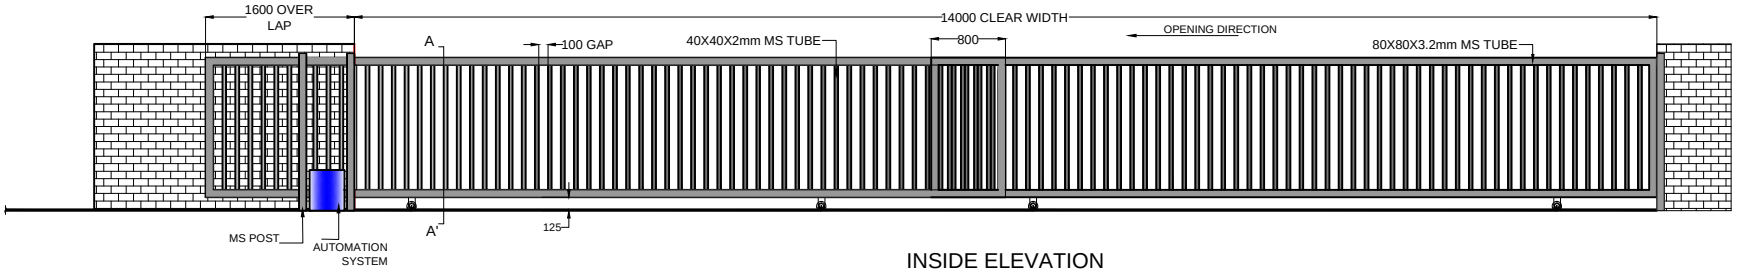


INSIDE ELEVATION

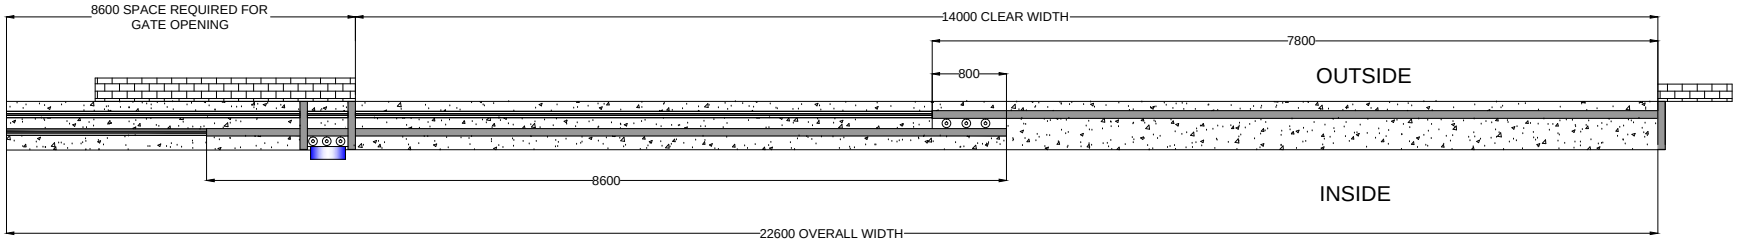

PLAN

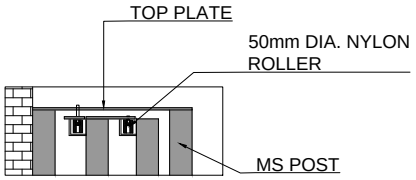

DETAIL VIEW OF B

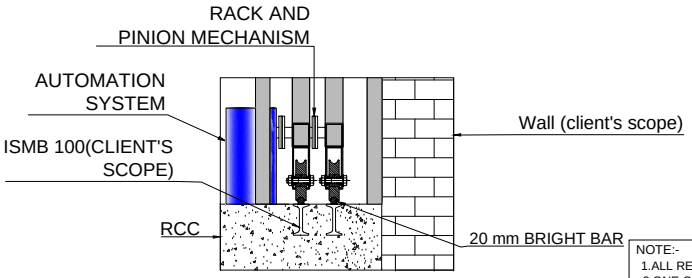

DETAIL VIEW OF A

NOTE:-
1.ALL REQUIRED CIVIL WORK BE IN CLIENTS SCOPE.
2.ONE COAT OF RED OXIDE & TWO COAT OF APPROVED RAL SHADE WILL BE GIVEN TO THE GATE.
3.IF NECESSARY GATE LEAF WILL BE IN TWO PARTS FOR TRANSPORTATION & WILL BE WELD TOGETHER ON SITE.

CLEAR WIDTH	CLEAR HEIGHT	QUANTITY.
14000mm	1500mm	01 NOS

This drawing & designing is the property of NIHVA TECHNOLOGIES. Not to be sold or copied to any other concern.

TITLE: AUTOMATIC DOUBLE LEAF TELESCOPIC GATE

	SIGN	DATE
DRAWN	SURAJ	25/10/17
CHECK	SHEKHAR	25/10/17
REV.		
APPROVAL	SHEKHAR	25/10/17

If any queries contact : projects@nihva.com

ALL DIMENSION ARE IN mm

NIHVA TECHNOLOGIES PVT. LTD.
NIHVA TECHNOLOGIES PVT. LTD. PUNE
Tel : 020 66304033
Email:- info@nihva.com
Website:- www.nihva.com

CLIENT - **Suroj Buildcon Pvt Ltd**
PROJECT - **Embassy**
SITE - Chakan
DWG. NO. : NIHVA/17-18/0248
SCALE: NTS | WT: | SHEET: 01 OF 01