



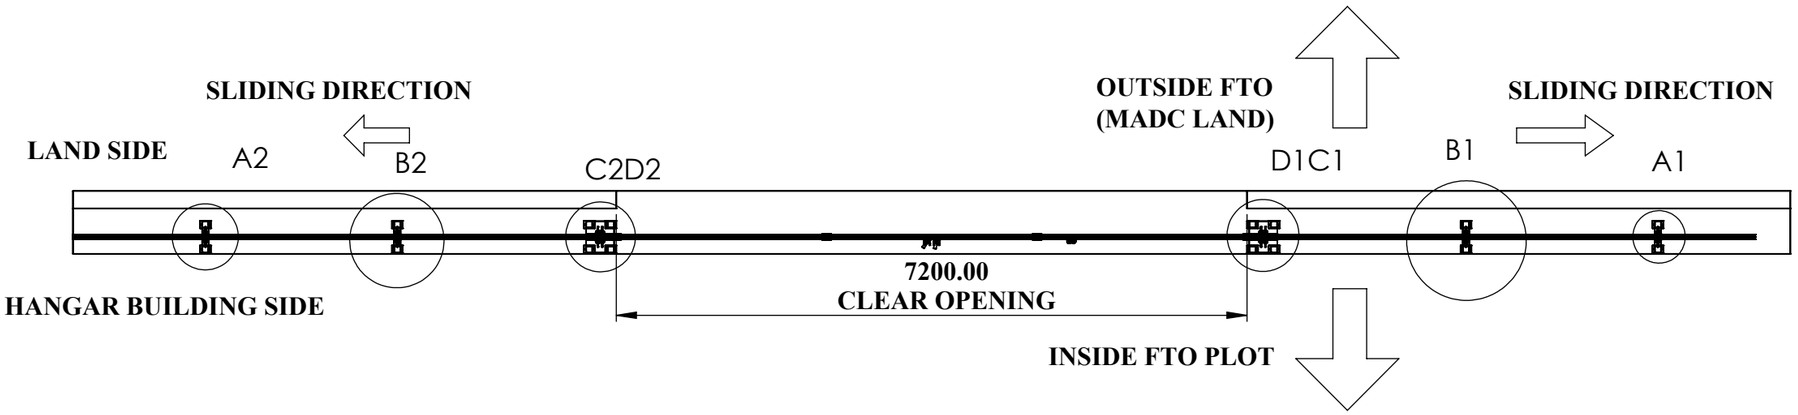


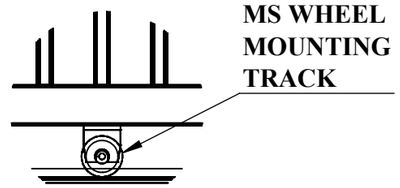

DETAIL H
SCALE 1 : 15

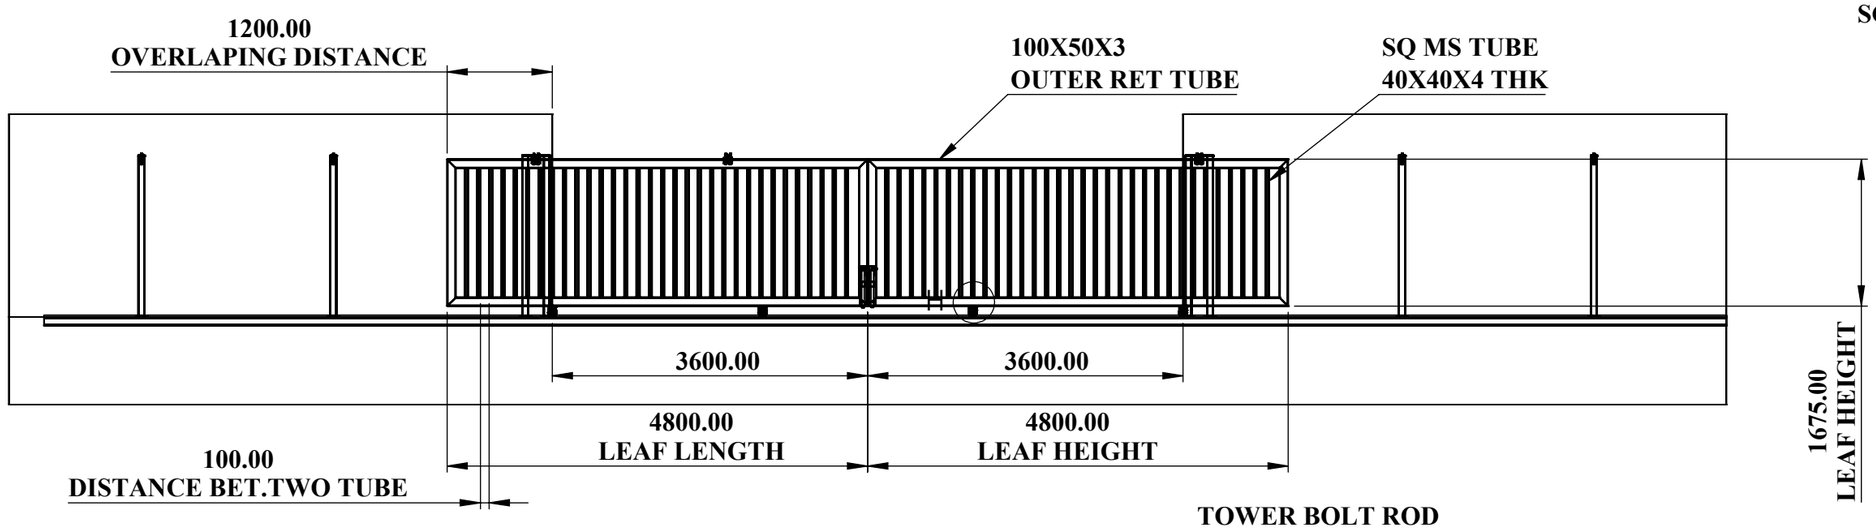


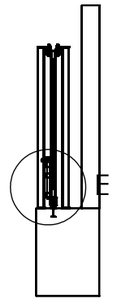

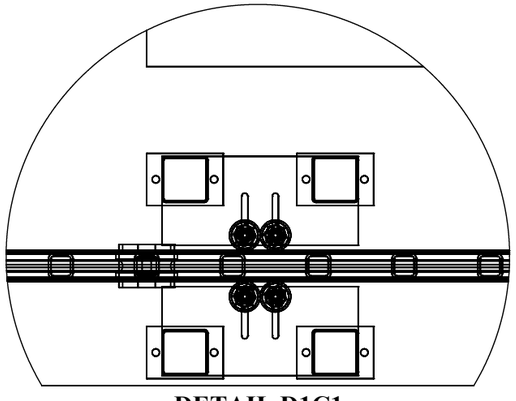


DETAIL D1C1
SCALE 1 : 10

POST1 AND NYLON BEARING ASM

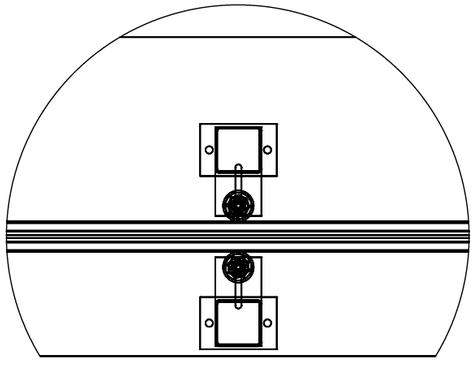

DETAIL A2
SCALE 1 : 10

POST 2 AND NYLON BEARING ASM

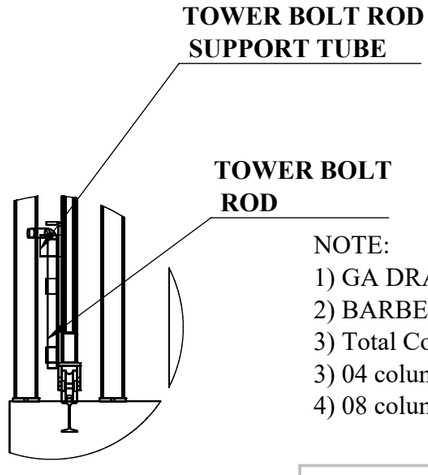


DETAIL SCALE E
1 : 20


TOWER BOLT LOCKING ARRANGEMENT

NOTE:
1) GA DRAWING TYPE NO 03
2) BARBED WIRE IS NOT MENTION IN DWG.
3) Total Column-8 (A1,B1,C1,D1) same as Right side add 4 Post
3) 04 column posts when the gate is in the closed position.(C1,D1 &C2,D2)
4) 08 column posts when the gate is in the open position.(A1,B1,C1,D1 &A2,B2,C2,D2)


TITLE - GATE AUTOMATION				NIHVA TECHNOLOGIES PVT.LTD.PUNE
DWG NO - NTPL-290-PM-003			QTY - 1	Website - www.nihva.com
	NAME	SIGNATURE	DATE	PROJECT NO - NTPL-290-PM
DRAWN	V.B.		29-07-2025	PRODUCT - BY PARTING SLIDING GATE
CHK'D	B.S.		29-07-2025	SITE LOCATION - AMRAVATI
APPV'D	V.T.		29-07-2025	TYPE 3
if any queries contact - supportautomation@nihva.com				REVISION - 00
ALL DIMENSION ARE IN mm			A3	SCALE - SHEET 1 OF 1

ITEM NO.	PART NUMBER	DESCRIPTION	QTY.
1	CIVIL BASE	1900(L) X3350 (W)	1
2	EN 8 BAR AND ISMB 1	19200 (L)	1
3	SLIDING GATE ASM	4800 X 1675	2
4	DOUBLE POST ASM	320X350X10	2
5	SINGLE POST ASM	320X75X10	4
6	NYLON ROLLER WITH BOLT ASM	75 (L) X50 (DIA)	16
7	HEX NUT	M14	16
8	M14 ANCHOR ASSY	M14 X150	64
9	TOWER BOLT ASM	300 MM (L) 15 (DIA)	2
10	NYLON STOPPER	215X110X110	2

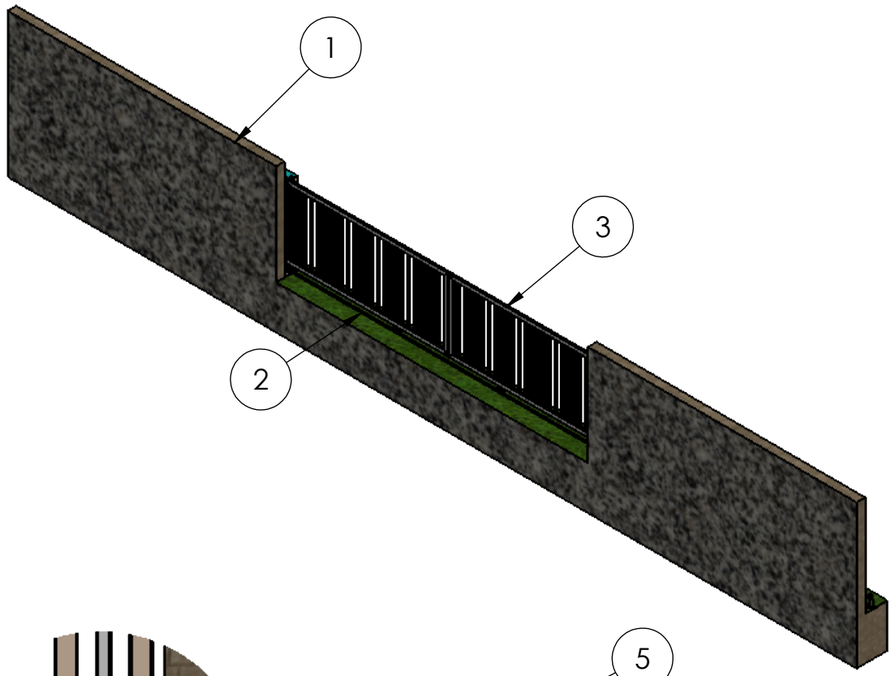


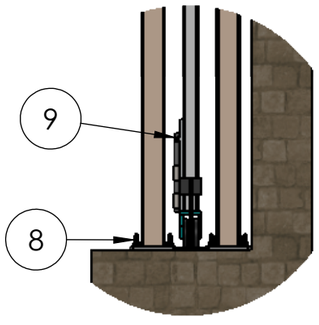


DETAIL D
SCALE 1 : 20

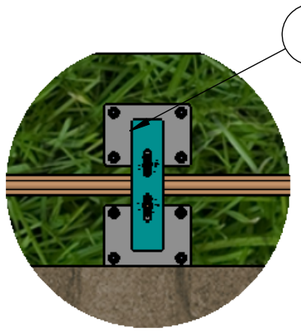

DETAIL A
SCALE 1 : 15

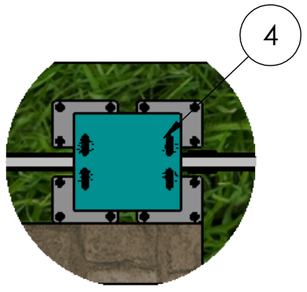


DETAIL B
SCALE 1 : 20

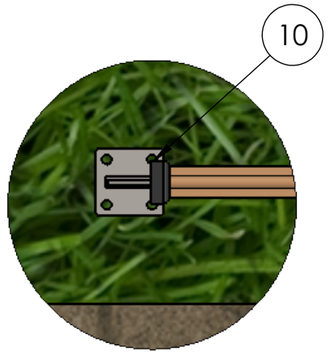


DETAIL C
SCALE 1 : 10



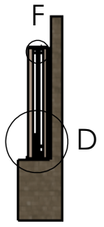




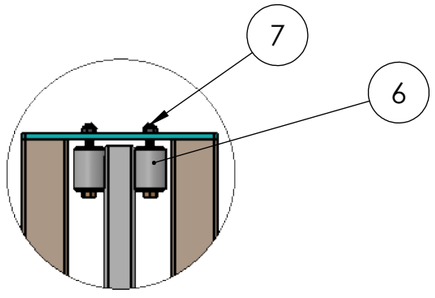


DETAIL F
SCALE 1 : 10

TITLE - GATE AUTOMATION				NIHVA TECHNOLOGIES PVT.LTD.PUNE Website - www.nihva.com
DWG NO - NTPL-290-PM-003			QTY - 1	
	NAME	SIGNATURE	DATE	PROJECT NO - NTPL-290-PM
DRAWN	V.B.		13-08-2025	PRODUCT - BYPARTING SLIDING GATE
CHK'D	B.S.		13-08-2025	SITE LOCATION -AMRAVATI
APPV'D	V.T.		13-08-2025	TYPE 3
if any queries contact - supportautomation@nihva.com				REVISION -00
ALL DIMENSION ARE IN mm			A3	SCALE -

ITEM NO.	PART NUMBER	DESCRIPTION	QTY.
1	BY PARTING SLIDING GATE	4800(L) X1675 (H)	1
2	WHEEL AND PLATE ASM	4 INCH WHEEL	2

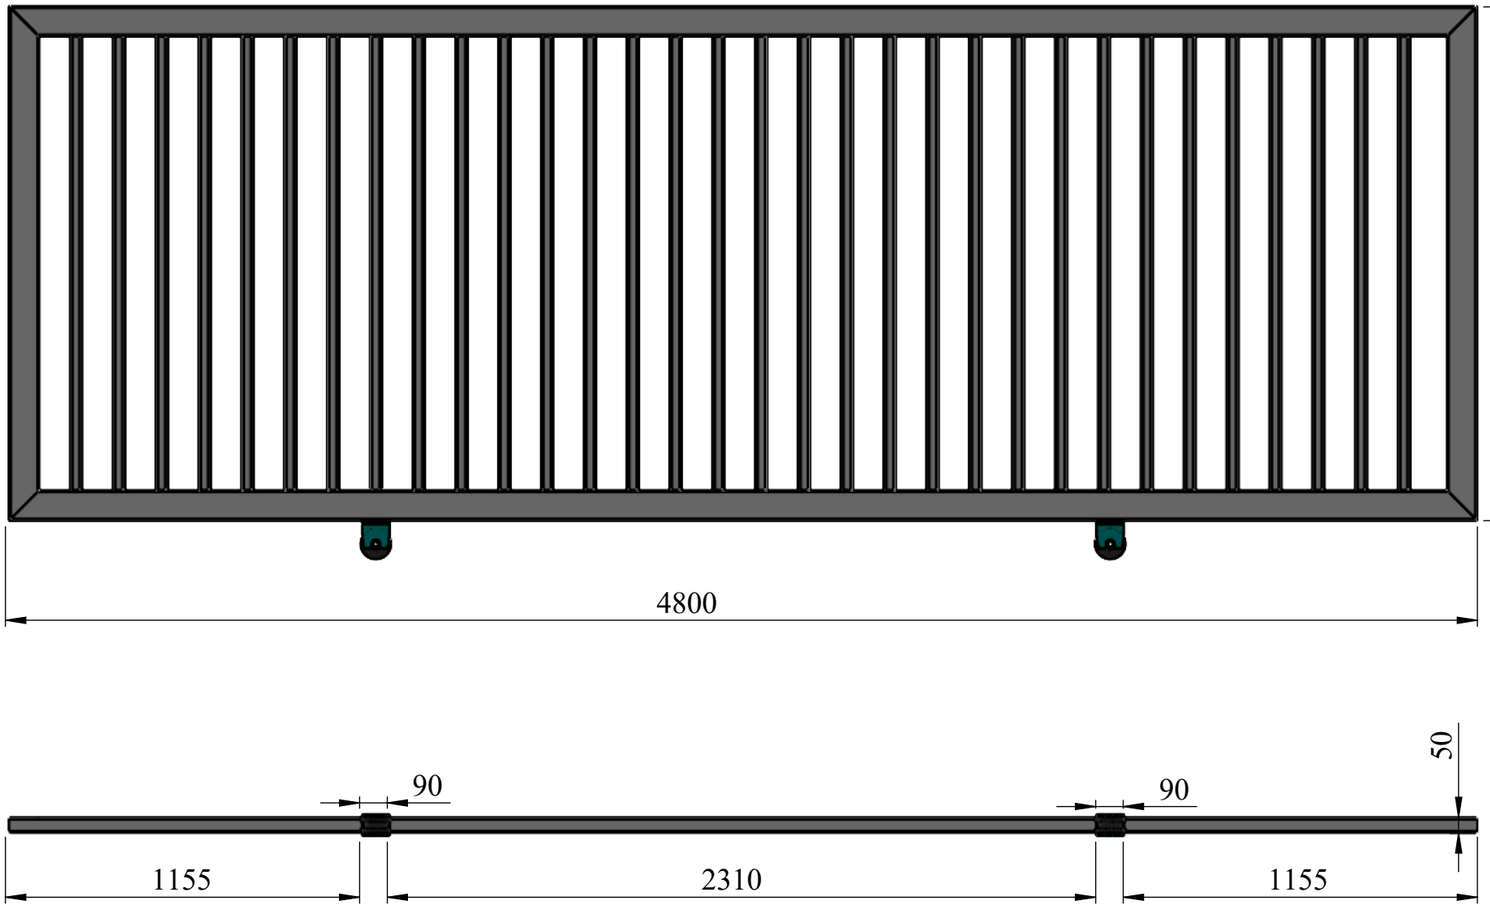


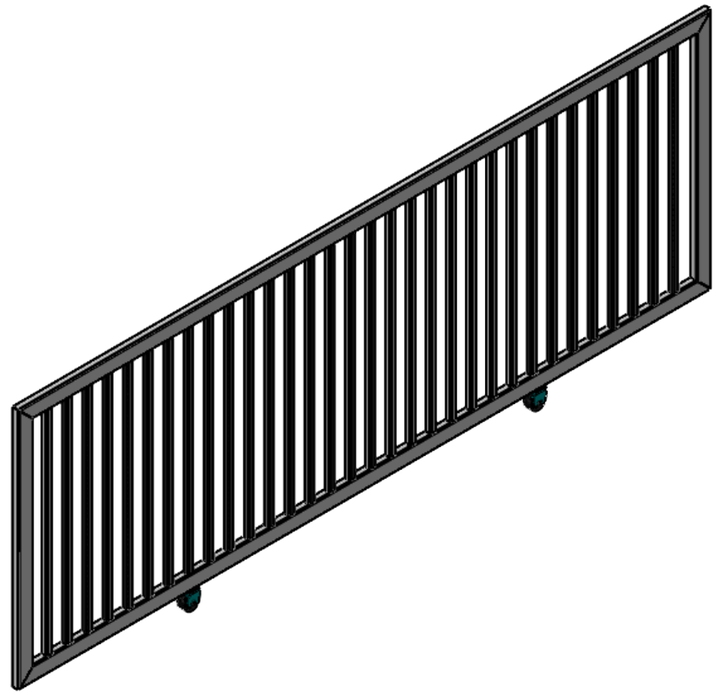


SLIDING LEAF- 2 NOS


TITLE - GATE AUTOMATION				NIHVA TECHNOLOGIES PVT.LTD.PUNE Website - www.nihva.com
DWG NO - NTPL-290-PM-003-01				
	NAME	SIGNATURE	DATE	PROJECT NO - NTPL-290-PM
DRAWN	V.B.		13-08-2025	PRODUCT - BY PARTING SLIDING GATE
CHK'D	B.S.		13-08-2025	SITE LOCATION - AMRAVATI
APPV'D	V.T.		13-08-2025	TYPE-3
if any queries contact - design@nihva.com				REVISION -00 / QTY - 1
ALL DIMENSION ARE IN mm		A3		SCALE - / SHEET 1 OF 18

ITEM NO.	PART NUMBER	DESCRIPTION	QTY.
	OUTER FRAME	100X 50X 3 THK	8
	INNER SQ TUBE	40X 40 X 4 THK	64

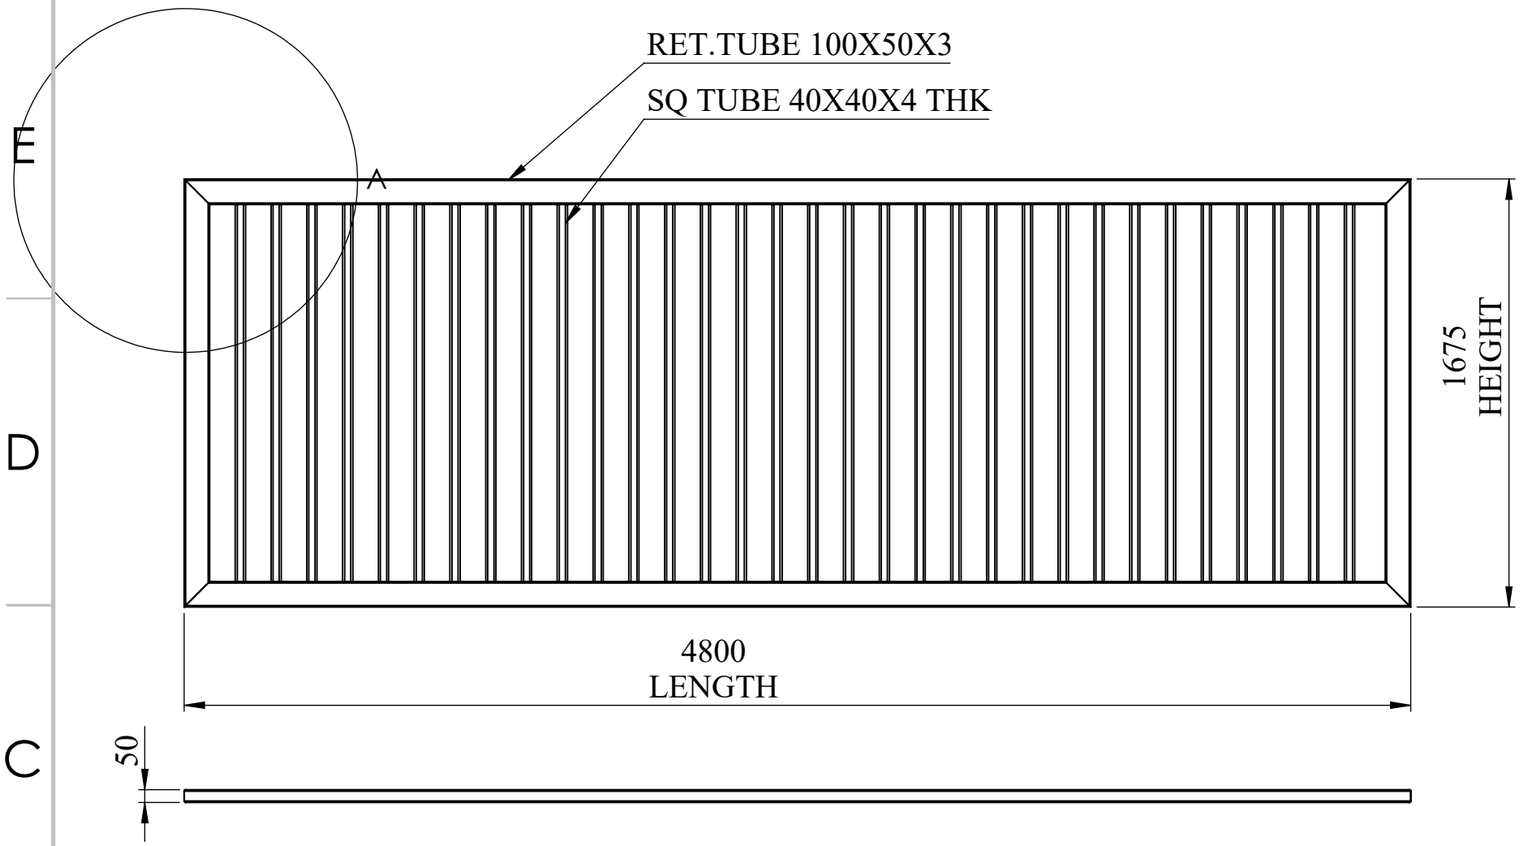

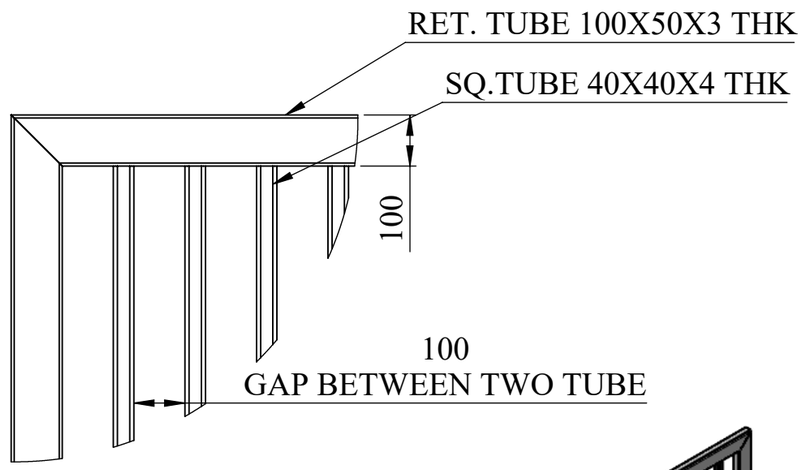


DETAIL A
SCALE 1 : 12

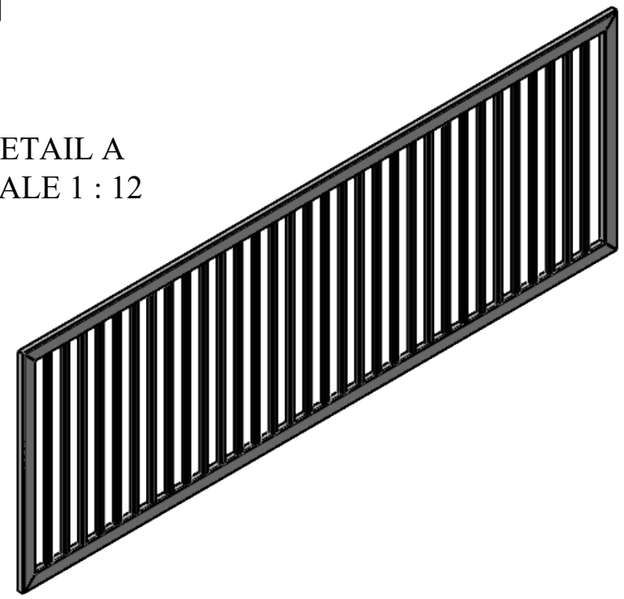


SUPPORT TUBE
QTY- 64 NOS FOR TWO LEAF

TITLE - GATE AUTOMATION				NIHVA TECHNOLOGIES PVT.LTD.PUNE
DWG NO - NTPL-290-PM-003-01-01				Website - www.nihva.com
	NAME	SIGNATURE	DATE	PROJECT NO - NTPL-290-PM
DRAWN	V.B.		13-08-2025	PRODUCT - BY PARTING SLIDING GATE
CHK'D	B.S.		13-08-2025	SITE LOCATION - AMRAVATI
APPV'D	V.T.		13-08-2025	TYPE-3
if any queries contact - design@nihva.com				REVISION -00 / QTY - 1
ALL DIMENSION ARE IN mm		A3		SCALE - / SHEET 2 OF 18

ITEM NO.	PART NUMBER	DESCRIPTION	QTY.
1	BOTTOM PLATE	215X150X10	16
2	SINGLE POST PLATE	320X75X10	4
3	VERTICAL TUBE	75X75X3	16

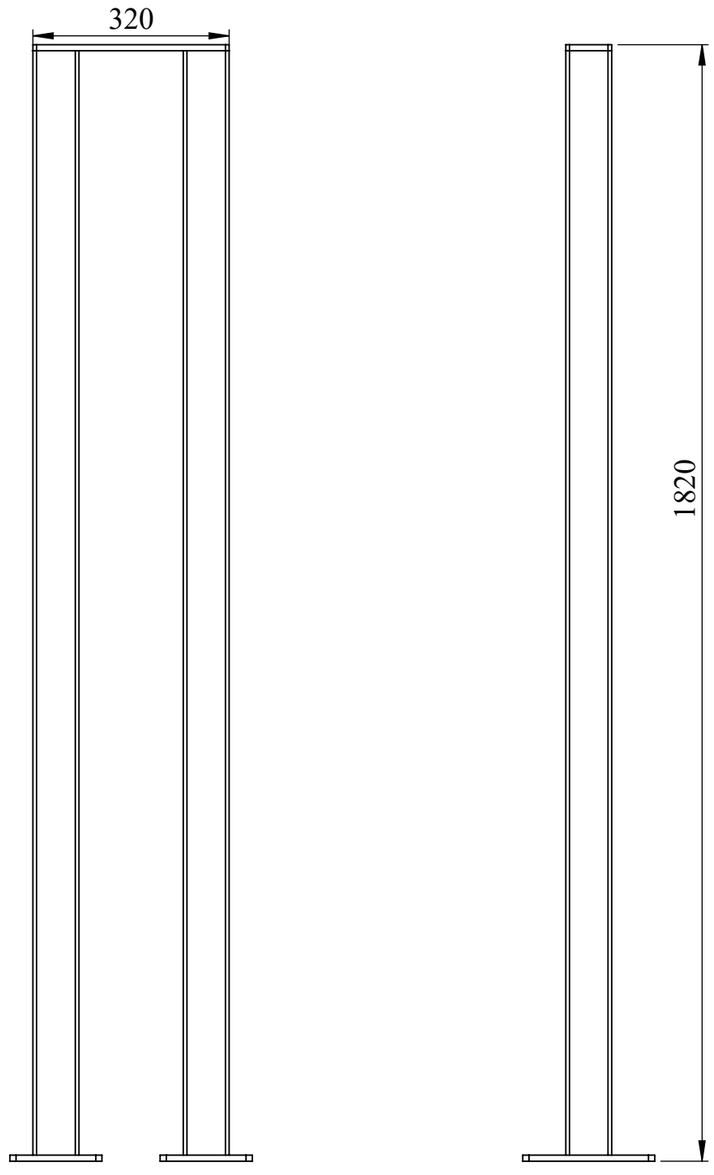


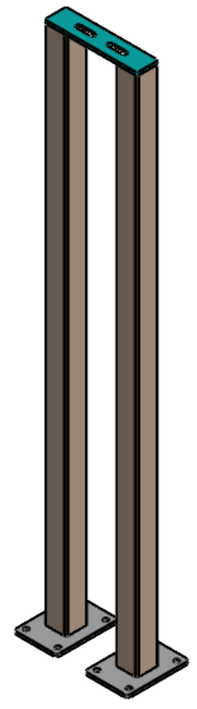


SINGLE POST ASM
QTY- 4 NOS

TITLE -GATE AUTOMATION				NIHVA TECHNOLOGIES PVT.LTD.PUNE Website - www.nihva.com
DWG NO - NTPL-290-PM-003-02				
	NAME	SIGNATURE	DATE	PROJECT NO - NTPL-290-PM
DRAWN	V.B.		13-08-2025	PRODUCT - BY PARTING SLIDING GATE
CHK'D	B.S.		13-08-2025	SITE LOCATION - AMRAVATI
APPV'D	V.T.		13-08-2025	TYPE 3
if any queries contact - design@nihva.com				REVISION -00 / QTY - 1
ALL DIMENSION ARE IN mm		A3		SCALE - / SHEET 3 OF 18

ITEM NO.	PART NUMBER	DESCRIPTION	QTY.
1	SINGLE POST PLATE	320X75X10	4

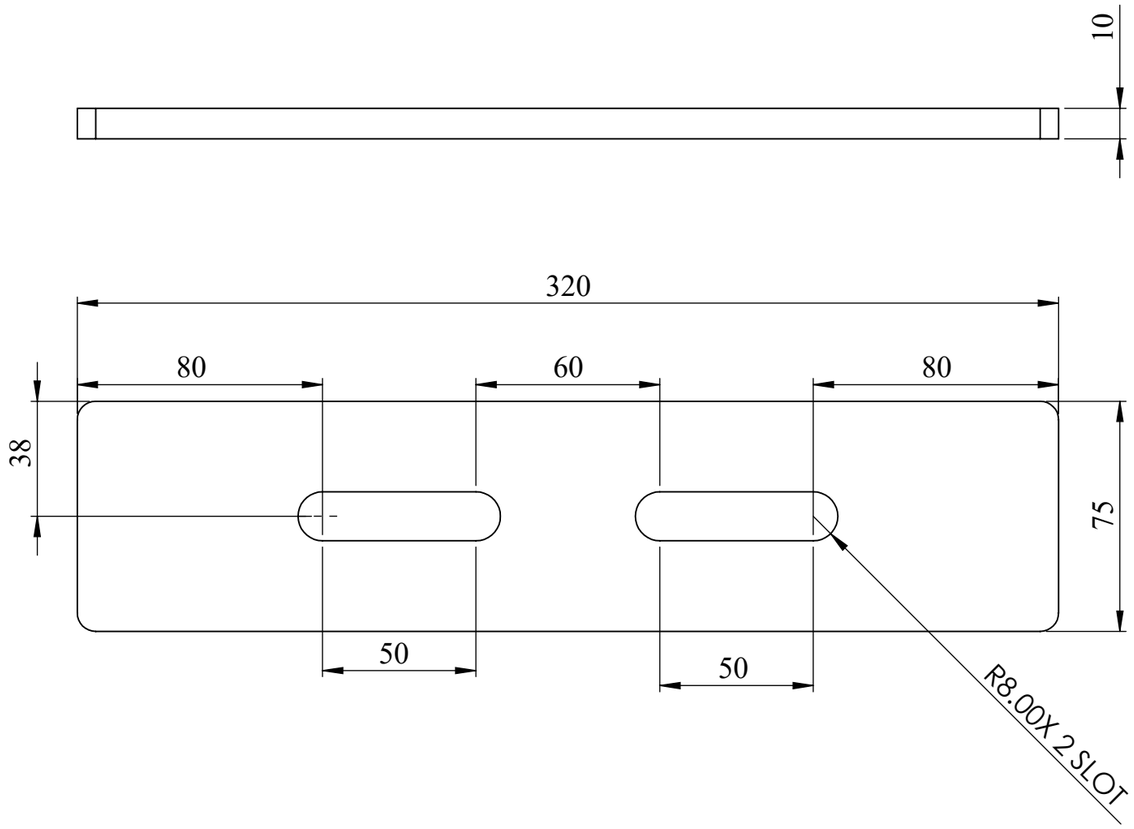


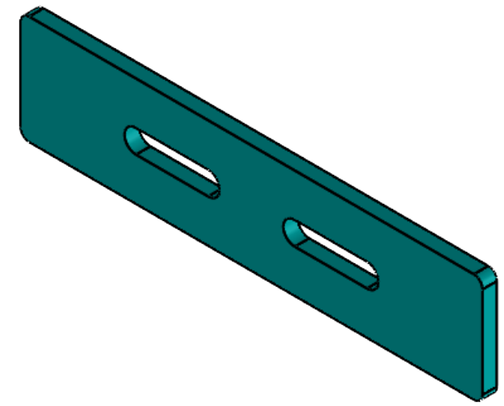


SINGLE POST PLATE
320X75X10 MM THK
QTY-4 NOS

TITLE -GATE AUTOMATION				NIHVA TECHNOLOGIES PVT.LTD.PUNE
DWG NO - NTPL-290-PM-003-02-01				Website - www.nihva.com
	NAME	SIGNATURE	DATE	PROJECT NO - NTPL-290-PM
DRAWN	V.B.		13-08-2025	PRODUCT - BY PARTING SLIDING GATE
CHK'D	B.S.		13-08-2025	SITE LOCATION - AMRAVATI
APPV'D	V.T.		13-08-2025	TYPE 3
if any queries contact - design@nihva.com				REVISION -00 / QTY - 1
ALL DIMENSION ARE IN mm		A3		SCALE - / SHEET 4 OF 18

ITEM NO.	PART NUMBER	DESCRIPTION	QTY.
1	VERTICAL SUPPORT TUBE	75X75X3	16

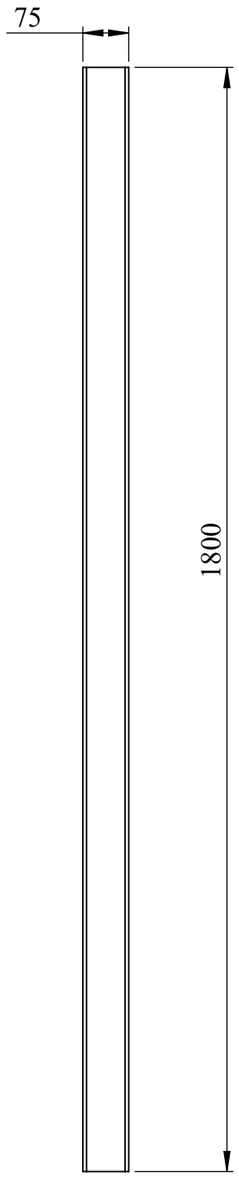


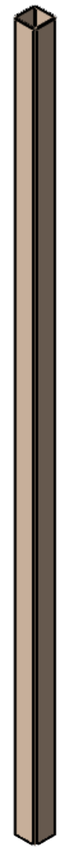



VERTICAL SUPPORT TUBE
75X75X3 MM THK
QTY-16 NOS
THIS VERTICAL SUPPORT TUBE SAME AS USE DOUBLE POST

TITLE -GATE AUTOMATION				NIHVA TECHNOLOGIES PVT.LTD.PUNE
DWG NO - NTPL-290-PM-003-02-02				Website - www.nihva.com
	NAME	SIGNATURE	DATE	PROJECT NO - NTPL-290-PM
DRAWN	V.B.		13-08-2025	PRODUCT - BY PARTING SLIDING GATE
CHK'D	B.S.		13-08-2025	SITE LOCATION - AMRAVATI
APPV'D	V.T.		13-08-2025	TYPE 3
if any queries contact - design@nihva.com				REVISION -00 / QTY - 1
ALL DIMENSION ARE IN mm		A3		SCALE - / SHEET 5 OF 18

ITEM NO.	PART NUMBER	DESCRIPTION	QTY.
1	BOTTOM PLATE	215X150X10	16

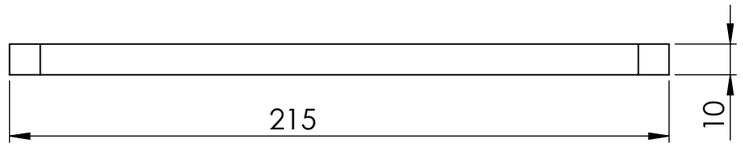

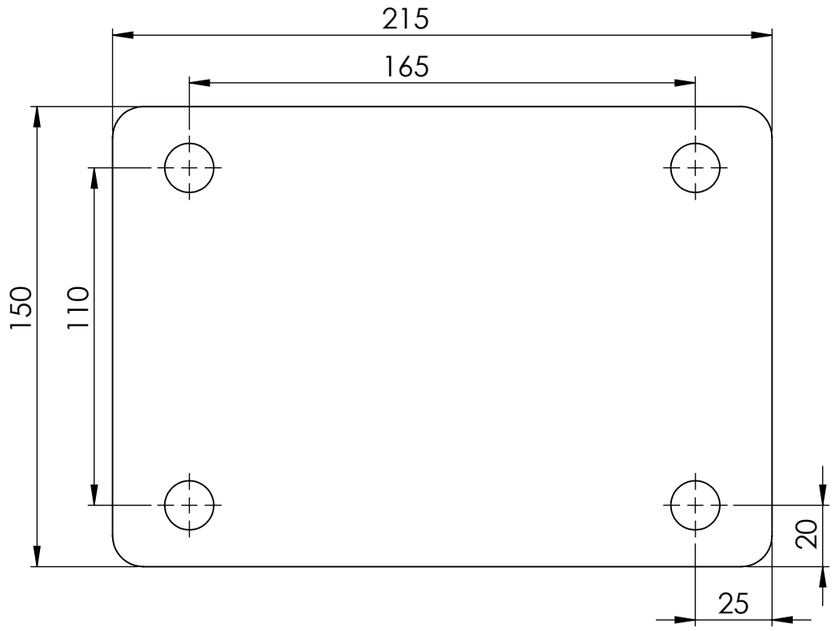


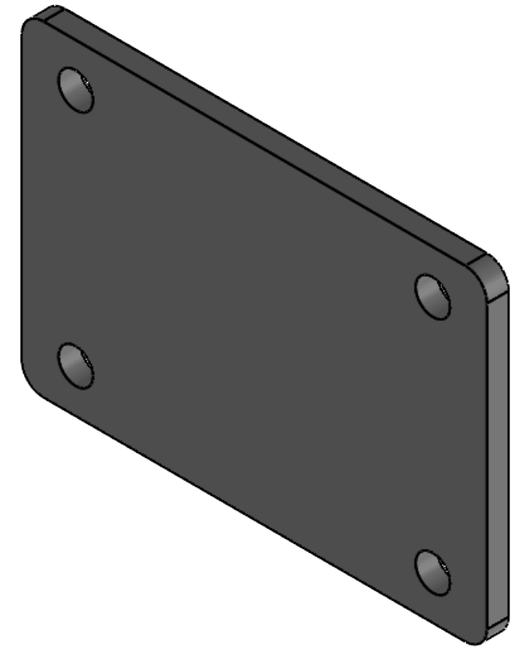


BOTTOM PLATE FOR POST
215X150X10 MM THK
QTY-16 NOS
THIS BOTTOM PLATE SAME AS USE DOUBLE POST

TITLE -GATE AUTOMATION				NIHVA TECHNOLOGIES PVT.LTD.PUNE
DWG NO - NTPL-290-PM-003-02-03				Website - www.nihva.com
	NAME	SIGNATURE	DATE	PROJECT NO - NTPL-290-PM
DRAWN	V.B.		13-08-2025	PRODUCT - BY PARTING SLIDING GATE
CHK'D	B.S.		13-08-2025	SITE LOCATION - AMRAVATI
APPV'D	V.T.		13-08-2025	TYPE 3
if any queries contact - design@nihva.com				REVISION -00 / QTY - 1
ALL DIMENSION ARE IN mm		A3		SCALE - / SHEET 6 OF 18

ITEM NO.	PART NUMBER	DESCRIPTION	QTY.
1	BOTTOM PLATE	215X150X10	16
2	DOUBLE POST PLATE	350X320X10	2
3	VERTICAL TUBE	75X75X3	16

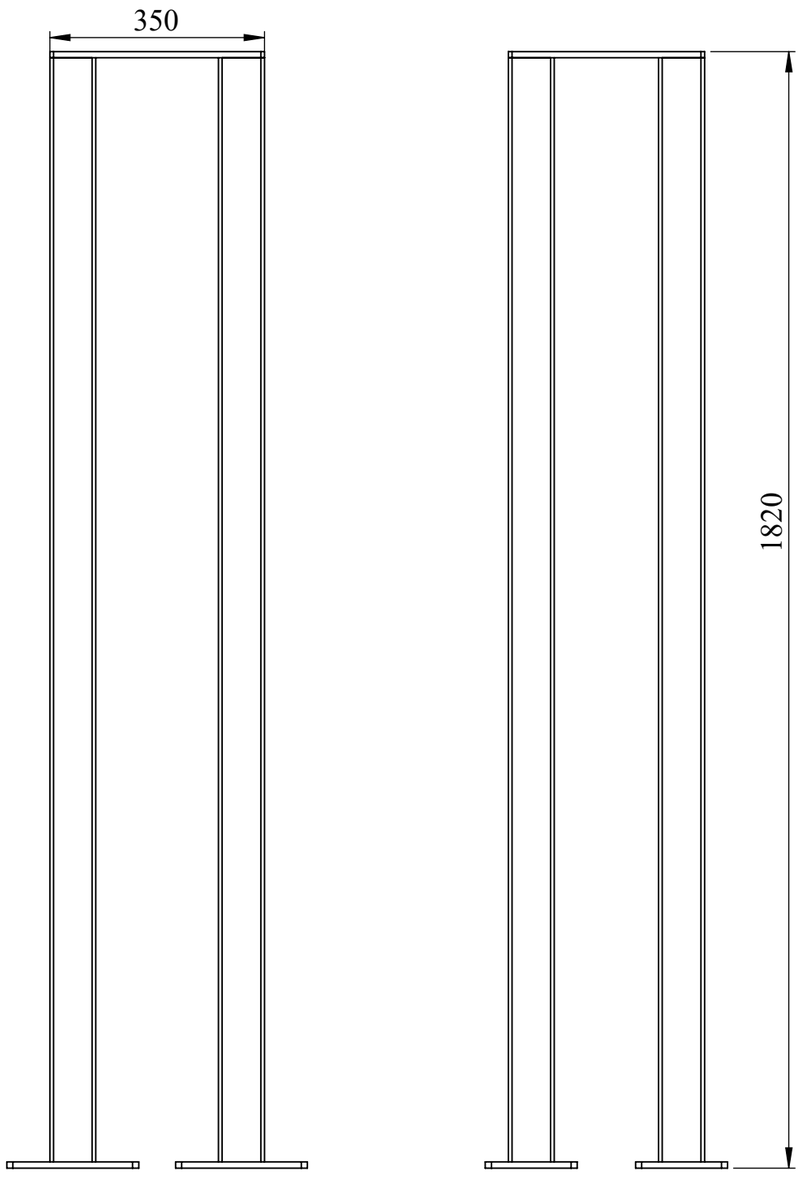

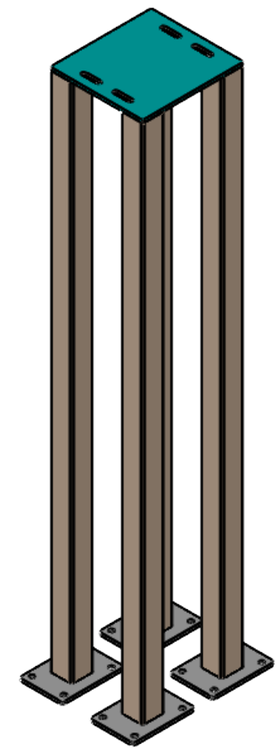



DOUBLE POST ASM
QTY- 2 NOS

TITLE -GATE AUTOMATION				NIHVA TECHNOLOGIES PVT.LTD.PUNE
DWG NO - NTPL-290-PM-003-03				Website - www.nihva.com
	NAME	SIGNATURE	DATE	PROJECT NO - NTPL-290-PM
DRAWN	V.B.		13-08-2025	PRODUCT - BY PARTING SLIDING GATE
CHK'D	B.S.		13-08-2025	SITE LOCATION - AMRAVATI
APPV'D	V.T.		13-08-2025	TYPE 3
if any queries contact - design@nihva.com				REVISION -00 / QTY - 1
ALL DIMENSION ARE IN mm		A3		SCALE - / SHEET 7 OF 18

ITEM NO.	PART NUMBER	DESCRIPTION	QTY.
1	DOUBLE POST PLATE	350X320X10	2



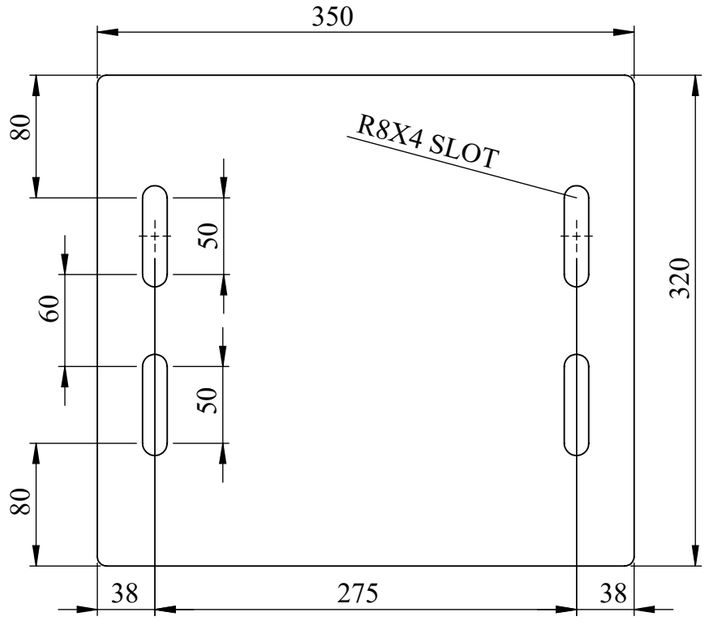


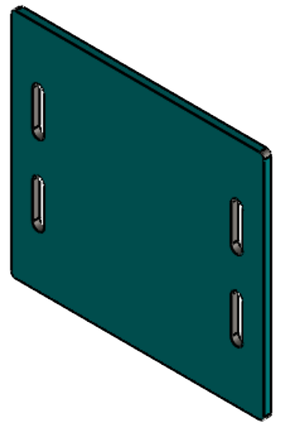



DOUBLE POST PLATE
350X320X10 MM THK
QTY-2 NOS

TITLE -GATE AUTOMATION				NIHVA TECHNOLOGIES PVT.LTD.PUNE
DWG NO - NTPL-290-PM-003-03-01				Website - www.nihva.com
	NAME	SIGNATURE	DATE	PROJECT NO - NTPL-290-PM
DRAWN	V.B.		13-08-2025	PRODUCT - BY PARTING SLIDING GATE
CHK'D	B.S.		13-08-2025	SITE LOCATION - AMRAVATI
APPV'D	V.T.		13-08-2025	TYPE 3
if any queries contact - design@nihva.com				REVISION -00 / QTY - 1
ALL DIMENSION ARE IN mm		A3		SCALE - / SHEET 8 OF 18

ITEM NO.	PART NUMBER	DESCRIPTION	QTY.
1	GUIDE PLATE	ID-14 (H)-79 (W)-10	8
2	SUPPORT PLATE	90x74x10	4
3	WHEEL	100x50	4

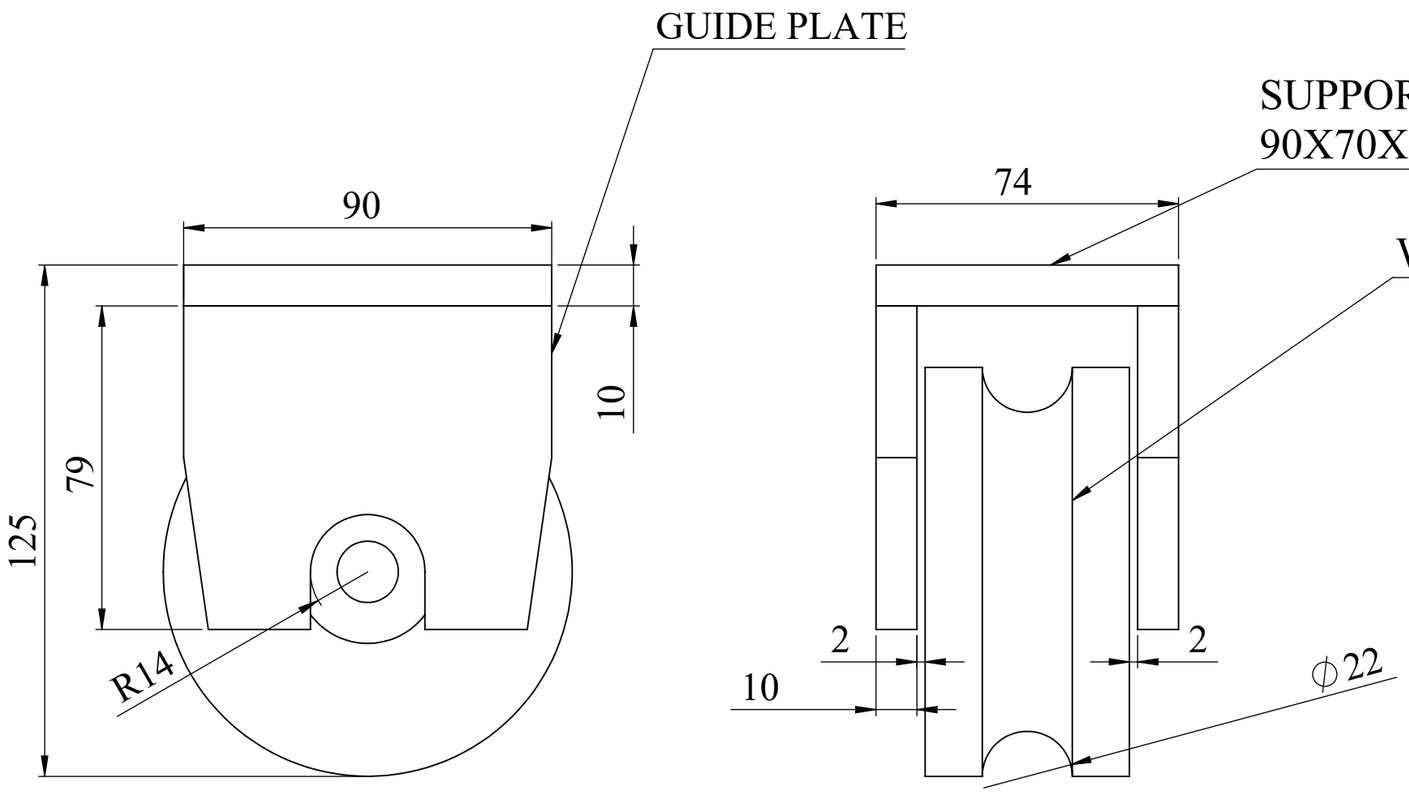

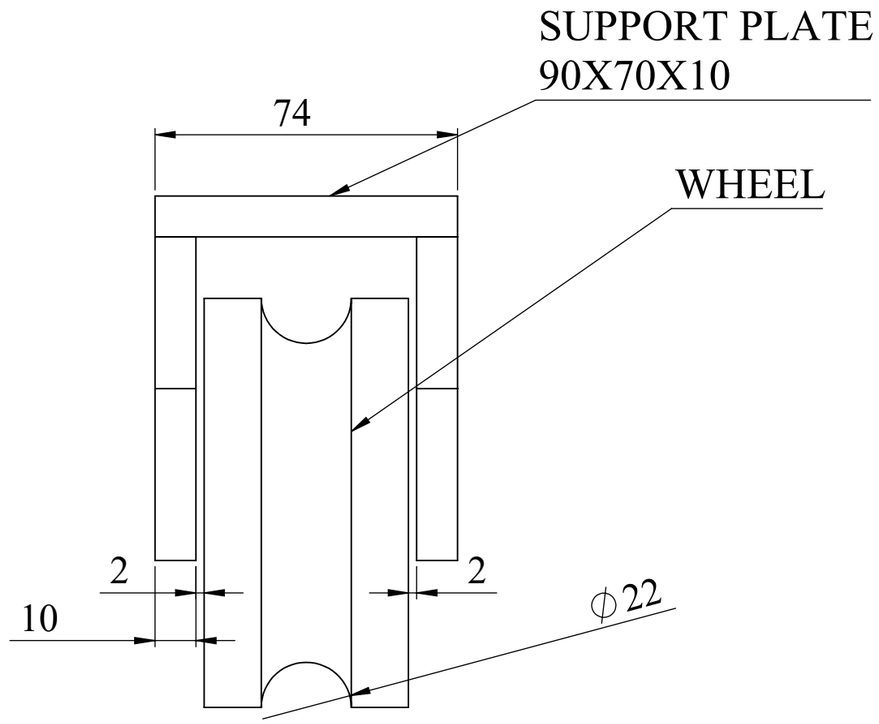


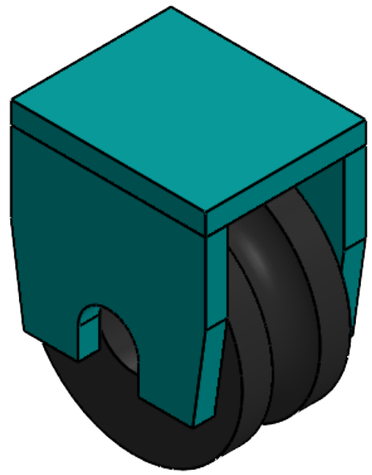


QTY- 4 NOS

TITLE - GATE AUTOMATION				NIHVA TECHNOLOGIES PVT.LTD.PUNE	
DWG NO - NTPL-290-PM-003-01-02				Website - www.nihva.com	
	NAME	SIGNATURE	DATE	PROJECT NO -NTPL-290-PM	
DRAWN	V.B.		13-08-25	PRODUCT - BY PARTING SLIDING GATE	
CHK'D	B.S.		13-08-25	SITE LOCATION - AMRAVATI	
APPV'D	V.T.		13-08-25	TYPE 3	
if any queries contact - design@nihva.com				REVISION -00	QTY - 1
ALL DIMENSION ARE IN mm		A3		SCALE -	SHEET 9 OF 18

ITEM NO.	PART NUMBER	DESCRIPTION	QTY.
1	SUPPORT PLATE	90x74x10	4

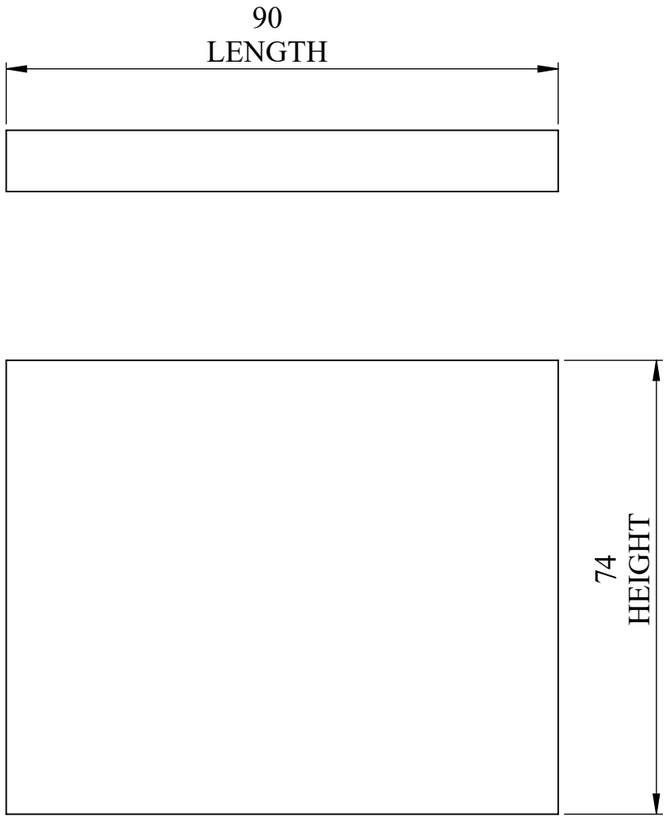


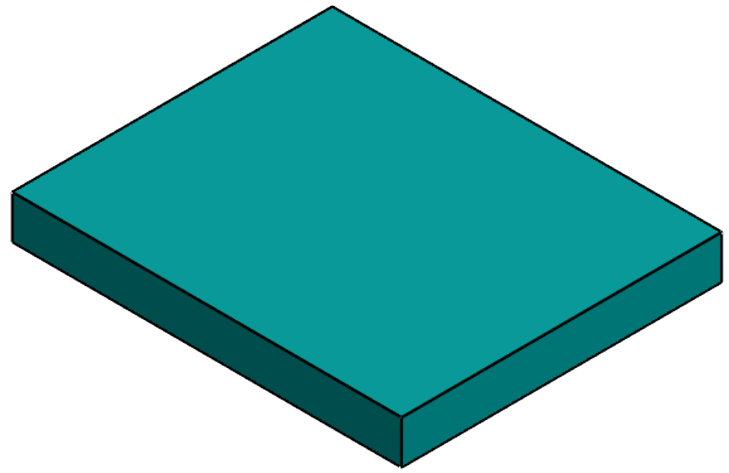



SUPPORT PLATE
QTY- 4 NOS

TITLE - GATE AUTOMATION				NIHVA TECHNOLOGIES PVT.LTD.PUNE Website - www.nihva.com
DWG NO - NTPL-290-PM-003-01-02-01				
	NAME	SIGNATURE	DATE	PROJECT NO - NTPL-290-PM
DRAWN	V.B.		13-08-2025	PRODUCT - BY PARTING SLIDING GATE
CHK'D	B.S.		13-08-2025	SITE LOCATION -AMRAVATI
APPV'D	V.T.		13-08-2025	TYPE 3
if any queries contact - design@nihva.com				REVISION -00 / QTY - 1
ALL DIMENSION ARE IN mm		A3		SCALE - / SHEET 10 OF 18

ITEM NO.	PART NUMBER	DESCRIPTION	QTY.
1	GUIDE PLATE	ID-14 (H)-79 (W)-10	8

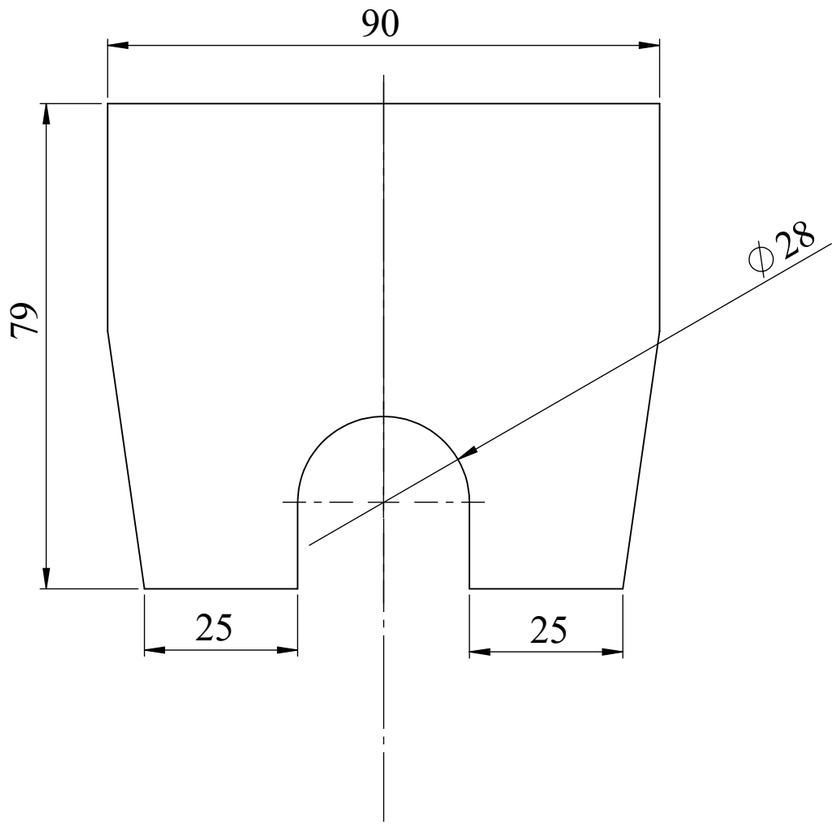

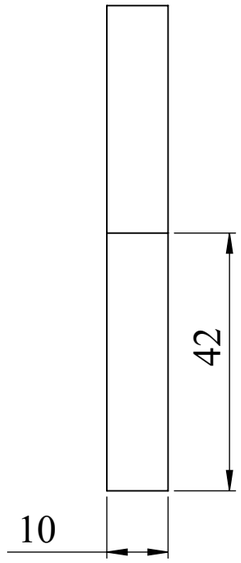


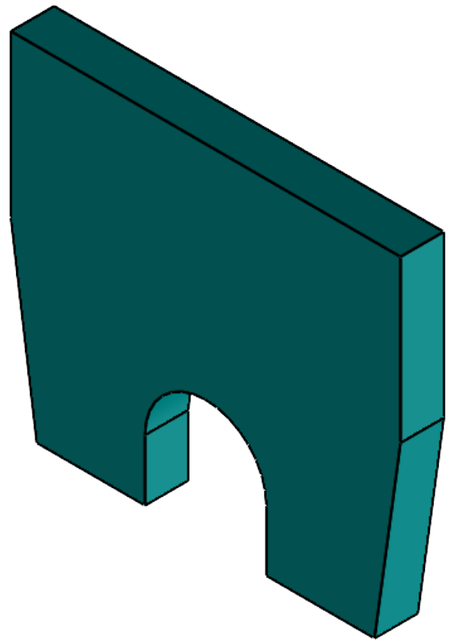


GUIDE PLATE
QTY- 8 NOS

TITLE - GATE AUTOMATION				NIHVA Technologies Pvt. Ltd.	NIHVA TECHNOLOGIES PVT.LTD.PUNE
DWG NO - NTPL-290-PM-003-01-02-02					Website - www.nihva.com
	NAME	SIGNATURE	DATE	PROJECT NO - NTPL-290-PM	
DRAWN	V.B.		13-08-2025	PRODUCT - BY PARTING SLIDING GATE	
CHK'D	B.S.		13-08-2025	SITE LOCATION -AMRAVATI	
APPV'D	V.T.		13-08-2025	TYPE 3	
if any queries contact - design@nihva.com				REVISION -00	QTY - 1
ALL DIMENSION ARE IN mm		A3		SCALE -	SHEET 11 OF 18

ITEM NO.	PART NUMBER	DESCRIPTION	QTY.
1	WHEEL	100x50	4

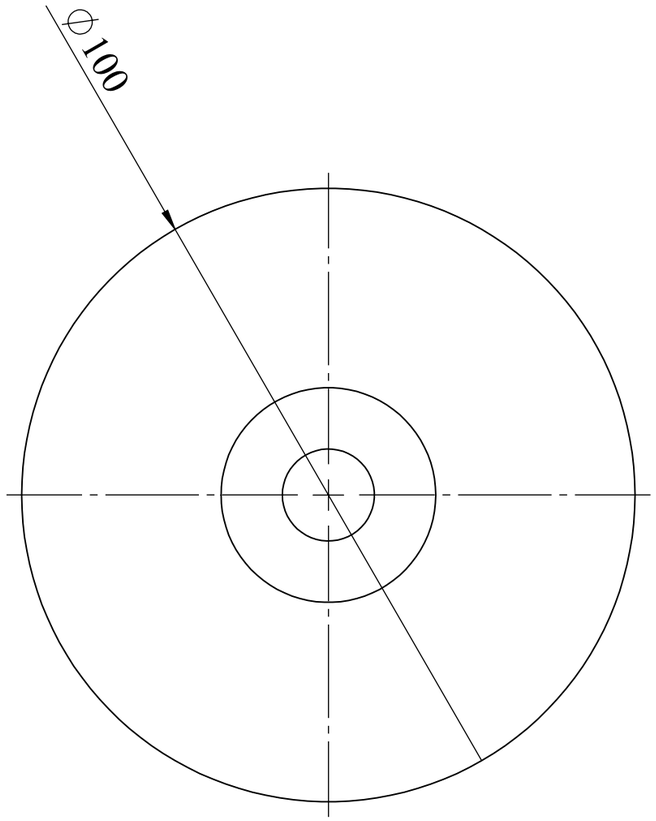

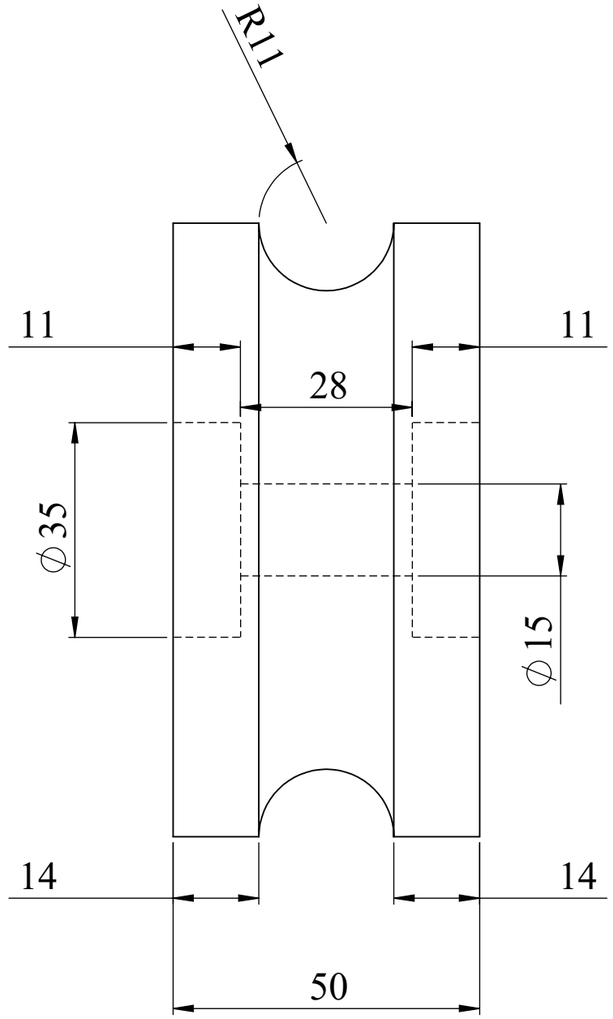






WHEEL
QTY- 4 NOS

TITLE - GATE AUTOMATION				NIHVA TECHNOLOGIES PVT.LTD.PUNE
DWG NO - NTPL-290-PM-003-01-02-03				Website - www.nihva.com
	NAME	SIGNATURE	DATE	PROJECT NO - NTPL -290-PM
DRAWN	V.B.		13-08-2025	PRODUCT -BY PARTING SLIDING GATE
CHK'D	B.S.		13-08-2025	SITE LOCATION -AMRAVATI
APPV'D	V.T.		13-08-2025	TYPE 3
if any queries contact - design@nihva.com				REVISION -00 / QTY - 1
ALL DIMENSION ARE IN mm		A3		SCALE - / SHEET 12 OF 18

ITEM NO.	PART NUMBER	DESCRIPTION	QTY.
1	EN8 BAR	OD- 20 MM	1
	ISMB BEAM	SIZE- 100 X 50 19200 MM (L)	1

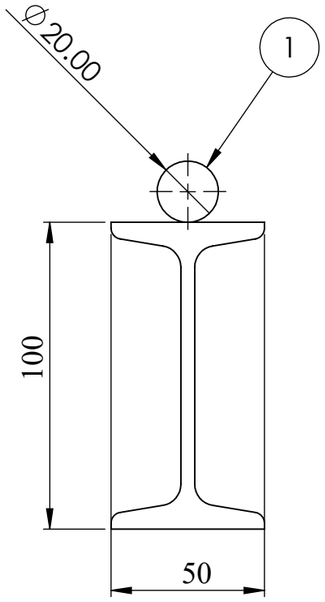

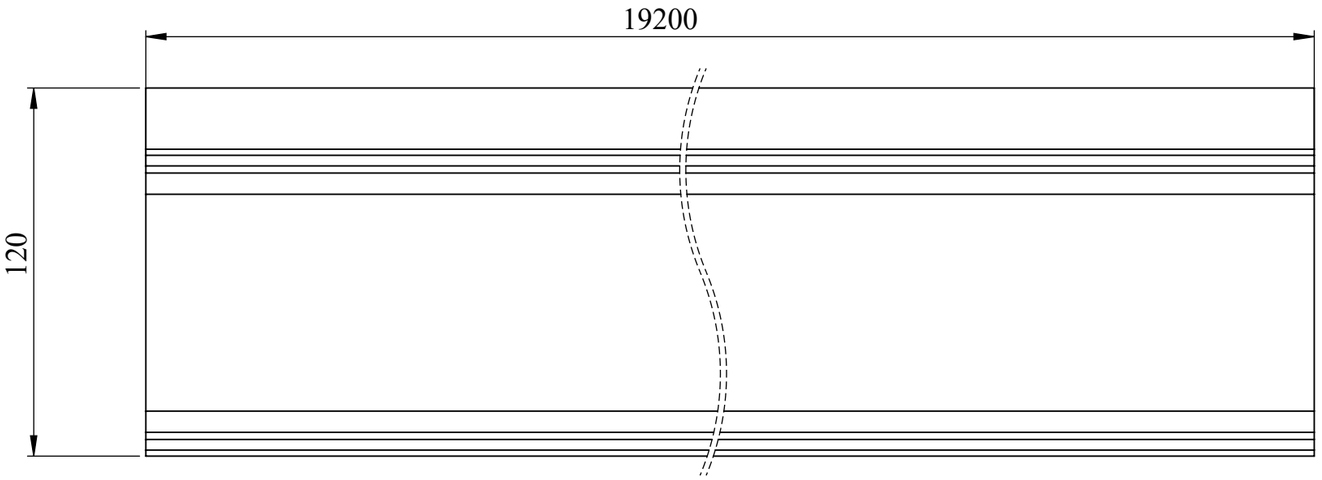


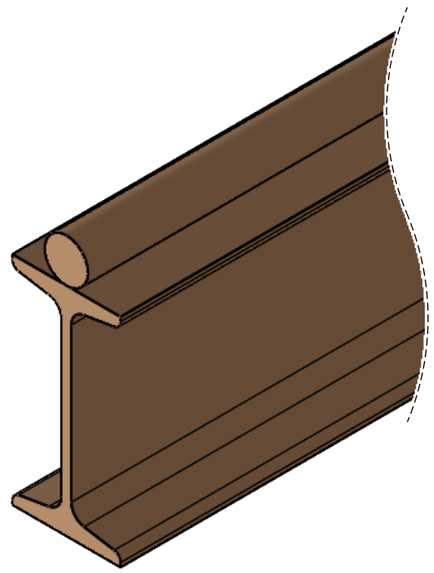


GATE TRACK
QTY-1NOS

TITLE - GATE AUTOMATION				NIHVA TECHNOLOGIES PVT.LTD.PUNE
DWG NO - NTPL-290-PM-003-04				Website - www.nihva.com
	NAME	SIGNATURE	DATE	PROJECT NO - NTPL-290-PM
DRAWN	V.B.		13-08-2025	PRODUCT - BY PARTING SLIDING GATE
CHK'D	B.S.		13-08-2025	SITE LOCATION - AMRAVATI
APPV'D	V.T.		13-08-2025	TYPE-3
if any queries contact - design@nihva.com				REVISION -00 / QTY - 1
ALL DIMENSION ARE IN mm		A3		SCALE - / SHEET 13 OF 18

ITEM NO.	PART NUMBER	DESCRIPTION	QTY.
1	M14 ANCHOR	M14X150	65

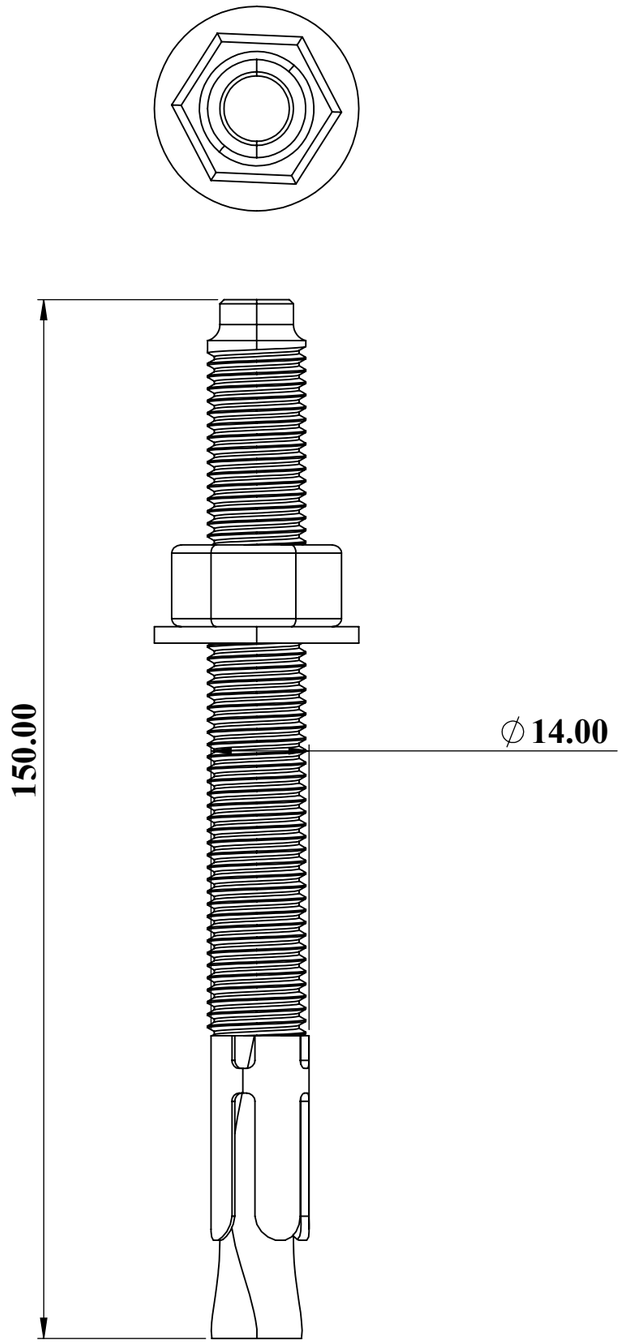


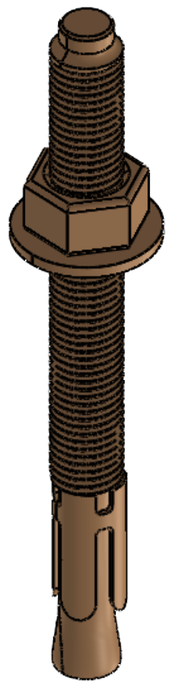



NOTE -
M14 X 150 MM ANCHOR BOLT
QTY- 65 NOS

TITLE -GATE AUTOMATION				NIHVA TECHNOLOGIES PVT.LTD.PUNE Website - www.nihva.com
DWG NO - NTPL-290-PM-003-05				
	NAME	SIGNATURE	DATE	PROJECT NO - NTPL-290-PM
DRAWN	V.B.		12-08-2025	PRODUCT -BYPARTING SLIDING GATE
CHK'D	B.S.		12-08-2025	SITE LOCATION - AMRAVATI
APPV'D	V.T.		12-08-2025	TYPE 3
if any queries contact - design@nihva.com				REVISION -00 / QTY - 1
ALL DIMENSION ARE IN mm		A3		SCALE - / SHEET 14 OF 18

ITEM NO.	PART NUMBER	DESCRIPTION	QTY.
1	NYLON STOPPER		2
2	NYLON STOPPER PLATE	135X135X10	2

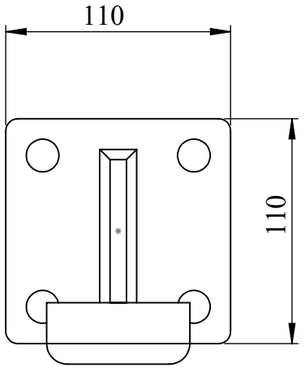

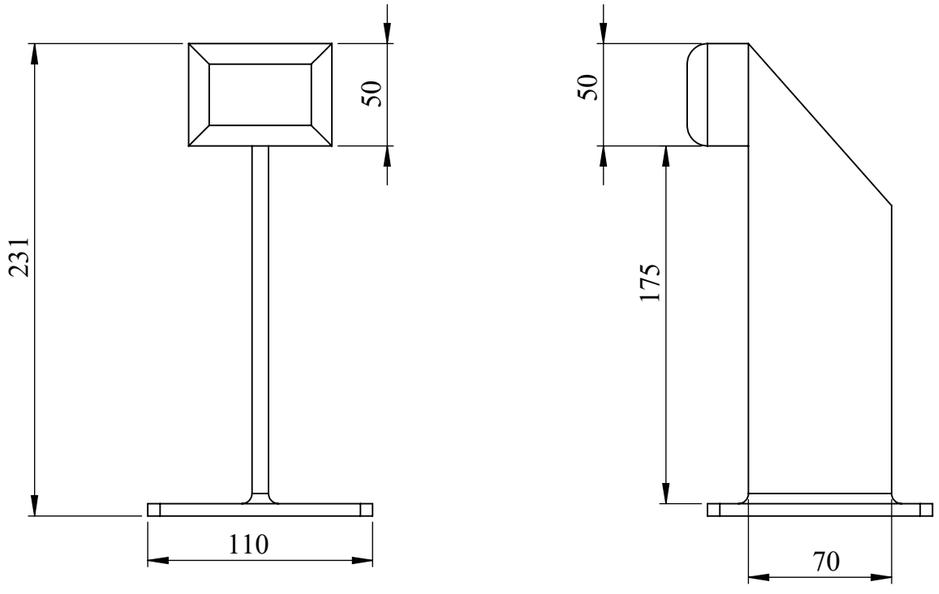


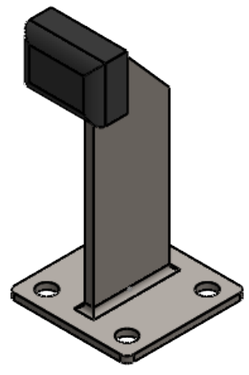



NOTE -
NYLON STOPPER
QTY- 2 NOS

TITLE -GATE AUTOMATION				NIHVA TECHNOLOGIES PVT.LTD.PUNE
DWG NO - NTPL-290-PM-003-06				Website - www.nihva.com
	NAME	SIGNATURE	DATE	PROJECT NO - NTPL-290-PM
DRAWN	V.B.		13-08-2025	PRODUCT - BY PARTING SLIDING GATE
CHK'D	B.S.		13-08-2025	SITE LOCATION - AMRAVATI
APPV'D	V.T.		13-08-2025	TYPE 3
if any queries contact - design@nihva.com				REVISION -00 / QTY - 1
ALL DIMENSION ARE IN mm		A3		SCALE - / SHEET 15 OF 18


ITEM NO.	PART NUMBER	DESCRIPTION	QTY.
2	NYLON STOPPER PLATE	135X135X10	2

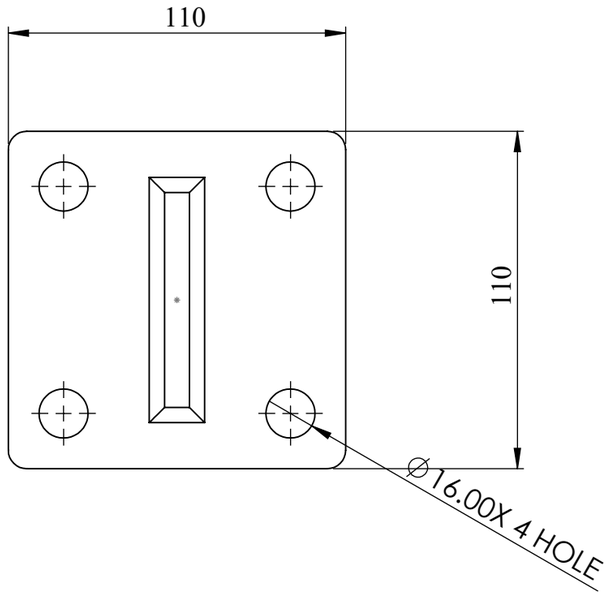

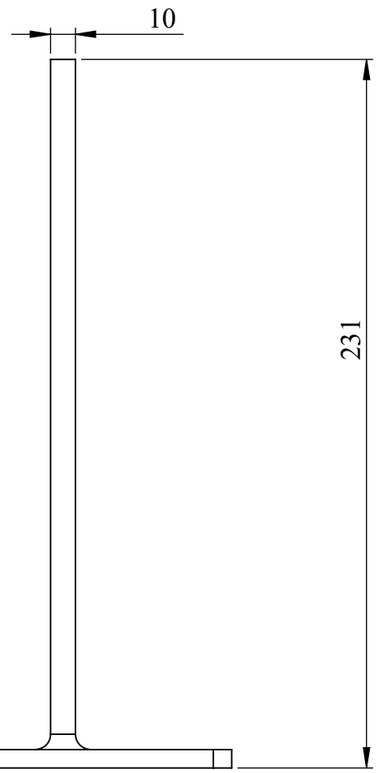

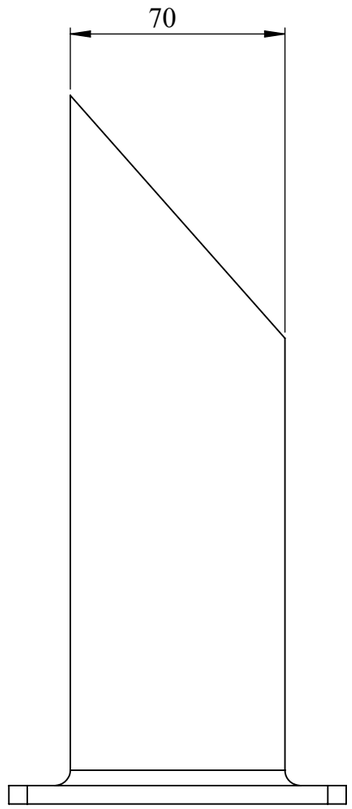



NOTE -
NYLON STOPPER
QTY- 2 NOS

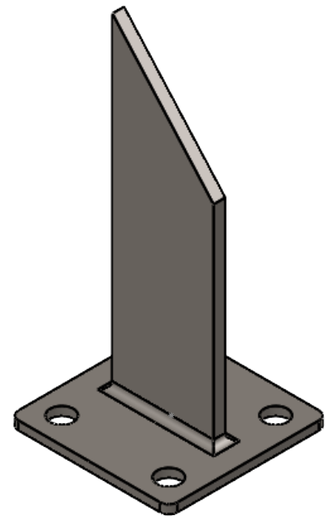


TITLE -GATE AUTOMATION				NIHVA TECHNOLOGIES PVT.LTD.PUNE Website - www.nihva.com
DWG NO - NTPL-290-PM-003-06-01				
	NAME	SIGNATURE	DATE	PROJECT NO - NTPL-290-PM
DRAWN	V.B.		12-08-2025	PRODUCT - BY PARTING SLIDING GATE
CHK'D	B.S.		12-08-2025	SITE LOCATION - AMRAVATI
APPV'D	V.T.		12-08-2025	TYPE 3
if any queries contact - design@nihva.com				REVISION -00 / QTY - 1
ALL DIMENSION ARE IN mm		A3		SCALE - / SHEET 16 OF 18

ITEM NO.	PART NUMBER	DESCRIPTION	QTY.
1	NYLON STOPPER		2

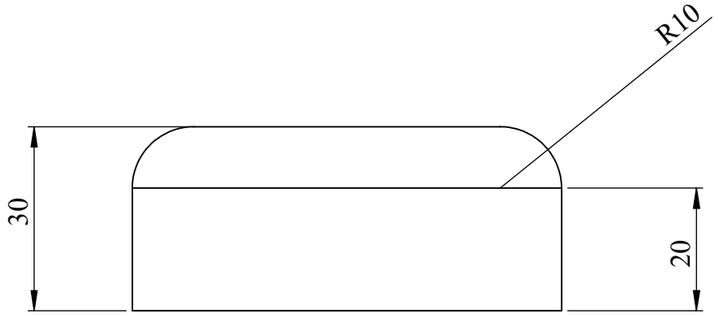

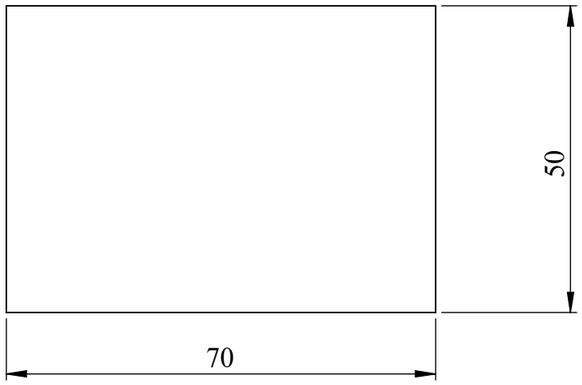


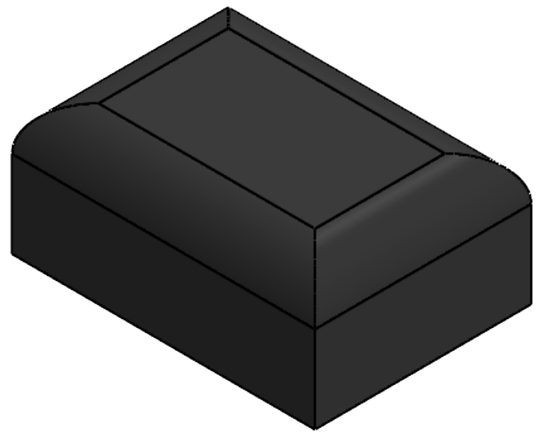


NOTE -
NYLON STOPPER
QTY- 2 NOS

TITLE -GATE AUTOMATION				NIHVA TECHNOLOGIES PVT.LTD.PUNE
DWG NO - NTPL-290-PM-003-07				Website - www.nihva.com
	NAME	SIGNATURE	DATE	PROJECT NO - NTPL-290-PM
DRAWN	V.B.		13-08-2025	PRODUCT - BY PARTING SLIDING GATE
CHK'D	B.S.		13-08-2025	SITE LOCATION - AMRAVATI
APPV'D	V.T.		13-08-2025	TYPE 3
if any queries contact - design@nihva.com				REVISION -00 / QTY - 1
ALL DIMENSION ARE IN mm		A3		SCALE - / SHEET 17 OF 18

ITEM NO.	PART NUMBER	DESCRIPTION	QTY.
1	TOWER BOLT HOLLOW PIPE	DIA- 18MM (3 MM THK)	2
2	Tower Bolt	DIA- 15MM 300(L)	2

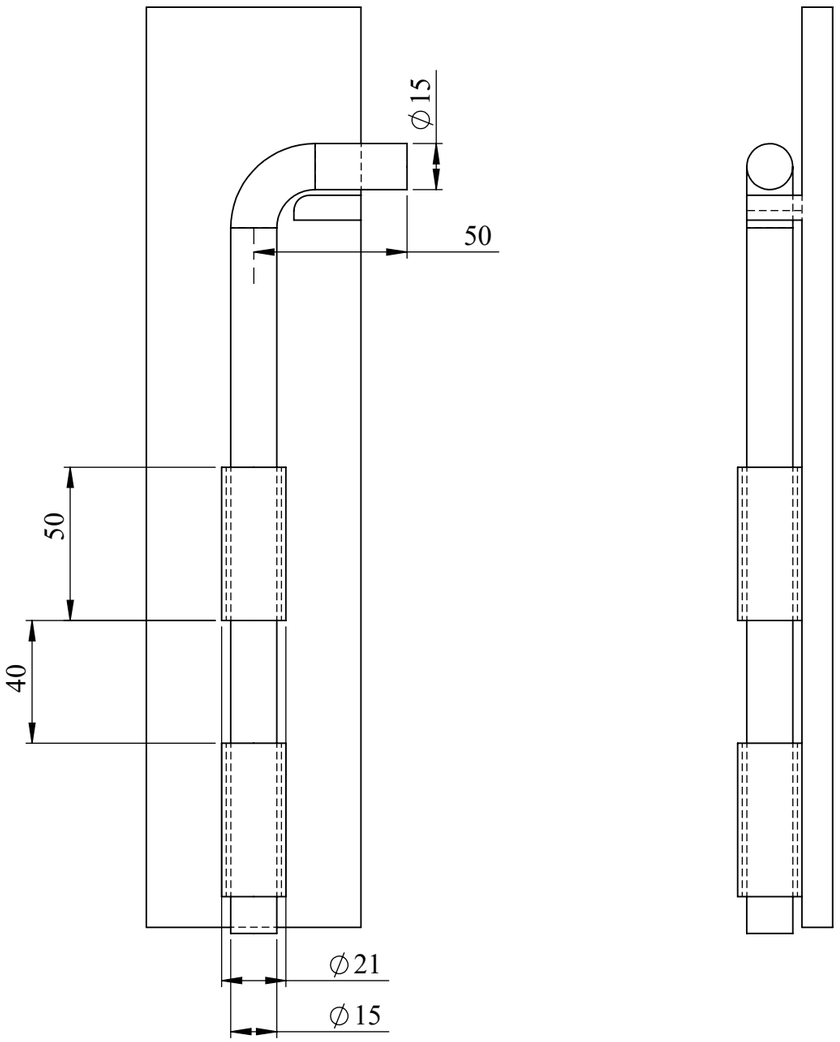

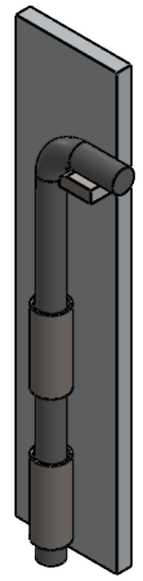

NOTE -
TOWER BOLT
QTY- 2 NOS

TITLE -GATE AUTOMATION				NIHVA TECHNOLOGIES PVT.LTD.PUNE
DWG NO - NTPL-290-PM-003-08				Website - www.nihva.com
	NAME	SIGNATURE	DATE	PROJECT NO - NTPL-290-PM
DRAWN	V.B.		13-08-2025	PRODUCT - BY PARTING SLIDING GATE
CHK'D	B.S.		13-08-2025	SITE LOCATION - AMRAVATI
APPV'D	V.T.		13-08-2025	TYPE 3
if any queries contact - design@nihva.com				REVISION -00 / QTY - 1
ALL DIMENSION ARE IN mm		A3		SCALE - / SHEET 18 OF 18