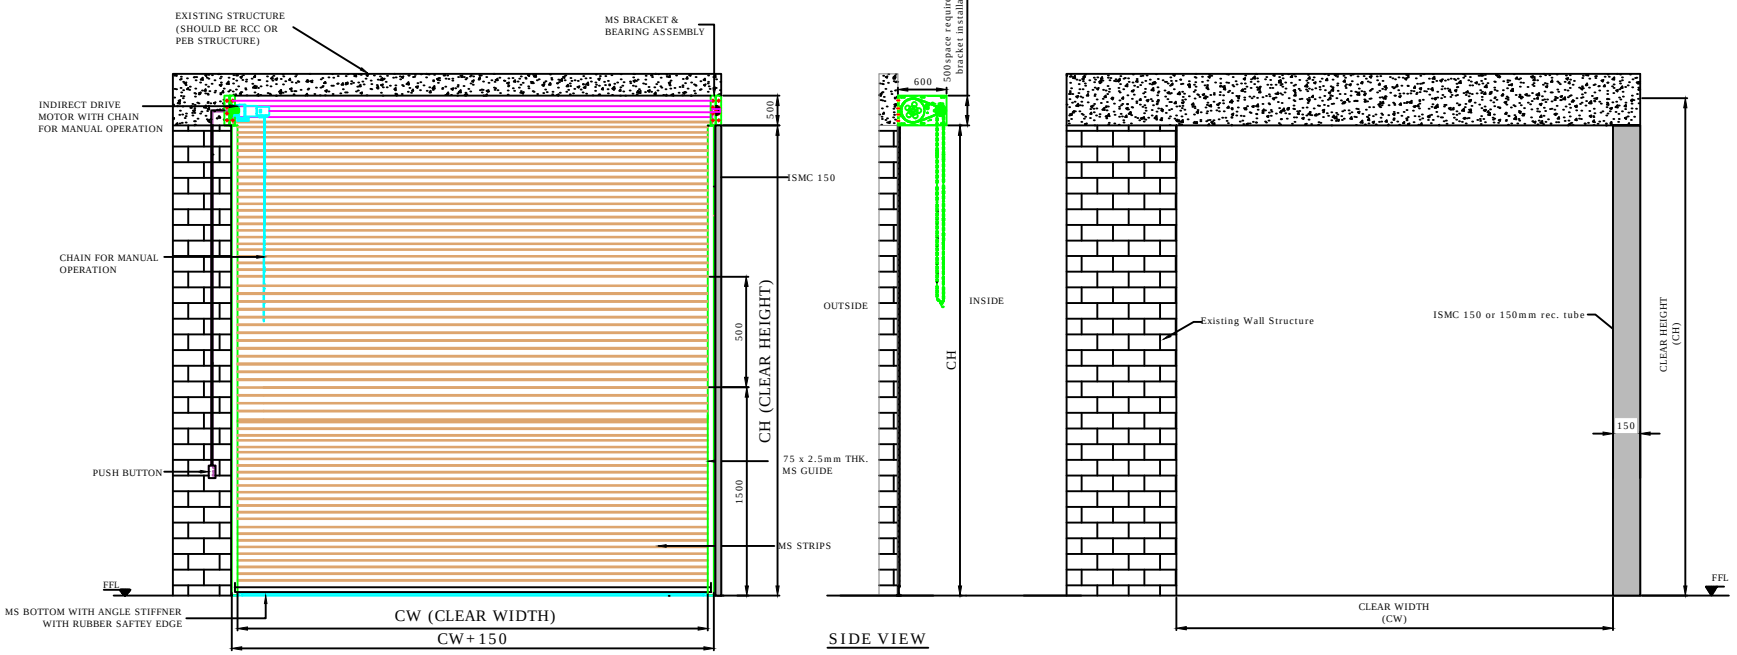


CLEAR WIDTH (CW)	CLEAR HEIGHT (CH)	QUANTITY	LOCATION
3350	3500	1	TRANSFORMER ROOM
3850	3500	1	TRANSFORMER ROOM

DIMENSION :

CLEAR WIDTH	CLEAR HEIGHT	QUANTITY
3350 mm	3500 mm	01 NOS.
3850 mm	3500 mm	01 NOS.

MATERIAL :

THICKNESS :

NOTE: REQUIRED STRUCTURE FOR DOOR SHOULD BE IN CLIENT SCOPE.

NIHVA TECHNOLOGIES PVT. LTD.
NIHVA TECHNOLOGY PVT. LTD. PUNE
Email:- info@nihva.com
Website:- www.nihva.com

TITLE:

MOTORIZED ROLLING SHUTTER WITH GRILL

CLIENT'S APPROVAL :

CLIENT -SUROJ BUILDCON PVT. LTD.

PROJECT - KSB CIVIL WORK

SITE LOCATION - SHIRWAL MIDC PHASE 2

DWG. NO. : NIHVA/16-17/0060/R02

SCALE: NTS	WT:	SHEET:1 OF 1
DRAWN BY: OMKAR		DATE: 21-10-2016
CHECK : ANIL		DATE: 21-10-2016

If any queries contact : projects@nihva.com

NOTE: ALL DIMENSION ARE IN mm

THIS DRAWING & DESIGNING IS THE PROPERTY OF NIHVA TECHNOLOGIES. NOT BE SOLD OR COPY TO ANY OTHER CONCERN.