

PRODUCED BY AN AUTODESK EDUCATIONAL PRODUCT

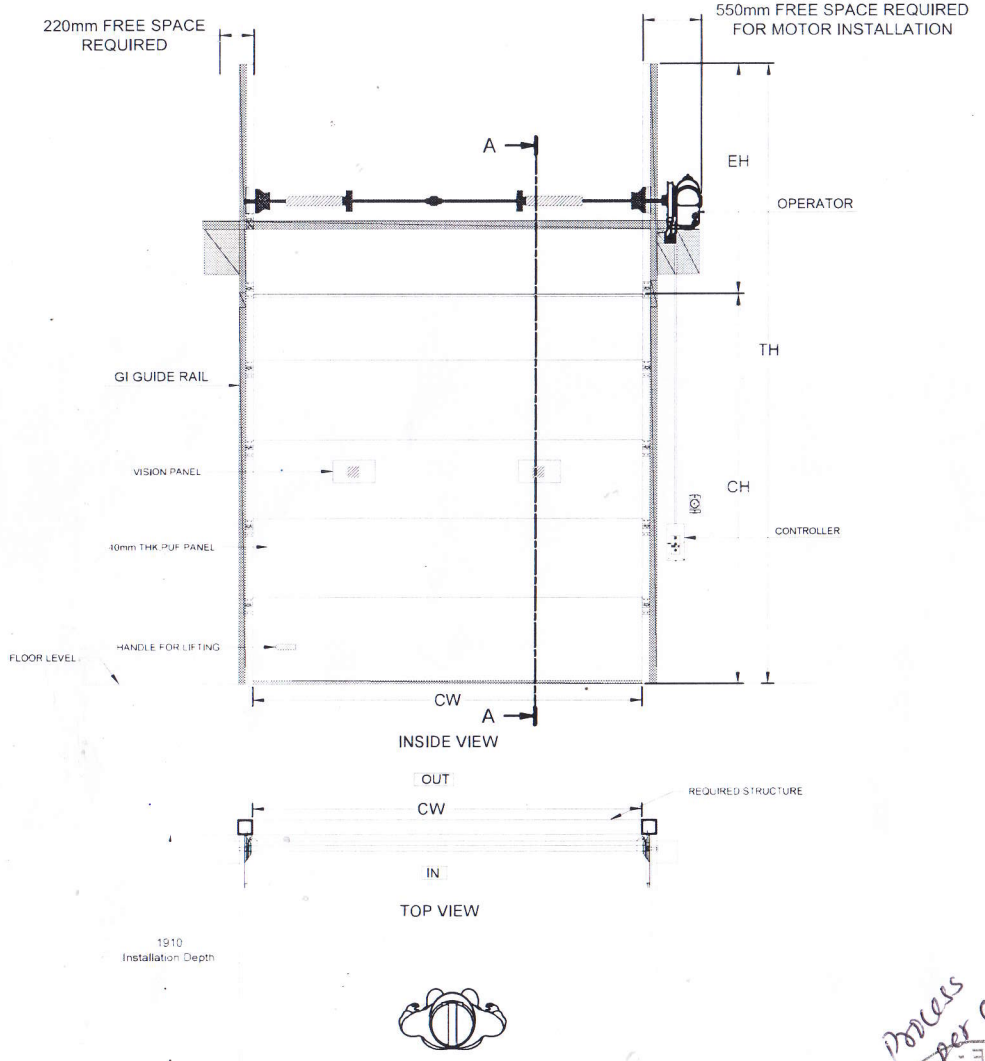

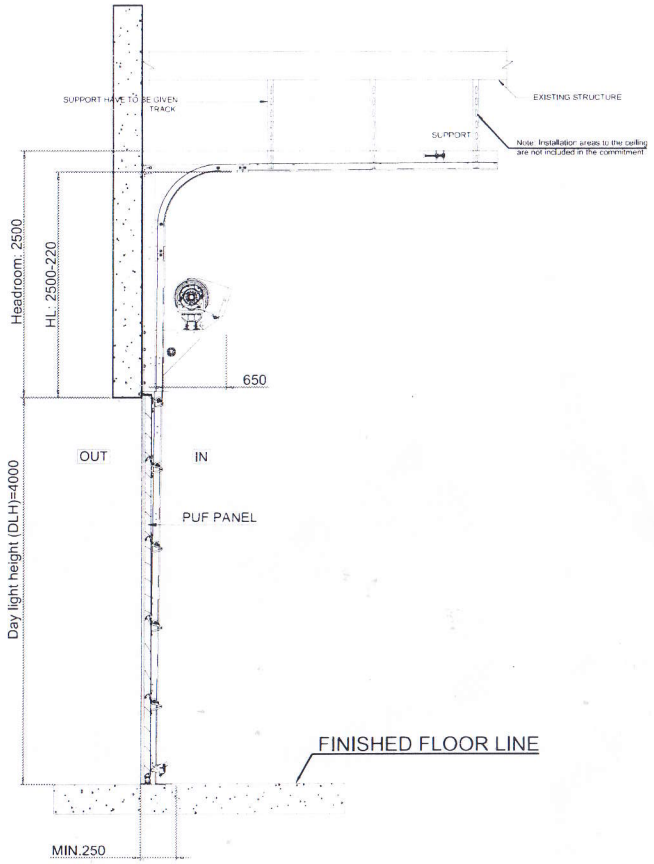

SECTION A-A

Note:- All support to be ~~pre~~ powder coated/ RAL-9002 (Do not use GI material and coating)

Boxes as per communication and Drawing

SR NO	CLEAR WIDTH	CLEAR HEIGHT	QTY	TH	EH
01	4000mm	4000mm	4	6500	2500

REV NO	DRAWN	SIGN	DESCRIPTION
R03	SURAJ		1.DOOR QTY CHANGE
R02	AKASH		1.TOTAL HEIGHT UPDATED
R01	SURAJ		1.HEIGHT CHANGED 2.GUIDE DETAIL ADDED

TOLERANCE: ±10mm

This drawing & design is the property of NIHVA TECHNOLOGIES. Not to be sold or copied to any other concern.

TITLE: SECTIONAL DOOR (HL)

NIHVA TECHNOLOGIES PVT. LTD. PUNE
Tel : 020 66304033
Website - www.nihva.com Email - info@nihva.com

	NAME	SIGN	DATE
DRAWN	SURAJ		16/07/17
CHECK	VIKRANT		16/07/17
APPROVAL	R.D		16/07/17

CLIENT -PROJECTSPOOL ENGG. SERVICE PVT. LTD.
PROJECT -
SITE - SHIRWAL.
If any queries contact : design@nihva.com
DWG. NO. : NIHVA/18-19/0087/R03 REV: 03
ALL DIMENSION ARE IN mm
SCALE: NTS WT: SHEET: 01 OF 01

PRODUCED BY AN AUTODESK EDUCATIONAL PRODUCT