


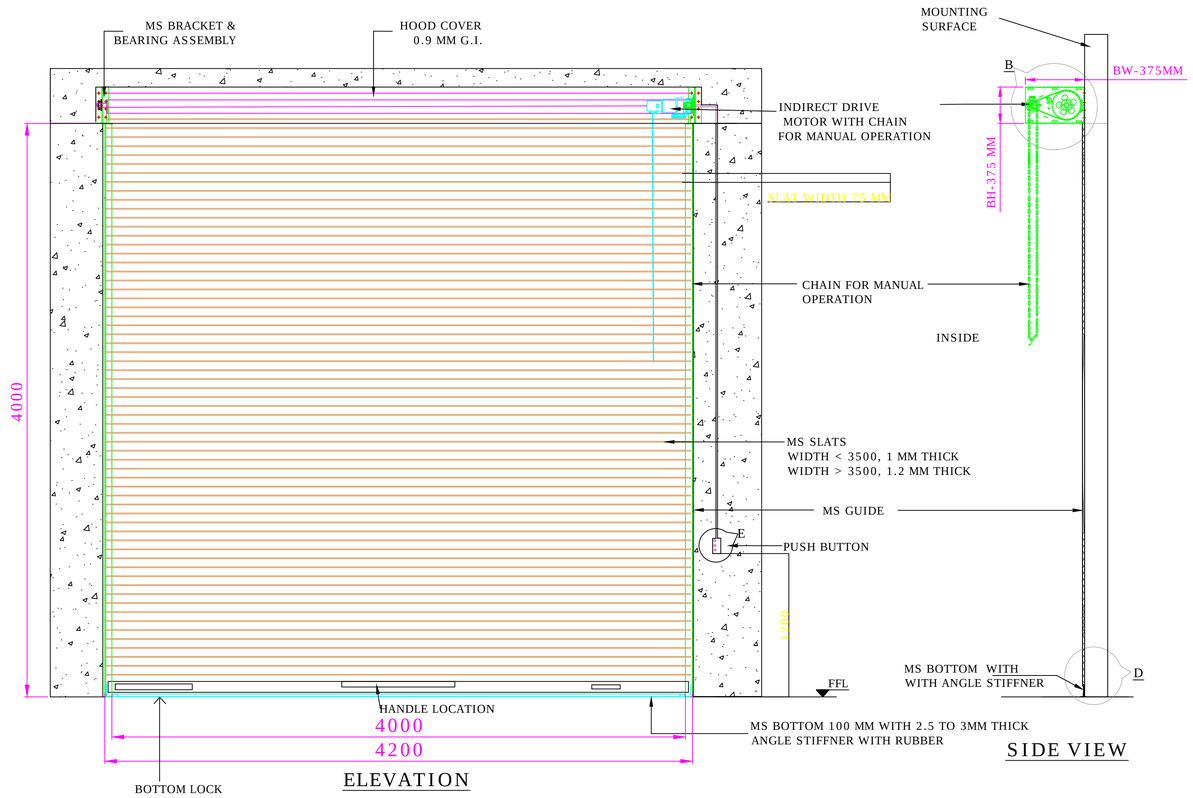


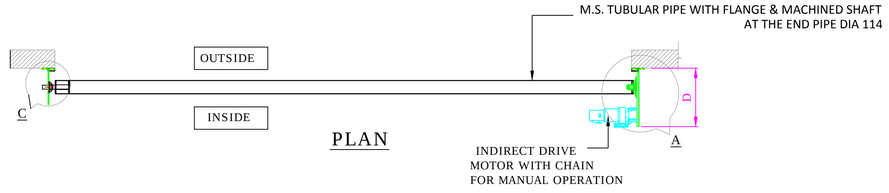


PLAN

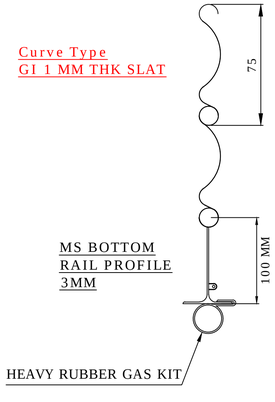


DETAILS : D

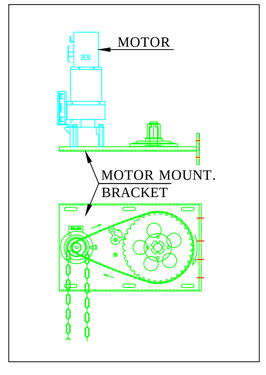

DETAILS : A & B

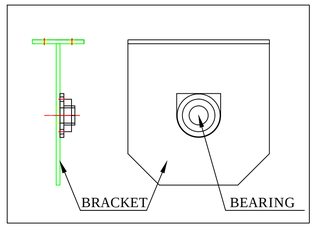

DETAILS : C

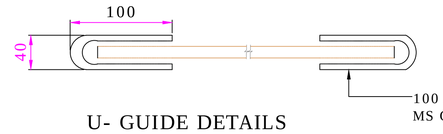

U- GUIDE DETAILS

M.S." U" SHAPED PROFILE 65 mm -150 mm x 3 mm THICK (AS PER THE OPENING w x h DIMENSION)

RAL CODE	SHADE	COLOUR
RAL 9001	CREAM	
RAL 9002	GREY WHITE	
RAL 9010	PURE WHITE	
RAL 5002	ULTRAMARINE BLUE	
RAL 7035	LIGHT GREY	
RAL 7001	SILVER GREY	

NOTES-
1. RAL SHADE NEED TO CONFIRM.
2. ROLLING SHUTTER WILL BE MOUNTED ON STRUCTURE.

1	4000	4000	1 NOS	
SR NO	CLEAR OPENING WIDTH (COW)	CLEAR OPENING HEIGHT (COH)	QUANTITY	RAL COLOR FOR PAINTING

This drawing & design is the property of NIHVA TECHNOLOGIES. Not to be sold or copied to any other concern.

TITLE MOTORIZED ROLLING SHUTTER

	NAME	SIGN	DATE
DRAWN	G.I.P.		15.12.2021
CHECK	A.K.		15.12.2021
APPRD.			

NIHVA TECHNOLOGIES PVT. LTD.
NIHVA TECHNOLOGIES PVT. LTD. PUNE
Tel : 020 66304033
Email:- info@nihva.com
Website:- www.nihva.com

CLIENT - MA ENGINEERING
PROJECT -
SITE LOCATION -
If any queries contact :design@nihva.com
DWG. NO. : NIHVA/21-22/MFG/005
REV- R00
ALL DIMENSION ARE IN mm
SCALE: NTS
WT:
SHEET: