
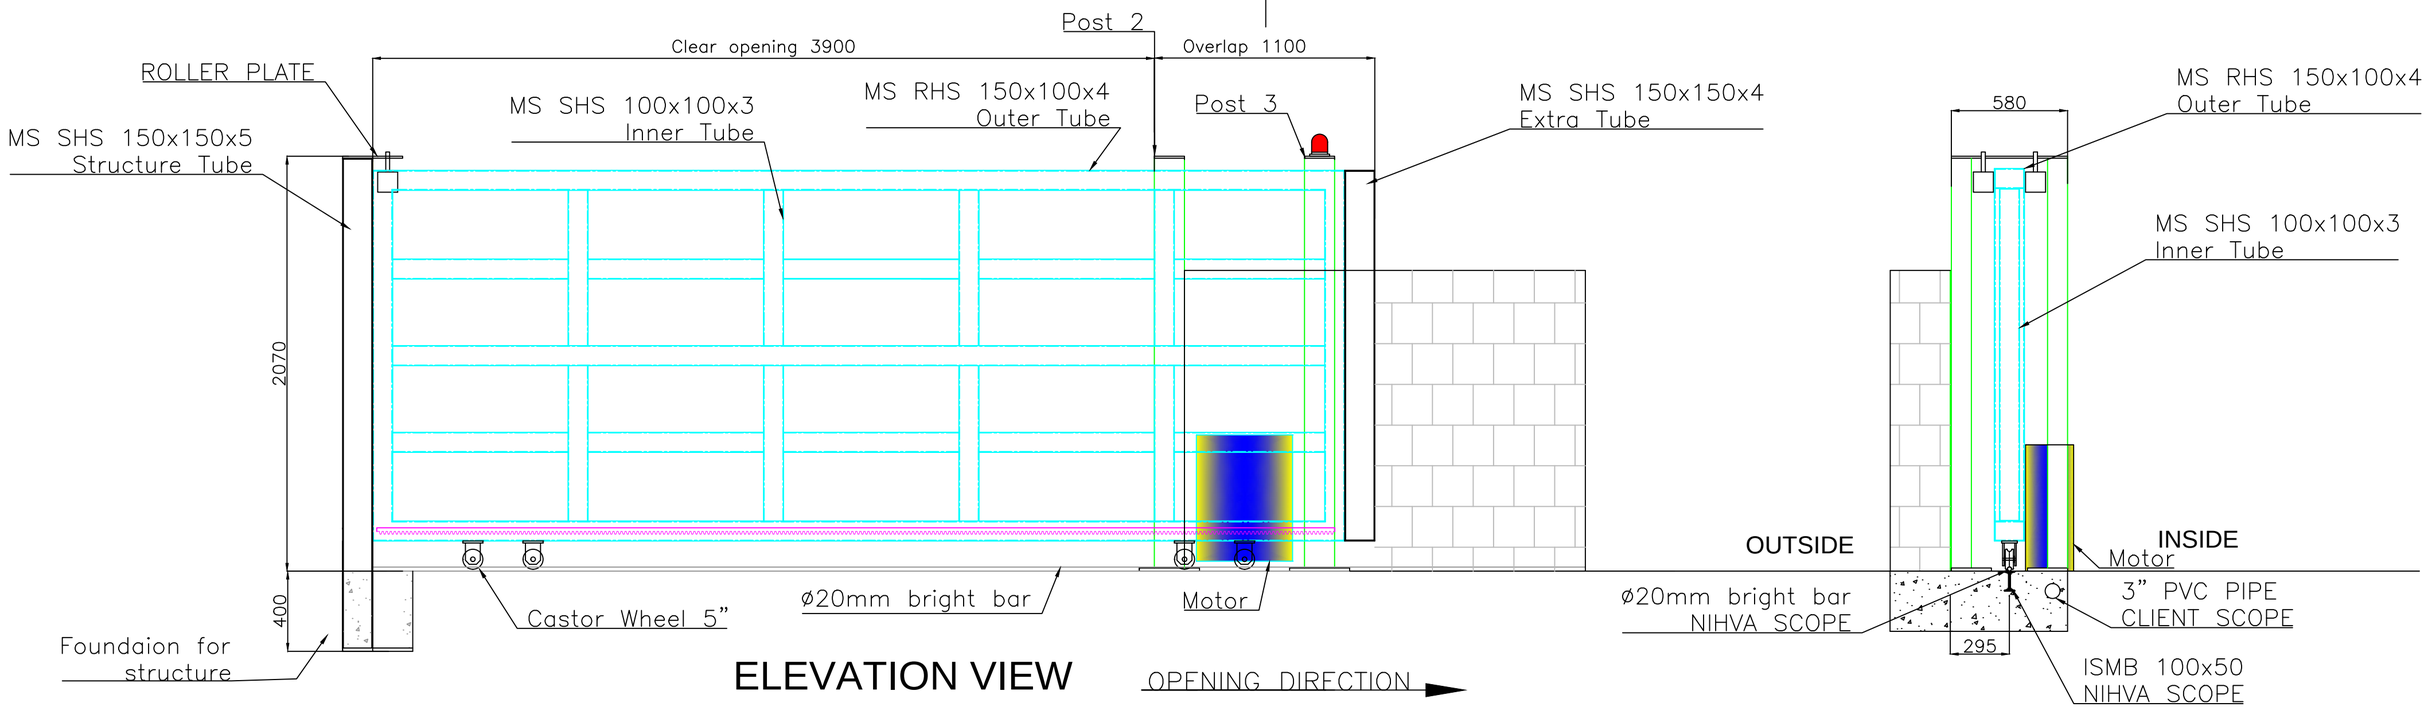


ELEVATION VIEW

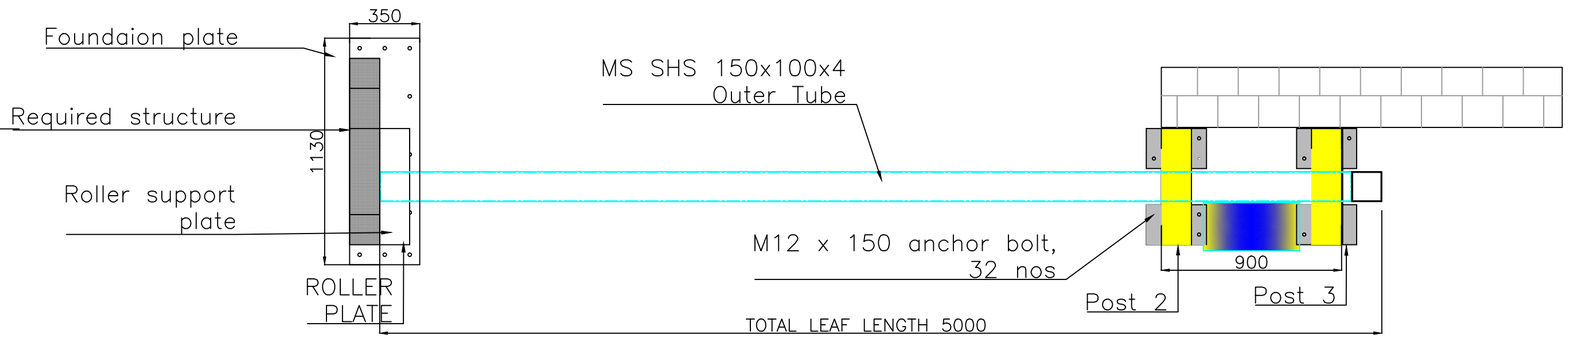

PLAN

Technical Specs of Motorized Sliding Gate

1. Opening length - 3900mm
2. Gate Height - 2000mm
3. Total leaf weight ≈ 790 kg
4. Parking length required - 5000mm
5. Outer tube size - MS SHS 150x100x4mm
6. Inner tube size - MS SHS 100x100x3mm
7. Extra support tube- MS SHS 150x150x4mm
8. Bottom Rail - Bright bar Ø20mm
9. Post size - MS SHS 150x100x4mm
10. T`Safety feature - Photocell and flashing light
11. Operation - Push button from side

Note-

1. All dimension are in mm.
2. All civil work is under client scope.
3. 3" PVC pipe in the foundation to be provided by client.
4. Power supply single phase 230v, 50hz.
5. Cable for power supply 2.5 sqmm 3 core
6. Cable for photocell - 1.5 sqmm 4 core

Rev 01-
1. Orientation changed from left to right.

Rev 02-
1. Foundation plate and structure added.
2. Post positions changed.
3. Clear opening changed to 3900.
4. Extra tube added to achieve clear opening.

Rev 03-
1. Foundation plate size reduced and shifted to right side

This drawing & design is the property of NIHVA TECHNOLOGIES. Not to be sold or copied to any other concern.

TITLE				
SLIDING (EXIT) GATE SOUTH WEST				NIHVA TECHNOLOGIES PVT. LTD. PUNE
	NAME	SIGN	DATE	Tel : 020 66304033
DRAWN	G.P.		22.01.22	Email:- info@nihva.com
CHECK	A.K.		22.01.22	Website:- www.nihva.com
APPRD.	V.T.		22.01.22	CLIENT -HAIMAVATHY PROPERTIES PVT. LTD.
If any queries contact : design@nihva.com				LOCATION - MUMBAI
				PRODUCT - SLIDING GATE 3900 X 2000
				NIHVA\20-21\191 REV- 03
ALL DIMENSION ARE IN mm				SCALE: NTS SHEET: 01 OF 02