

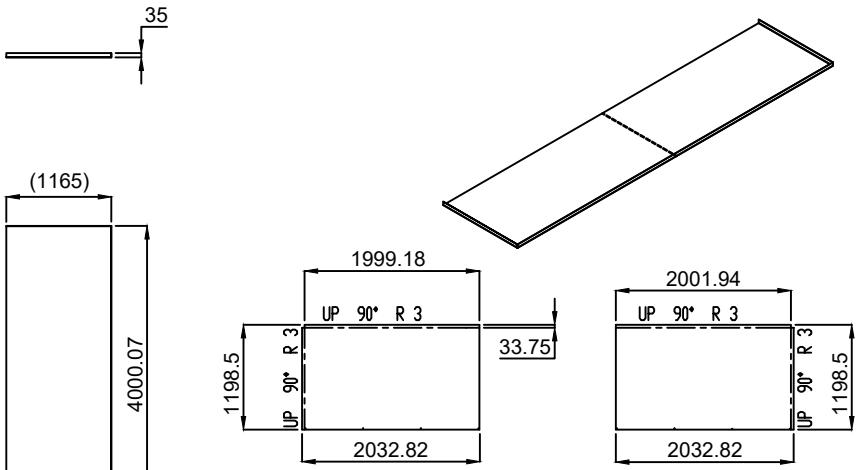


CRM DOOR 05
QTY - 2 NOS
DOWN-SIDE FOLD

CRM DOOR 05
QTY - 2 NOS
UP-SIDE FOLD

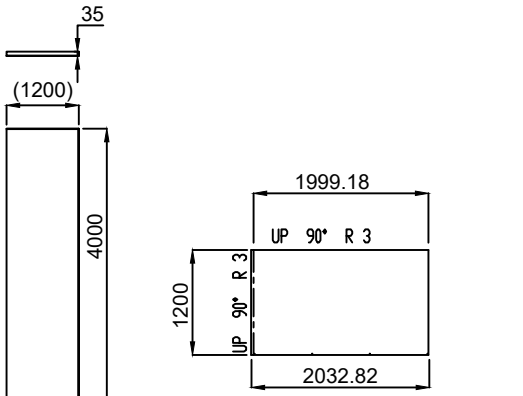


CRM DOOR 05
QTY - 8 NOS
DOWN-SIDE/UPSIDE
FOLD

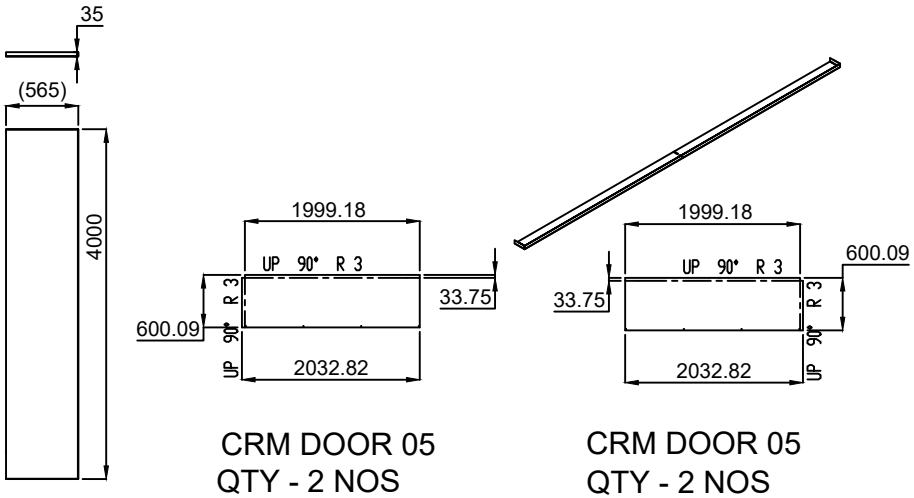

CRM DOOR 05
QTY - 2 NOS
DOWN-SIDE FOLD

CRM DOOR 05
QTY - 2 NOS
UP-SIDE FOLD

CRM DOOR ALL
QTY - 16 NOS / each
sheet all qty

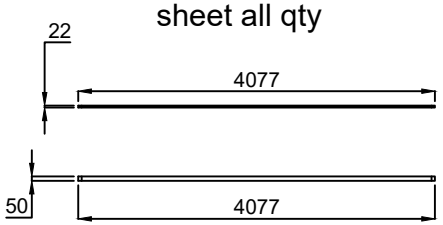

PPGI SHEET 1 MM

NOTE: DURING BENDING CRITICAL DIMENSION SHOULD BE MANDETORY

REV.	REVISION DESCRIPTION	Date	Revised By
000	MODIFIED DUE TO RECIEVED COIL SIZE 1210 MM INSTEAD OF 1250 MM	22/05/2022	MAHESH S.

This drawing & design is the property of NIHVA TECHNOLOGIES. Not to be sold or copied to any other concern.

TITLE:- 1 LEAF LH CRM DOOR 5

NIHVA TECHNOLOGIES PVT. LTD.

NIHVA TECHNOLOGIES PVT. LTD. PUNE
Tel : 020 66304033
Email:- info@nihva.com
Website:- www.nihva.com

	NAME	DATE	SIGN
DRAWN	M.SUTAR	22/05/2022	
CHECK	M.SUTAR	22/05/2022	
APPRD.			

CLIENT - NIHVA TECHNOLOGIES PVT.LTD
LOCATION -
PRODUCT - SLIDING DOOR - PPGI CLADDING
If any queries contact : design@nihva.com
DWG NO:-NIHVA/22-23/VDR/0015 REV- 0
ALL DIMENSION ARE IN mm
SCALE: NTS SCALE:-- 1:1 SHEET: 02 OF 02