

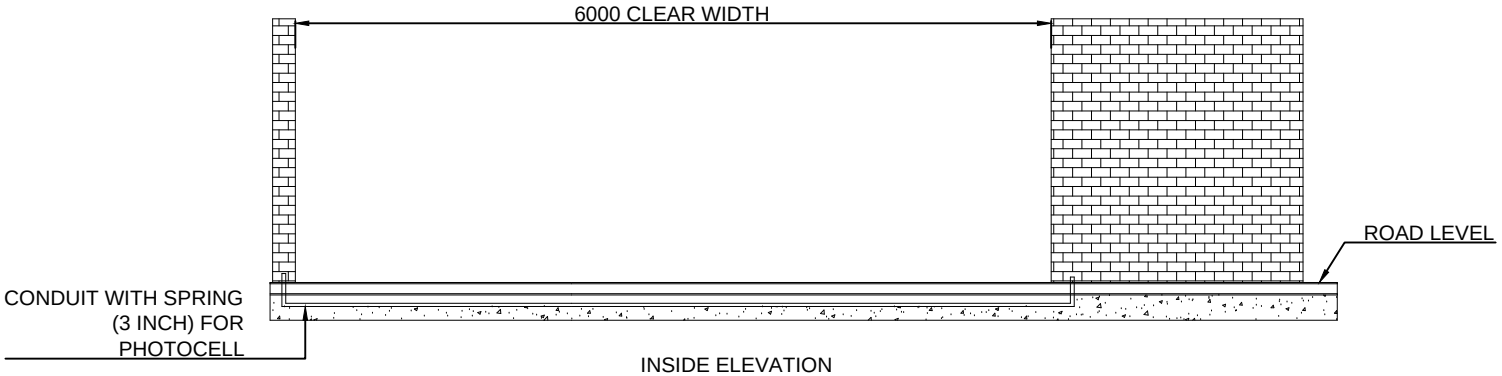


INSIDE ELEVATION

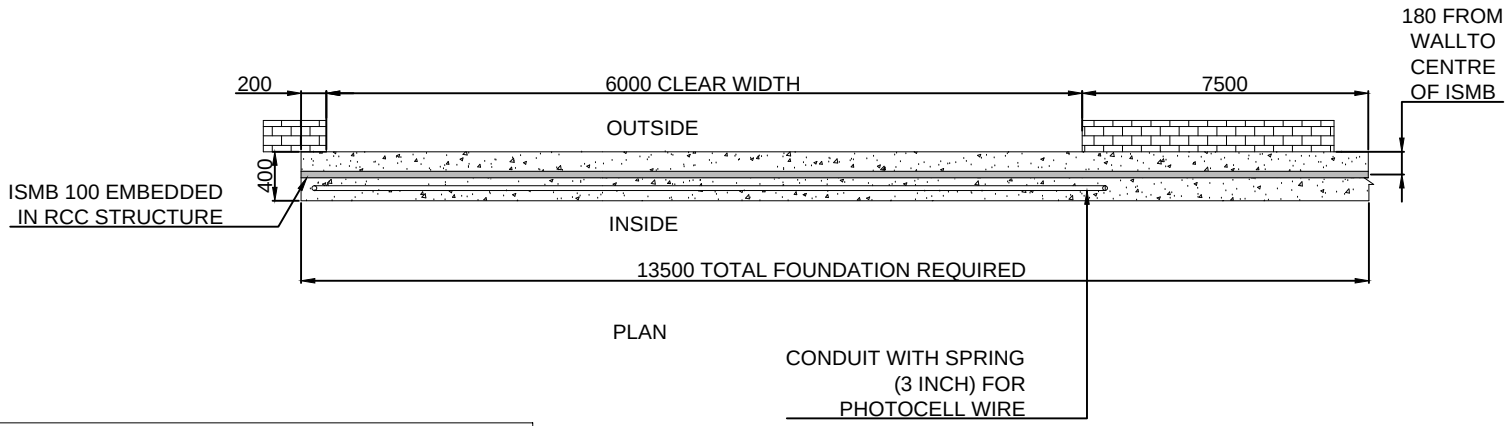

PLAN

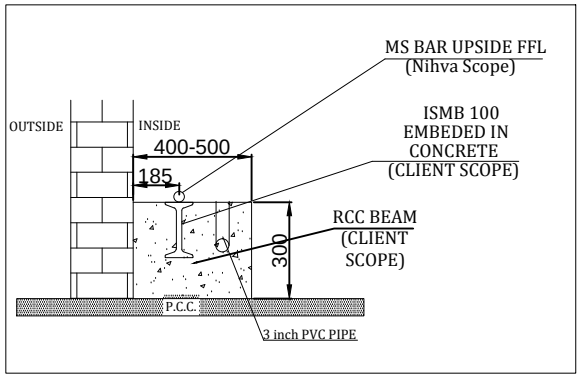

6.0m SLIDING GATE FOUNDATION

ISMB 100 X 50 X 13500L = 1 NO/GATE

This drawing & design is the property of NIHVA TECHNOLOGIES. Not to be sold or copied to any other concern.

TITLE	FOUNDATION FOR 6M SLIDING GATE			NIHVA TECHNOLOGIES PVT. LTD. PUNE Tel : 020 66304033 Email:- info@nihva.com Website:- www.nihva.com
	NAME	SIGN	DATE	
DRAWN	P.V.A		11.10.19	CLIENT - ASHOK CONSTRUCTION
CHECK				PROJECT - JOHN DEERE
REV.				SITE LOCATION - RANJANGAON
APPROVAL				DWG. NO. : NIHVA/19-20/0121
If any queries contact : projects@nihva.com				SCALE: NTS / WT: / SHEET: 01 OF 01
ALL DIMENSION ARE IN mm				