



Abbrevation's:
WOW-Wall Opening Width
WOH-Wall Opening Height
UC-Under Cut
FFL-Finished Floor Level

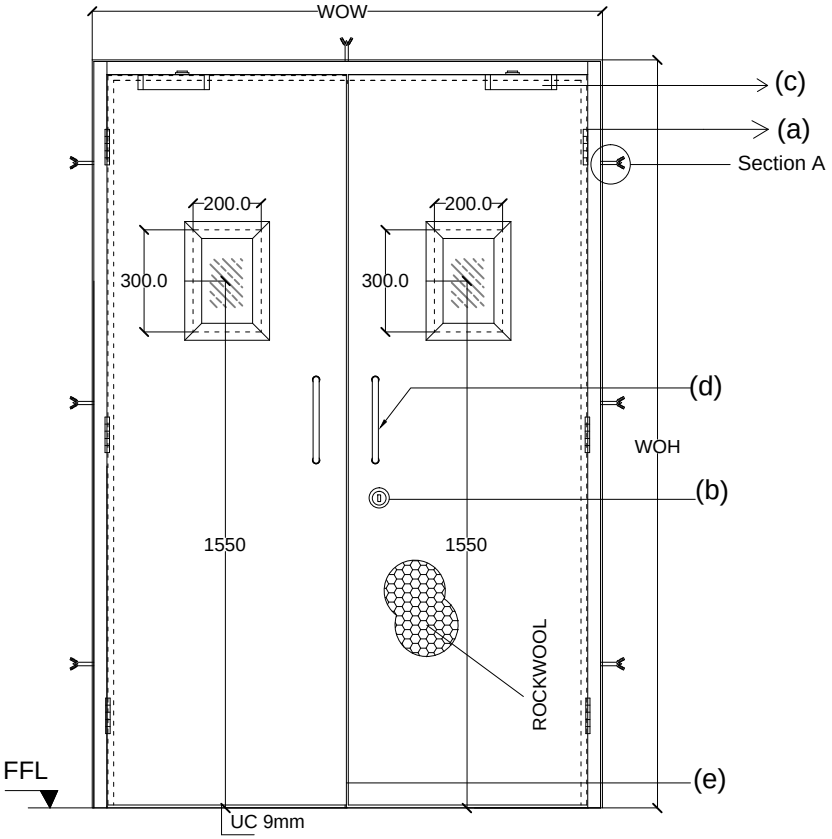

Outside Elevation



Top View

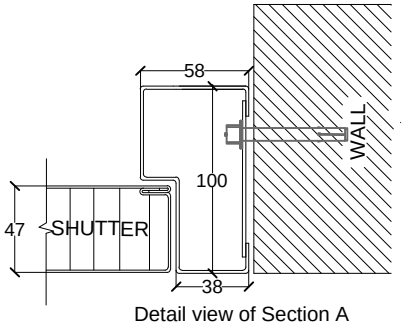

Detail view of Section A

ASSESORIES DETALES

(a) HINGES: SS hinges 100x75x3mm

(b) LOCK : Mortise dead Lock with cylinder(One side key & thumb turn on other side)with escutcheon.

(c) DOOR CLOSER : B4W

(d) HANDLE : D Handle (300x22) pair.

(e) VISION PANEL - 5mm THK. GLASS OF SIZE-200X300mm

Shutter thickness : 47 mm
Frame Sheet thick : 1.20mm
Shutter sheet thick : 0.80mm
Fixing : On Soliid Brick plasterd wall with Anchors

NOTE:- *All Dimensions are in mm.
*Tolerance:-All Linear Dimensions ±3mm,Others ±0.5mm.
*The Drawing Is For Location of Hardware only. Drawing Does Not Represent The Hardware For More Clarity, Please Go Through Hardware Broucher.

COLORS
TRAFFIC WHITE:- RAL9016
LIGHT GRAY :- RAL7035
GENTIAN BLUE :- RAL5010
SINGLE RED :- RAL3001

Door Type

WOW	WOH	TYPE 5	TYPE 6	TYPE 7	TYPE 8	QUANTITY
2000	2500			04		04

This drawing & designing is the property of NIHVA TECHNOLOGIES. Not be sold or copy to any other concern.

TITLE: STEEL DOOR (DOUBLE LEAF)

	NAME	DATE	SIGN.
DRAWN	SURAJ	25/09/17	
CHECK	SHEKHAR	25/09/17	
APPRD.	SHEKHAR	25/09/17	
REV.	01		
MFG			

ALL DIMENSION ARE IN mm

NIHVA TECHNOLOGIES PVT. LTD.
NIHVA TECHNOLOGY PVT. LTD. PUNE
Tel : 020 66304033
Email:- info@nihva.com
Website:-www.nihva.com

CLIENT -PHENIX CONSTRUCTION TECHNOLOGIES
PROJECT - SANAND GIDC
SITE LOCATION -GUJARAT
DWG. NO. - NIHVA/17-18/0161/R01 | REV- 1
SCALE:NTS | WT: | SHEET: 01 OF 01
If any queries contact : projects@nihva.com

NOTE:-
1.Client has to select door handling type from attached door handling sheet.

REV.01-(A)D HANDLE FOR BOTH LEAF
(B)DOOR CLOSER FOR BOTH LEAF