

GATE NO 2- 6m(CW) X1.8m(CH) SWING GATE

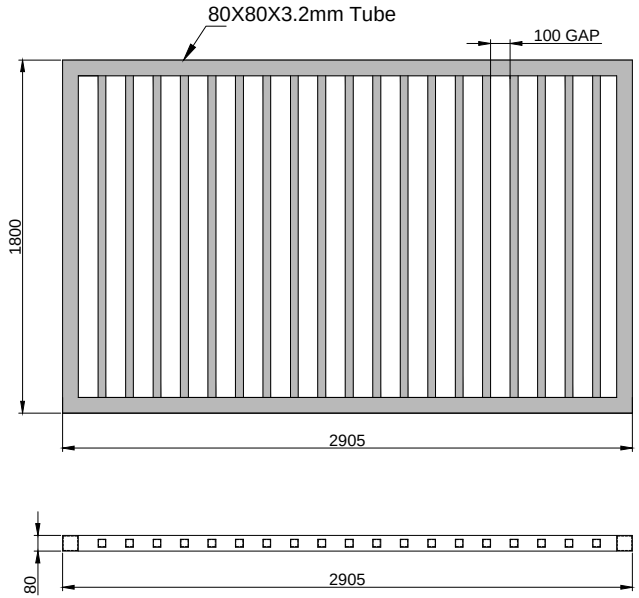


LEAF QTY- 2 NOS
NOTE- MAKE LOCKING ARRANGEMENT TO THE LEAFS. REFER ASSEMBLY DRG.

GATE NO 7- 7.2m(CW) X1.8m(CH) SWING GATE

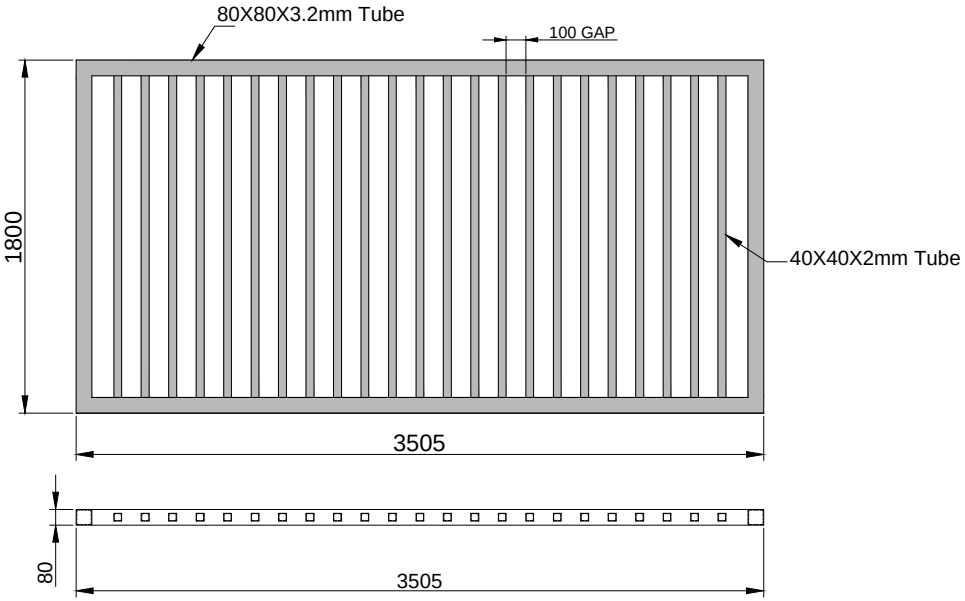


LEAF QTY- 2 NOS
NOTE- MAKE LOCKING ARRANGEMENT TO THE LEAFS. REFER ASSEMBLY DRG.

WICKET GATES- SIZE 1.5m(CW)X1.8m(CH)

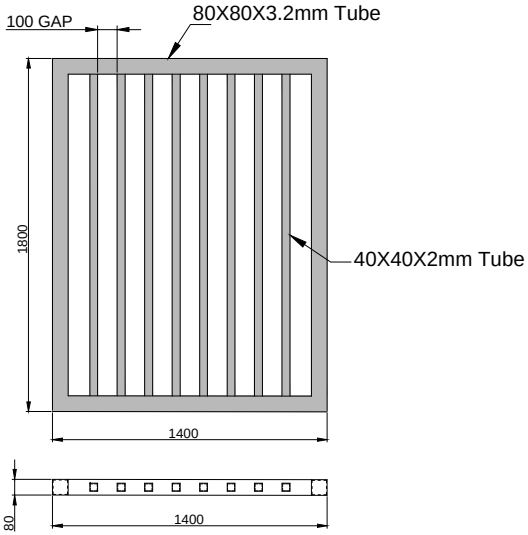


LEAF QTY- 5 NOS
NOTE- MAKE LOCKING ARRANGEMENT TO THE LEAFS. REFER ASSEMBLY DRG.

FIXING PLATE 1

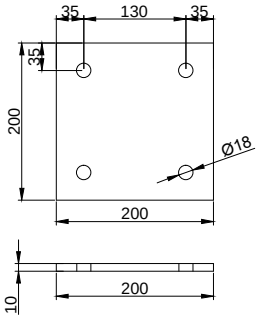

MATERIAL -MILD STEEL
THICKNESS- 10mm
QTY- 8nos

FIXING PLATE 2

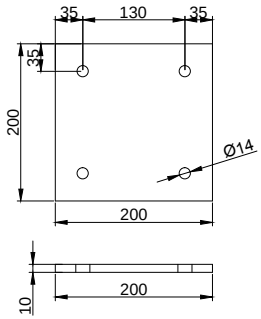

MATERIAL -MILD STEEL
THICKNESS- 10mm
QTY- 10nos

NOTE-
1. ALL REQUIRED CIVIL WORK WILL BE IN CLIENTS SCOPE.
2. ONE COAT OF RED OXIDE & TWO COAT OF APPROVED RAL SHADE WILL BE GIVEN TO THE GATE.
3.IF REQUIRED GATE LEAF WILL BE IN TWO PARTS FOR TRANSPORTATION & WILL BE WELD TOGETHER ON SITE.

SR NO	TUBE SPECIFICATION	
1	80X80X3.2mm	OUTER TUBE
2	40X40X2mm	INNER TUBE
3	GAP B/W INNER TUBES	100mm

TOLERANCE- ±10mm

This drawing & designing is the property of NIHVA TECHNOLOGIES. Not to be sold or copied to any other concern.

TITLE: GATE NO 2 & 7 & WICKET GATES & FIXING PLATES

NIHVA TECHNOLOGIES PVT. LTD. PUNE
Tel : 020 66304033
Email:- info@nihva.com
Website:- www.nihva.com

	SIGN	DATE
DRAWN	SURAJ	06/11/17
CHECK	SHEKHAR	06/11/17
APPROVAL	SHEKHAR	06/11/17

CLIENT -
PROJECT -
SITE LOCATION -
DWG. NO. : NIHVA/17-18/VDR/0171 | REV-0
If any queries contact : projects@nihva.com | SCALE: NTS | WT: | SHEET: 01 OF 01
ALL DIMENSION ARE IN mm