


THIS PRINT IS THE PROPERTY OF NIHVA IT IS TO BE USED ONLY FOR THE PURPOSE FOR WHICH IT WAS LENT
AND MUST NOT BE USED IN ANY WAY DERTIMENTAL TO THE INTEREST OF THIS COMPANY AND IS SUBJECT TO RETURN ON DEMAND.

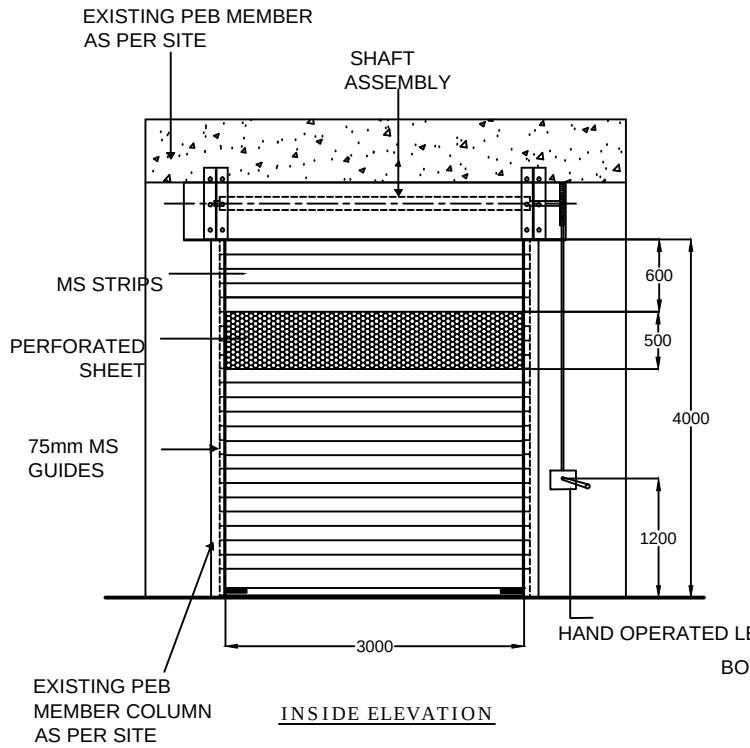


INSIDE ELEVATION

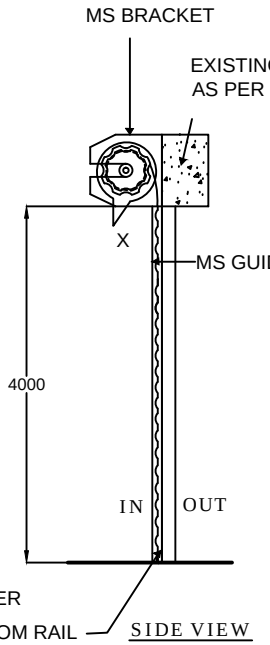


SIDE VIEW

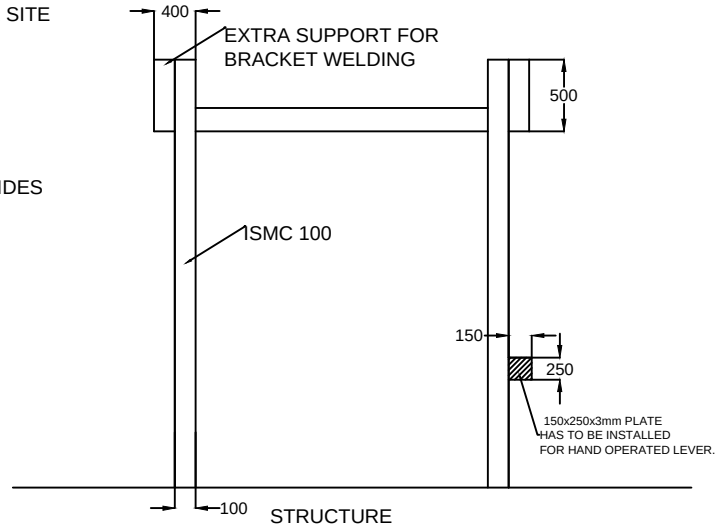


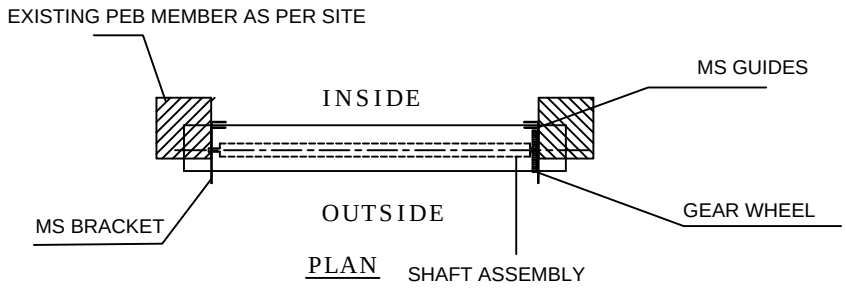

PLAN

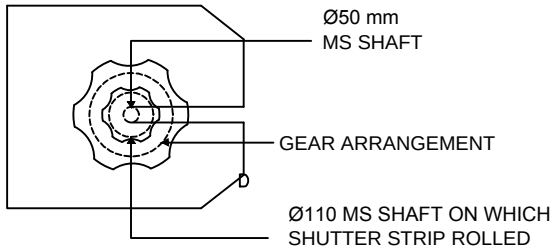

DETAIL 'X'

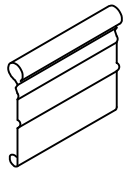

SHUTTER STRIP DETAIL

QUANTITY- 10

TITLE: ROLLING SHUTTER (GEAR OPERATED)	DO NOT SCALE DRAWING		
		SIGN	DATE
CLIENTS APPROVEL:-	DRAWN: OMKAR		16-02-16
	CHECK: ANIL		16-02-16
	ENG		
	APPRD.		
UNLESS & OTHERWISE SPECIFIED DIMENSION ARE IN M.M.	PROD		
	MFG		
	Ref. No.		

NIHVA TECHNOLOGIES PVT. LTD.

NIHVA TECHNOLOGIES PVT. LTD. Pune:-411044
Tel :- 020 66304033
Email :- info@nihva.com

CLIENT:		
PROJECT / SITE:		
PRODUCT NAME:		
DWG. NO.:NIHVA/15-16/		REV.: 0
SCALE: NTS	WT:	SHEET: 1 OF 1