
AS PER SITE VISIT MEASUREMENT

RETRACTABLE ROOF

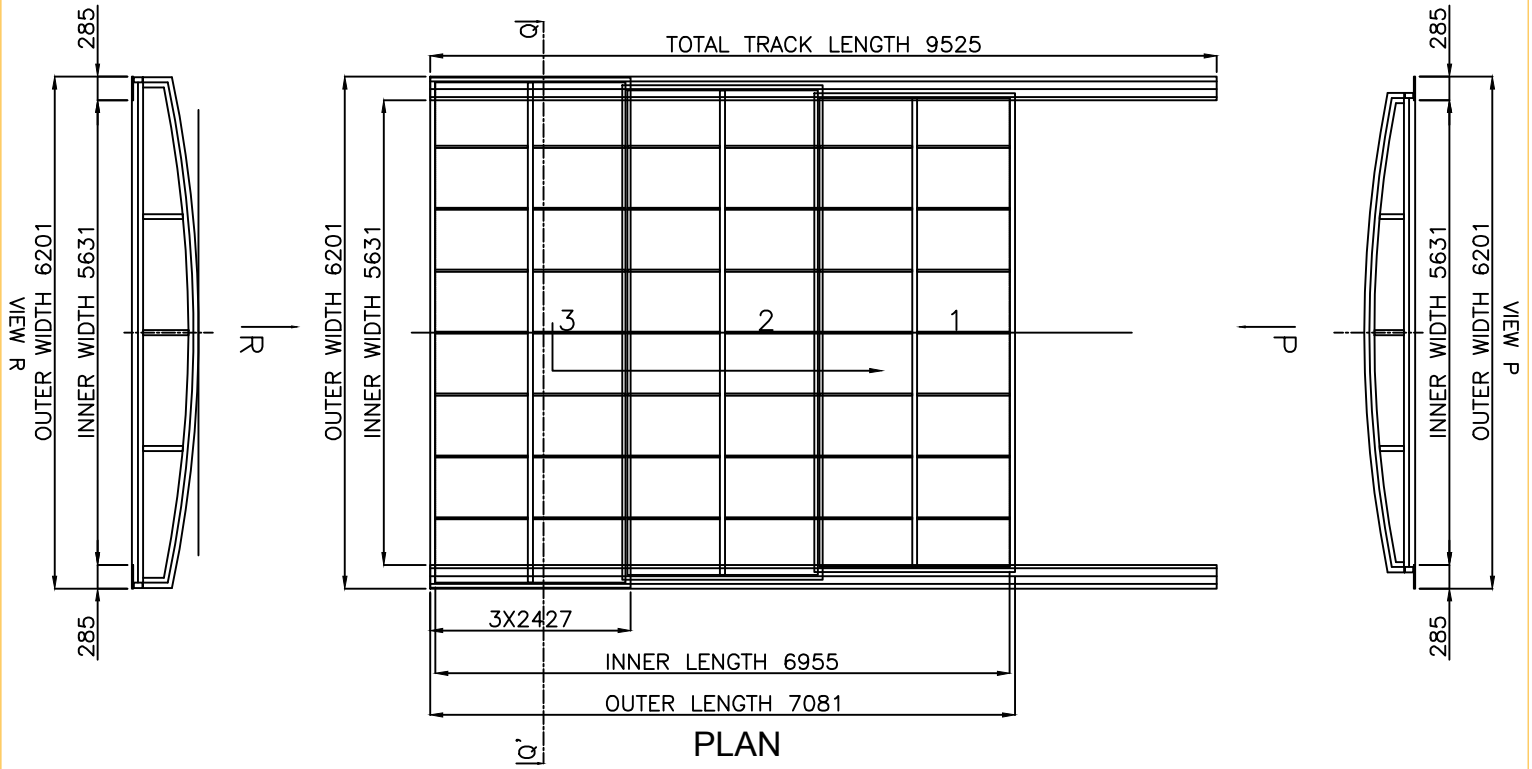


PLAN

ALL DIMENSION ARE IN MM

PROFILE	3X PROGRES, WHITE
INNER LENGTH OF ENCLOSURE	6955mm
OUTER LENGTH OF ENCLOSURE	7081mm
INNER WIDTH OF ENCLOSURE	5631mm
OUTER WIDTH OF ENCLOSURE	6201mm
TOTAL HEIGHT OF ENCLOSURE	808mm
LENGTH OF SEGMENTS	3X 2427mm
RAIL	2X 2-Track-9525mm
POLYCARBONATE SHEET	CLEAR COMPACT, 3mm
LARGE FACE	MOVING WITH SEGMENT 3
SMALL FACE	MOVING WITH SEGMENT 1
LATERAL DOOR	None
FOIL EPDM(BLACK)	100mm
MOTORS	Motorized

Index	Date	Name	Designation	Sheet	Scale
Drawn	05/06/19	RAGHU	RETRACTABLE ROOF	B	NTS
Chkd	05/06/19	PURUSH			

Drg.No.	Customer Drg.No.	
MVRR-351	MR. PREETESH BHAI	MEGAVENT TECHNOLOGIES

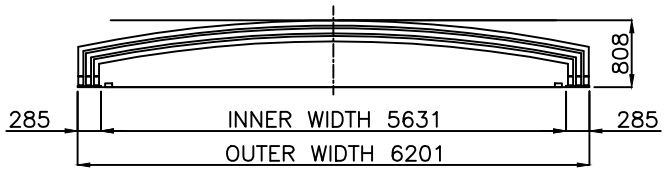

SECTION Q-Q'

Wt. per m² ≈ 13 kg/m²

Total Area ≈ 44 m²

Total Load on given area ≈ 572 kg