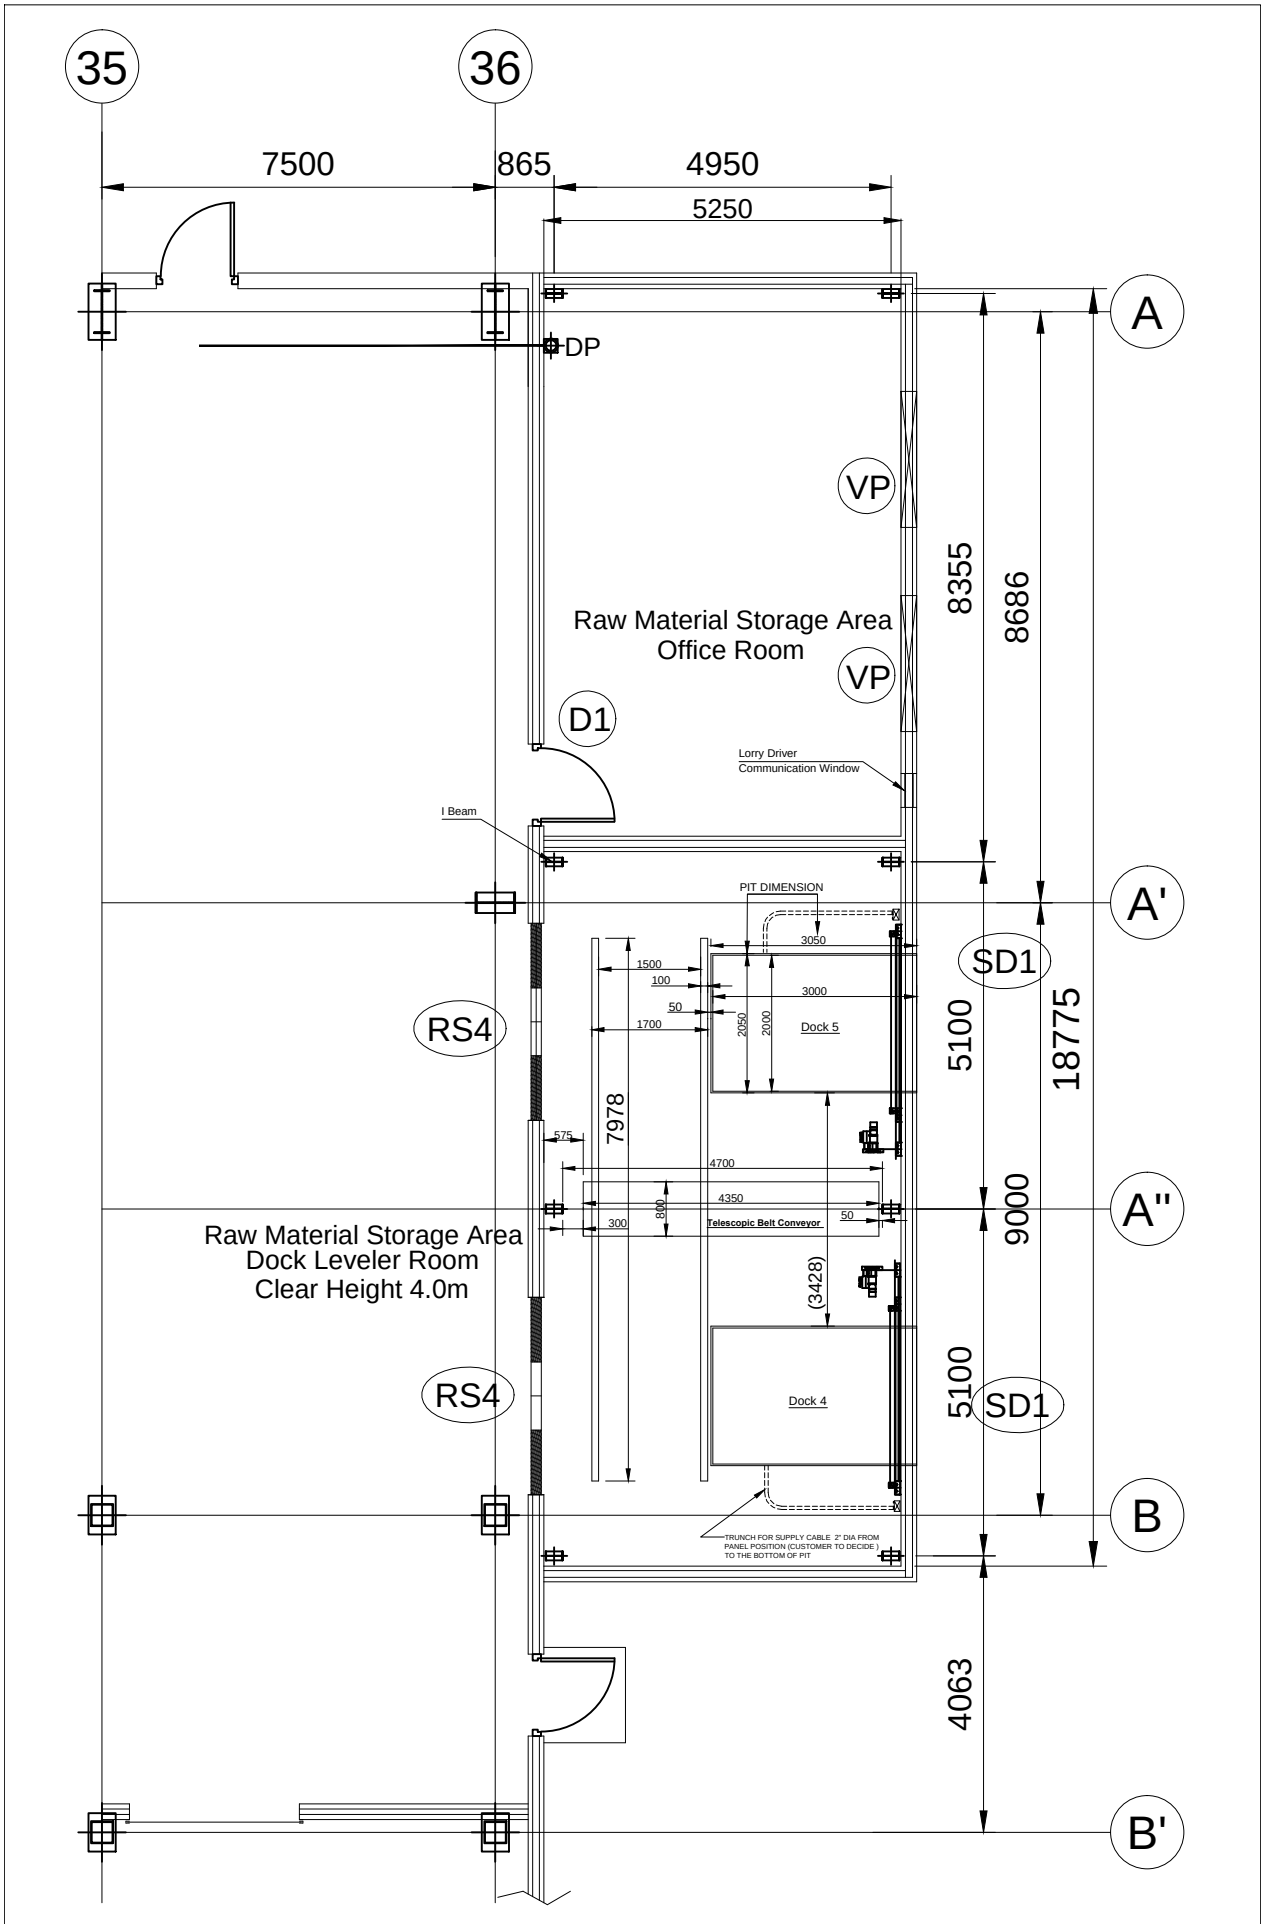

35
36
7500
865
4950
5250
A
DP
VP
8355
8686
Raw Material Storage Area
Office Room
VP
D1
Lorry Driver
Communication Window
I Beam
PIT DIMENSION
A'
3050
SD1
1500
100
50
1700
3000
2050
2000
Dock 5
RS4
5100
18775
7978
575
4700
4350
800
300
Telescopic Belt Conveyor
50
A''
9000
Raw Material Storage Area
Dock Leveler Room
Clear Height 4.0m
(3428)
RS4
Dock 4
5100
SD1
B
TRUNCH FOR SUPPLY CABLE 2" DIA FROM
PANEL POSITION (CUSTOMER TO DECIDE )
TO THE BOTTOM OF PIT
4063
B'