| | |
|---|---|
| CAPACITY | 2 TON |
| PLATFORM SIZE | 3000(L) X 2000(W) |
| POWER PACK | 3 HP, 3 PH |
| SHUT HEIGHT | 600 MM |
| LIFT HEIGHT | 1600 MM |
| OPEN HEIGHT | 2200 MM |

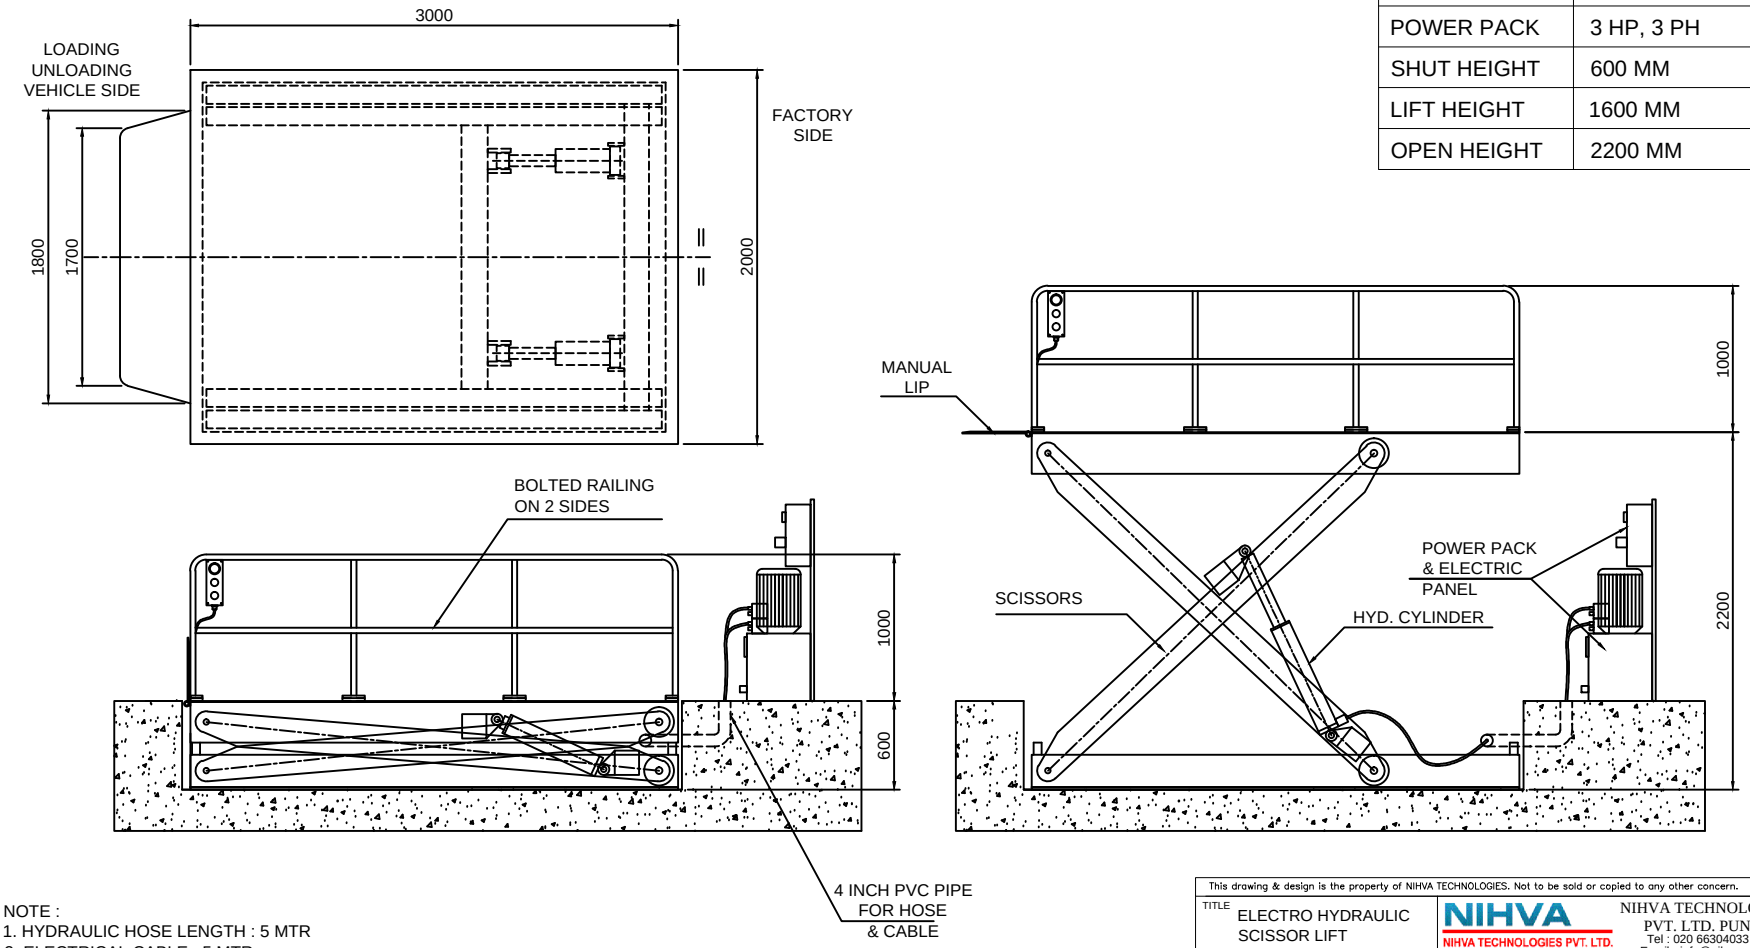


NOTE :
1. HYDRAULIC HOSE LENGTH : 5 MTR
2. ELECTRICAL CABLE : 5 MTR
3. PIT / CIVIL / PVC PIPE WILL BE IN CLIENT SCOPE.
4. INPUT SUPPLY : 3 PHASE 400 VOLT WITH NEUTRAL.

This drawing & design is the property of NIHVA TECHNOLOGIES. Not to be sold or copied to any other concern.

TITLE: ELECTRO HYDRAULIC SCISSOR LIFT

| | NAME | SIGN | DATE |
|---|---|---|---|
| DRAWN | P.A | | 20.11.2019 |
| CHECK | G.J | | 20.11.2019 |
| APPRD. | | | |

NIHVA TECHNOLOGIES PVT. LTD.
NIHVA TECHNOLOGIES PVT. LTD, PUNE
Tel : 020 66304033
Email:- info@nihva.com
Website:- www.nihva.com

CLIENT - MYLAN LABORATORIES LTD
PROJECT -
SITE LOCATION - INDORE
If any queries contact : design@nihva.com
DWG. NO. : NIHVA/19-20/0157 REV- 0
ALL DIMENSION ARE IN mm
SCALE: NTS WT: SHEET: 01 OF 01