
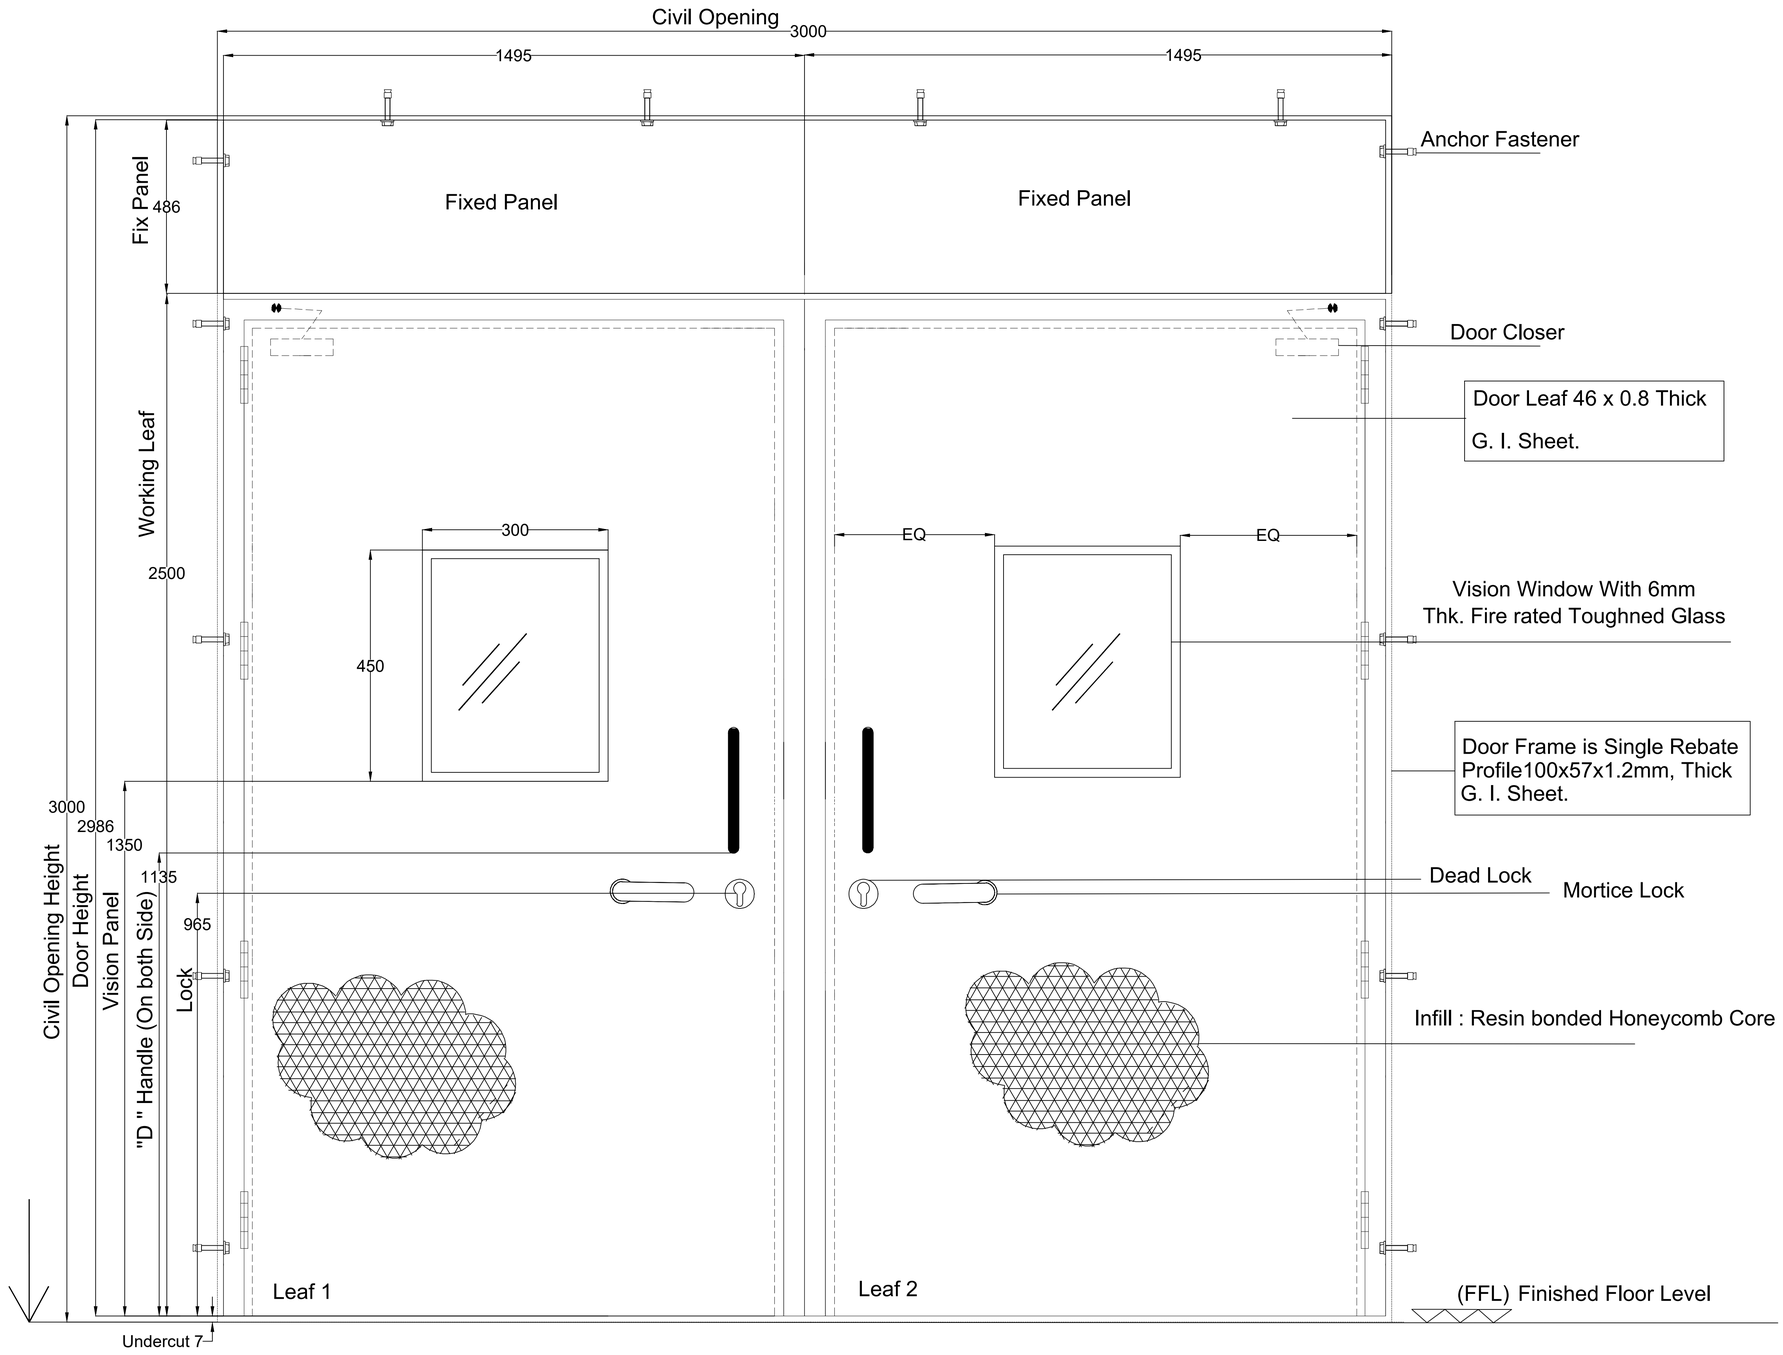


ELEVATION

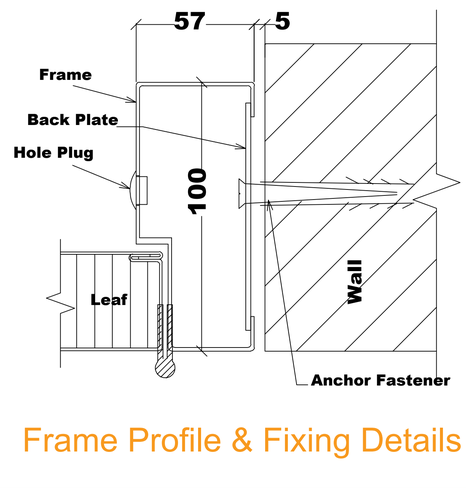

Frame Profile & Fixing Details

Technical Specification :

Door Frame : Single Rebate Profile100x57x1.2mm, Thick G.I. Sheet
Door Leaf : 46 x 0.8 Thick G.I. SHEET
Vision Window : 6 mm Thk. Fire rated Toughned Glass (300 x 450 mm)
Coating : etched primer coating, stove zinc phosphate primer and thermosetting PU aliphatic grade paint of approved colour
Testing Required : Minimum 250 hours of salt spray test for both Leafs
Accessories : Door Closer,SS Ball Bearing Hinges ,Both Side Handle Key Operation Mortice Lock , Bottom Closer

FINISH SIZE :

Width (FW)	Height (FH)	QTY
3000	**3000**	01

NOTES :

1:All Dimensions are in mm

2:Tolerances - All linear dimensions +/- 3mm, others +/- 0.5mm

3:All civil work is in client scope

This drawing & design is the property of NIHVA TECHNOLOGIES. Not to be sold or copied to any other concern.

TITLE: DOUBLE LEAF STEEL DOORS				NIHVA TECHNOLOGIES PVT. LTD.	
	NAME	DATE	SIGN		
DRAWN	S.J	20/02/2023		CLIENT -	
CHECK	A.K	20/02/2023		LOCATION -	
APPRD.	V.T	20/02/2023		PRODUCT - STEEL DOOR	
If any queries contact : design@nihva.com				DWG NO:-NIHVA\23-24\XXX	REV- 0
ALL DIMENSION ARE IN mm				SCALE: SCALE :1:1	SHEET: 01 OF 01

NIHVA TECHNOLOGIES
PVT. LTD. PUNE
Tel : 020 66304033
Email:- info@nihva.com
Website:- www.nihva.com