THIS DRAWING & DESIGN IS THE SOLE PROPERTY OF VMS & SHALL NOT BE COPIED, TRACED OR REPRODUCED BY ANY MEANS WITHOUT PRIOR WRITTEN CONSENT OF THE FIRM.

GENERAL NOTES :

1. ALL THE DIMENSIONS ARE UNFINISHED DIMENSIONS.
2. ALL DIMENSIONS ARE IN MM AND LEVELS ARE IN MT, UNLESS OTHERWISE MENTIONED.
3. ALL THE DIMENSIONS SHALL BE READ & NOT TO BE MEASURED.
4. IN CASE OF ANY DISCREPANCY, BRING IT TO THE NOTICE OF THE ARCHITECT IMMEDIATELY.
5. DETAIL DRAWING PRECEDES THE GENERAL DRAWING

STANDARD DRAWING SYMBOLS:

+ FINISHED LEVEL
+ UNFINISHED LEVEL

SECTION SYMBOL
UPPER HALF INDICATES DIAGRAM NO.
(NUMERICAL VALUE) IN DRAWING SHEET &
LOWER HALF INDICATES DRAWING NO.

ELEVATION SYMBOL
UPPER HALF INDICATES DIAGRAM NO. IN DRAWING
SHEET & LOWER HALF INDICATES DRAWING NO.

WINDOW SYMBOL
UPPER HALF INDICATES WINDOW NO. &
LOWER HALF INDICATES DRAWING NO.

DOOR SYMBOL
UPPER HALF INDICATES DOOR NO. &
LOWER HALF INDICATES DRAWING NO.

GRAPHIC LEGEND :

MASONRY CUT IN PLAN/SECTION.

RCC COLUMN CUT IN PLAN.

IMPORTANT NOTE :

SCHEDULE OF FLOORING (IN CIVIL SCOPE)

F1	VITRIFIED TILES FLOORING	F3	BRICK BAT COBA WATER PROOFING + HEAT REFLECTIVE TILE
F2	VITRIFIED TILES FLOORING & DADO		

SCHEDULE OF OPENINGS:


MKD.	SIZE	SILL HT.	LINTEL HT.	TOTAL NO.	REMARKS
D101	1935x2400	----	2400	2	ALUMINUM FRAME WITH GLASS DOOR
D102	1200x2400	----	2400	1	ALUMINUM FRAME WITH FLUSH DOOR
D103	900x2400	----	2400	4	ALUMINUM FRAME WITH GLASS DOOR
D104	800x2400	----	2400	3	ALUMINUM FRAME WITH FLUSH DOOR
W101	2975x1650	750	2400	1	ALLUMINIUM SLIDING WINDOW
W102	2545x1650	750	2400	1	ALLUMINIUM SLIDING WINDOW
W102a	2545x1650	750	2400	1	ALLUMINIUM SLIDING + FIXED GLASS WINDOW
W103	1935x1650	750	2400	4	ALUMINUM FRAME WITH FIXED GLASS WINDOW
V101	750x600	1800	2400	3	ALUMINUM FRAME WITH ALU. LOUVERS


FOR TENDER

NO.	DATE	DESCRIPTION	DRAWN BY	CHECKED BY


REVISION HISTORY

KEY PLAN
SCALE : N.T.S.

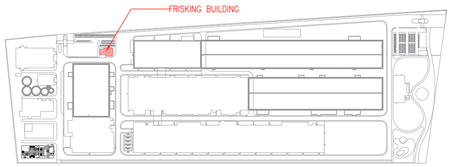


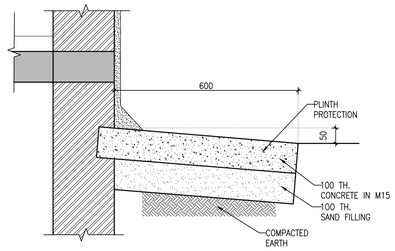


A TYPICAL PLINTH PROTECTION DETAIL
SCALE 1:10

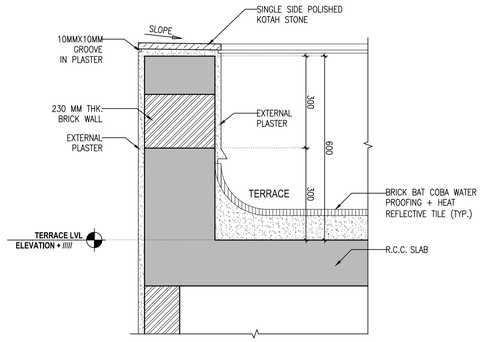

B TYPICAL PARAPET DETAIL
SCALE 1:10

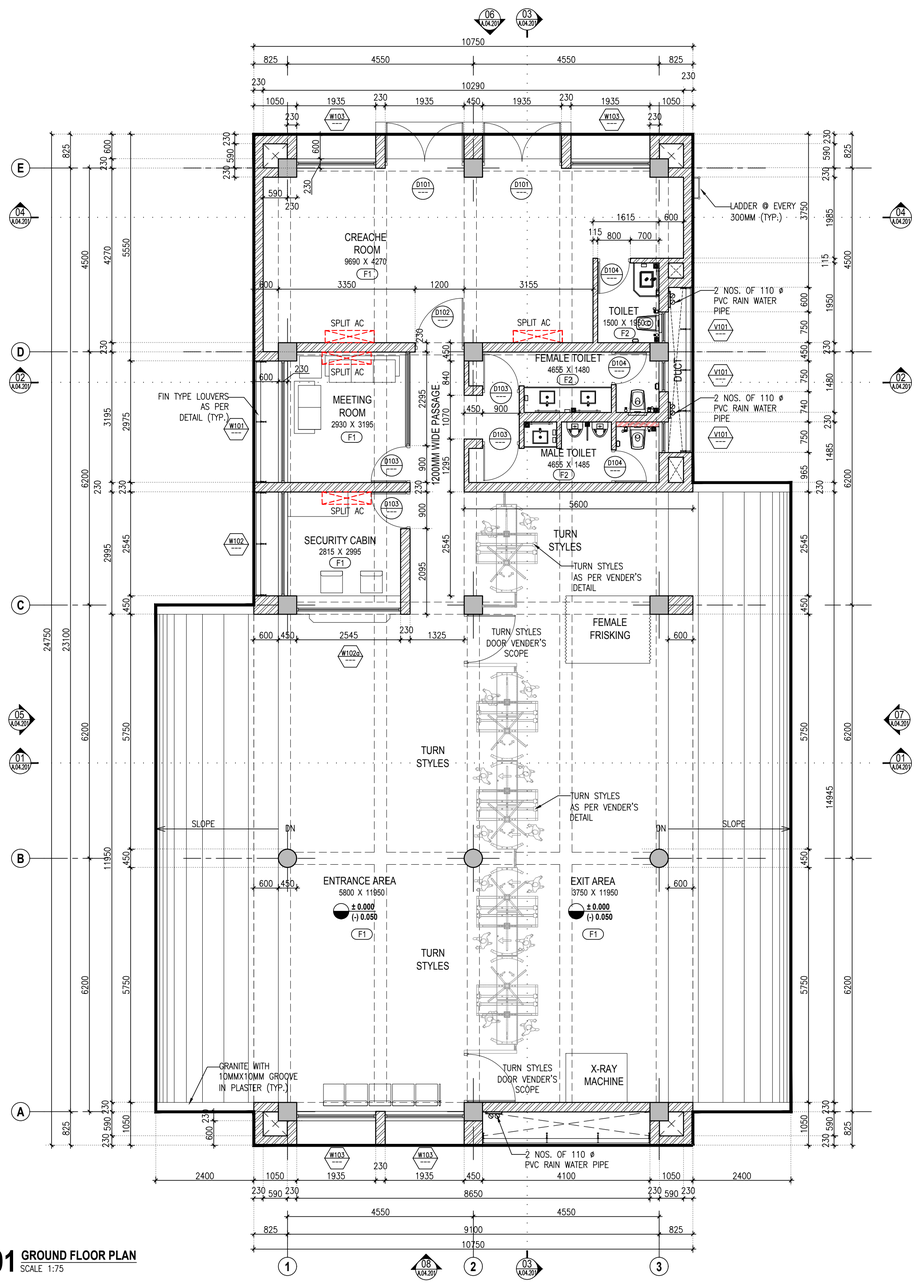

01 GROUND FLOOR PLAN
SCALE 1:75

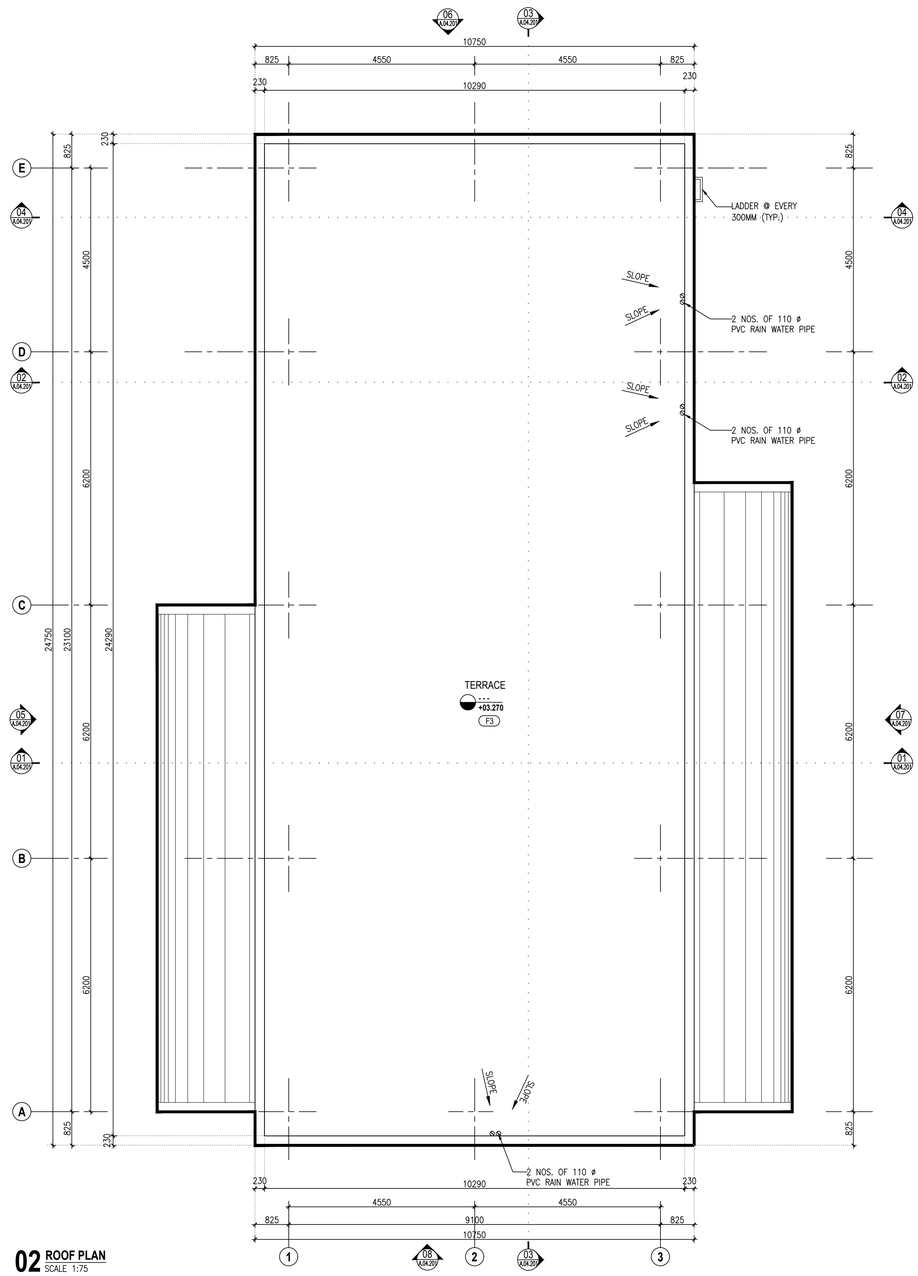

02 ROOF PLAN
SCALE 1:75

REFERENCE DRAWINGS :

01. ARCHITECTURAL :	A.4.201
02. STRUCTURAL :	-
03. HVAC :	-
04. ELECTRICAL :	-
05. UTILITIES :	-

FLOOR PLAN & DETAIL

FRISKING BUILDING

AGRAWAL METAL WORKS(P) LTD.

PROJECT NO.	SCALE :	DRAWN :	ASHISH C.
3824	AS PER MARKED	CHECKED:	DARSH D.
	DATE : 03-12-2024	APPROVED:	DARSH D.
		COORDINATION CHECKED:	DARSH D.

VMS ENGINEERING & DESIGN SERVICES (P) LTD.
CHITRAKOOT FLATS, B/H TIMES OF INDIA, OFF ASHRAM ROAD,
AHMEDABAD-380 009. PHONE: +91 (079) 2658-8829, 4023-6236
WWW.VMSCONSULTANTS.COM

SHEET SIZE	DRAWING NO.	TENDER	REVISION:
A1	T.A.8a.101	T	R0