
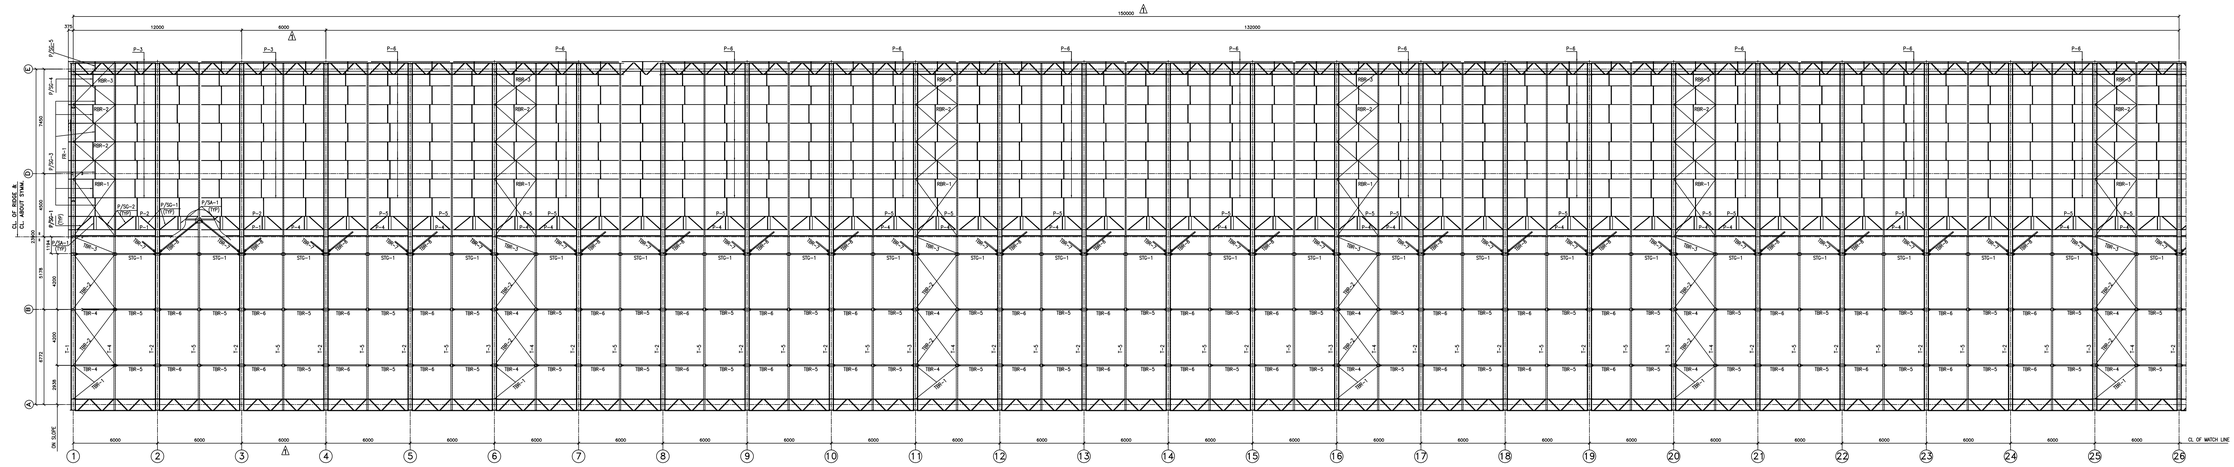


TOP, RAFTER & BOTTOM CHORD PLAN

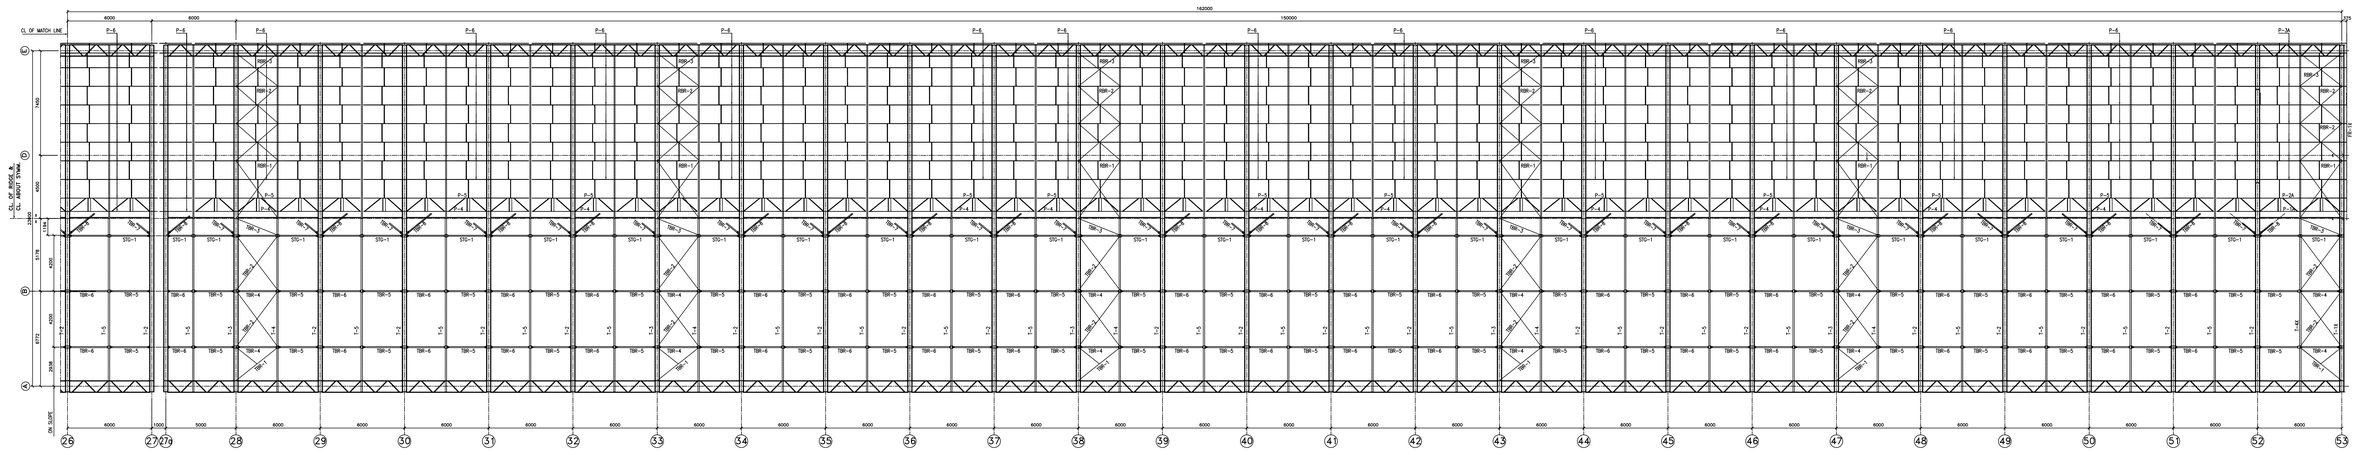

TOP, RAFTER & BOTTOM CHORD PLAN

NOTES:-
1. ALL DIMENSIONS ARE IN mm.
2. FOR DETAIL OF TRUSS, BRCGS. ETC. REFER RELEVANT STRUCTURAL FABRICATION DRGS.

REV	REVISION DETAILS	NO.OF REV. MARKS	DRAWN	CHECKED	REVIEWED: MECH.	PRO.&UTIL.	ELEC.	INST.	CIVIL	STRL.	APPROVED	DATE
6												
5												
4												
3												
2												
1	REVISED AS PER OUTOTEC COMMENTS DT. 20.08.08 & MKD △		D.BERA	AL.							AM.	21.08.08

SL.NO.	DRG. PRPD. BY	DESCRIPTION	DRAWING NO.	SHT	REV
6					
5					
4					
3					
2					
1					

REFERENCE DRAWINGS

	DESIGNED	DRAWN	CHECKED	REVIEWED: MECH.	PRO.&UTIL.	ELEC.	INST.	CIVIL	STRL.	APPROVED
DATE		01.07.08	02.07.08	04.07.08					04.07.08	04.07.08
SIGN.									AL	A.M
NAME		D BERA	N.K	S.D						

1. DO NOT SCALE, IF ANY DOUBT PLEASE ASK.
2. REVISION MARKS ARE INSCRIBED IN △

THIS DRAWING IS MBE'S PROPERTY AND MUST NOT BE USED EXCEPT IN CONNECTION WITH MBE'S WORK. REPRODUCTION, USE OR DISCLOSURE OF THE CONTENTS OF THIS DRAWING TO THIRD PARTY/IES WITHOUT EXPRESS / WRITTEN PERMISSION OF MBE IS STRICTLY PROHIBITED.

CLIENT: VEDANTA ALUMINA LTD, JHARSUGUDA, INDIA

PROJECT: THREE UNITS OF GREEN ANODE PLANT

TITLE: PETCOKE STORAGE SHED
G.A.& MARKING OF PURLIN,TRUSS,RAFTER & BOTT. CHORD BRCGS. ETC.

mbe PROJECTS DIVISION — McNally Bharat ENGINEERING COMPANY LIMITED, 4, MANGOE LANE, KOLKATA, INDIA

MBE ~~PROPOSAL~~/SO NO.: 08901

SCALE: 1 : 20

MBE DRAWING NUMBER: 1-B014-404-05-003

SHT NO.: 1 OF 1

REV: 1

SHT-A0

DG FILE : 1-B014-404-05-003_SHT1-R1

ST-A-001 (REV-1) DT-10.07.2001