




ELEVATION

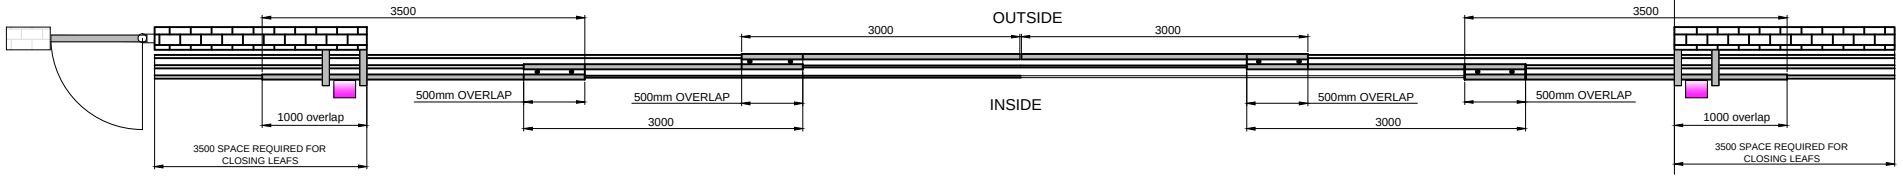

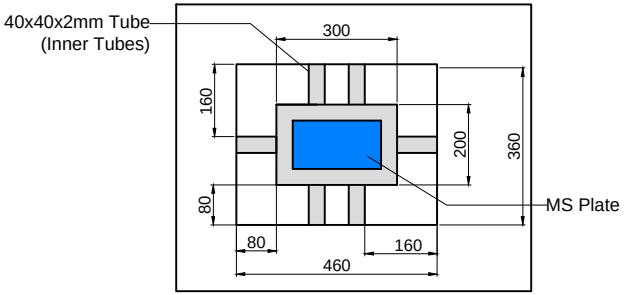

DETAILED VIEW OF A

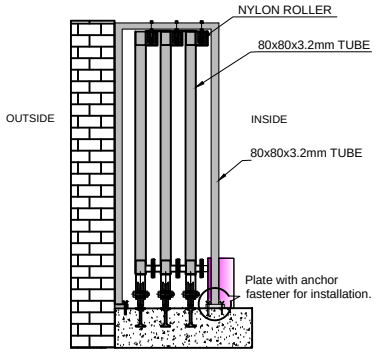

Clear Opening size -15000mm x 1500mm
Total No. of Leaf - 6 Leaf
Outer Tube Size-80x80x3.2mm
Inner Tube Size-40x40x2mm
NOTE :- *ALL REQ. CIVIL WORK WILL BE IN CLIENT SCOPE.

TOLERANCE - ±10mm

This drawing & design is the property of NIHVA TECHNOLOGIES. Not to be sold or copied to any other concern.


TITLE
TELESCOPIC GATE & WICKET GATE

NIHVA TECHNOLOGIES PVT. LTD.
NIHVA TECHNOLOGIES PVT. LTD. PUNE
Tel : 020 66304033
Email:- info@nihva.com
Website:- www.nihva.com

	NAME	SIGN	DATE
DRAWN	OMKAR		30-03-2018
CHECK	PRADEEP		30-03-2018
APPRD.	PRADEEP		30-03-2018


CLIENT -
PROJECT -
SITE LOCATION -

If any queries contact : design@nihva.com
DWG. NO. : NIHVA/17-18/VDR/0271
REV- 0
ALL DIMENSION ARE IN mm
SCALE: NTS
WT:
SHEET: 01 OF 01

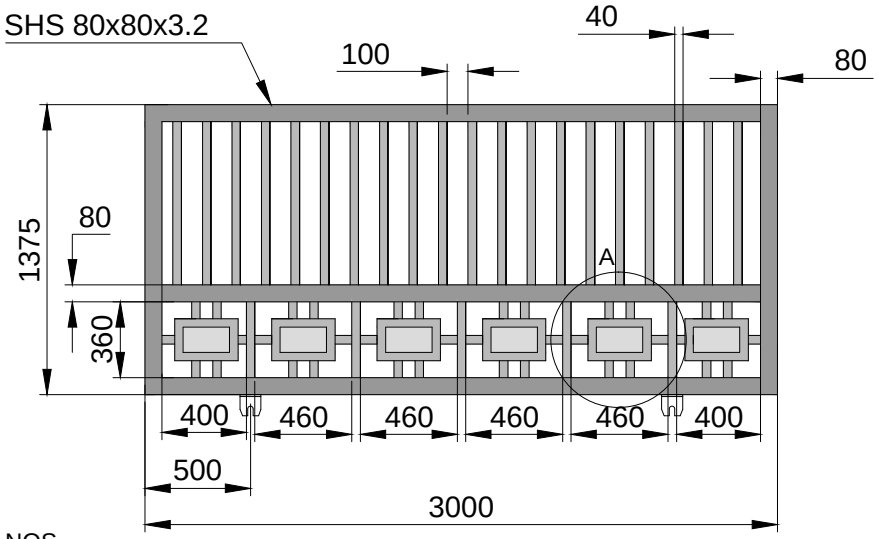


QTY- 4 NOS

LEAF 1

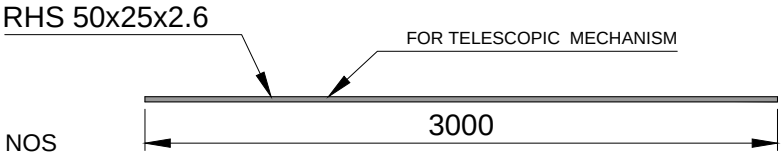


QTY- 4 NOS

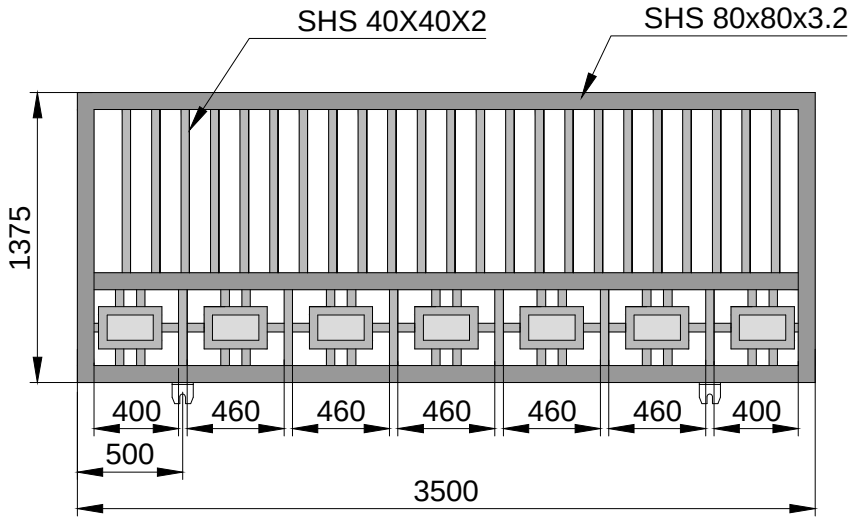


QTY- 2 NOS


LEAF 2

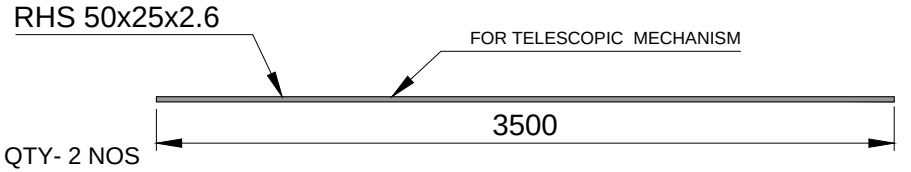

QTY- 2 NOS

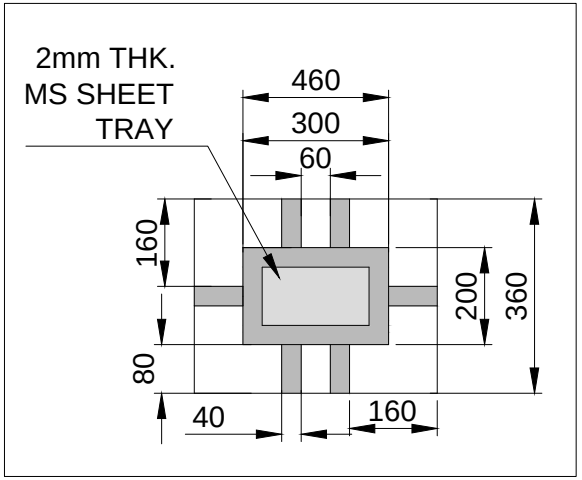


DETAILED VIEW OF A

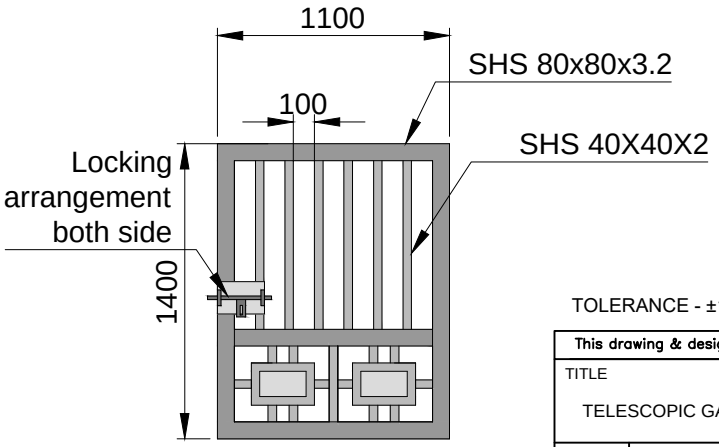

LEAF 3

QTY- 1 NOS

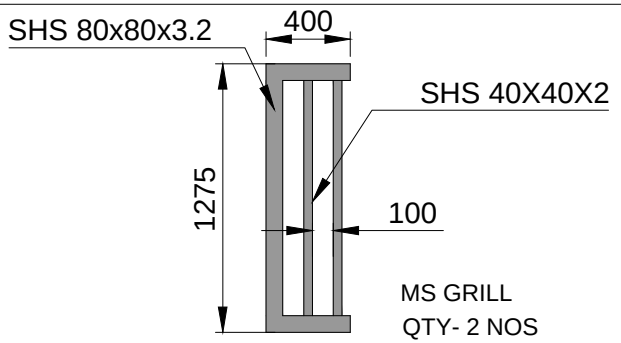


MS GRILL

QTY- 2 NOS

TOLERANCE - ±10mm


This drawing & design is the property of NIHVA TECHNOLOGIES. Not to be sold or copied to any other concern.

TITLE: TELESCOPIC GATE LEAFS			NIHVA TECHNOLOGIES PVT. LTD. PUNE Tel : 020 66304033 Email:- info@nihva.com Website:- www.nihva.com
	NAME	SIGN	DATE
DRAWN	SURAJ		19-03-2018
CHECK	OMKAR		19-03-2018
APPRD.	PRADEEP		19-03-2018
CLIENT -			
PROJECT -			
SITE LOCATION -			
If any queries contact : design@nihva.com	DWG. NO. : NIHVA/17-18/VDR/0272		REV- 0
ALL DIMENSION ARE IN mm	SCALE: NTS	WT:	SHEET: 01 OF 01

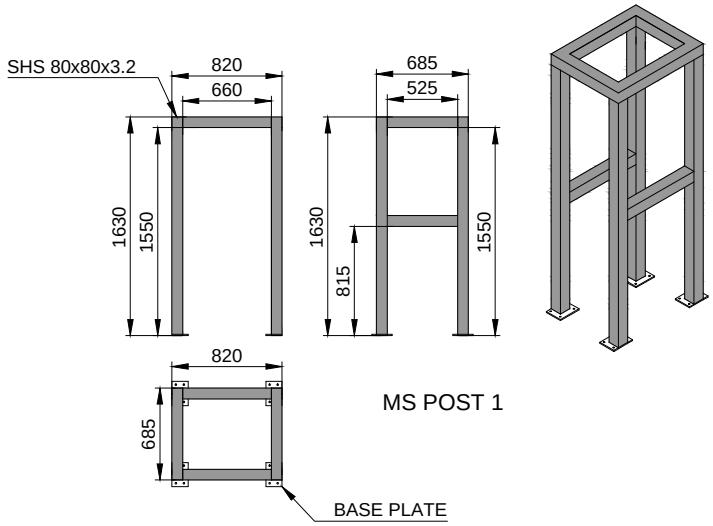


MS POST 1

QTY- 2 NOS

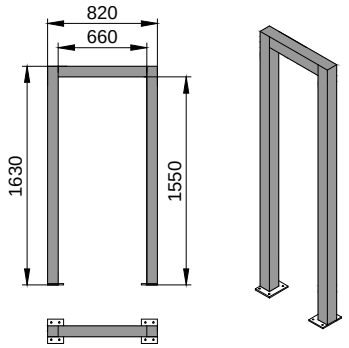


MS POST 2

QTY- 2 NOS

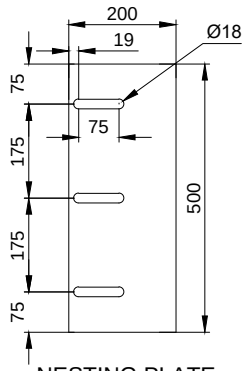


NESTING PLATE

MATERIAL- MILD STEEL
THICKNESS- 10mm
QTY- 6

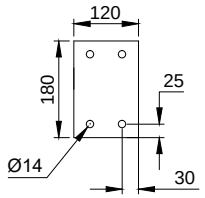


BASE PLATE FOR POST

MATERIAL- MILD STEEL
THICKNESS- 10mm
QTY- 12

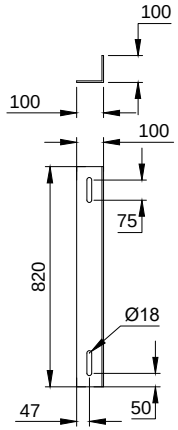


TOP BRACKET

MATERIAL- ISA 100X100X6mm
QTY- 2 NOS

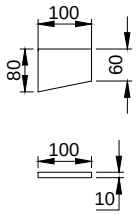

FIXING PLATE 1


MATERIAL- MILD STEEL
THICKNESS- 10mm
QTY- 12

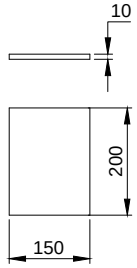

FIXING PLATE 2

MATERIAL- MILD STEEL
THICKNESS- 10mm
QTY- 4

TOLERANCE - ±10mm

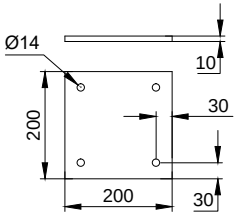

FIXING PLATE 3

MATERIAL- MILD STEEL
THICKNESS- 10mm
QTY- 2

This drawing & design is the property of NIHVA TECHNOLOGIES. Not to be sold or copied to any other concern.

TITLE: POST & BRACKETS			NIHVA TECHNOLOGIES PVT. LTD. PUNE Tel : 020 66304033 Email:- info@nihva.com Website:- www.nihva.com
	NAME	SIGN	DATE
DRAWN	OMKAR		30-03-2018
CHECK	PRADEEP		30-03-2018
APPRD.	PRADEEP		30-03-2018

CLIENT -		
PROJECT -		
SITE LOCATION -		
If any queries contact : design@nihva.com	DWG. NO. : NIHVA/17-18/VDR/0273	REV- 0
ALL DIMENSION ARE IN mm	SCALE: NTS WT:	SHEET: 01 OF 01