
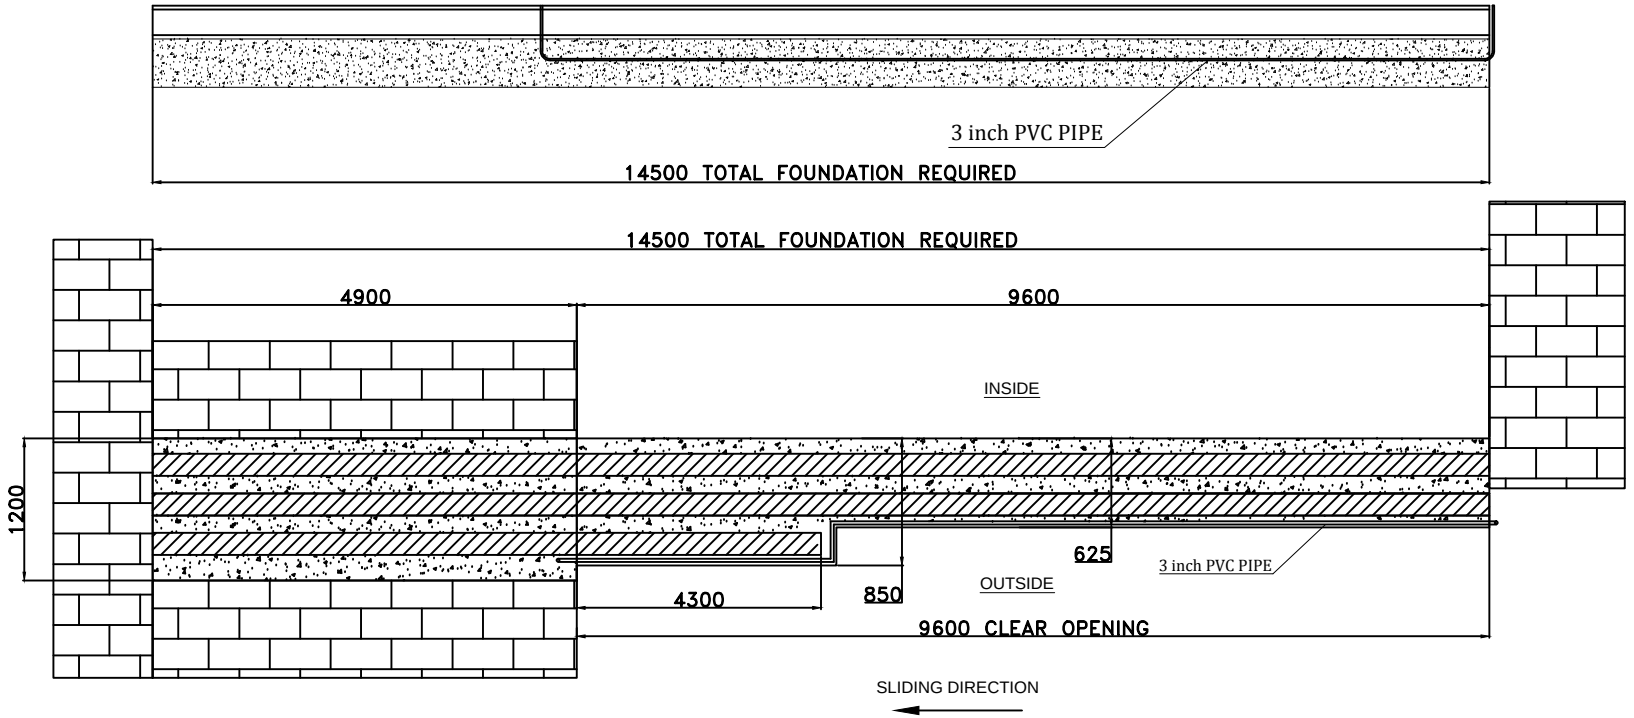


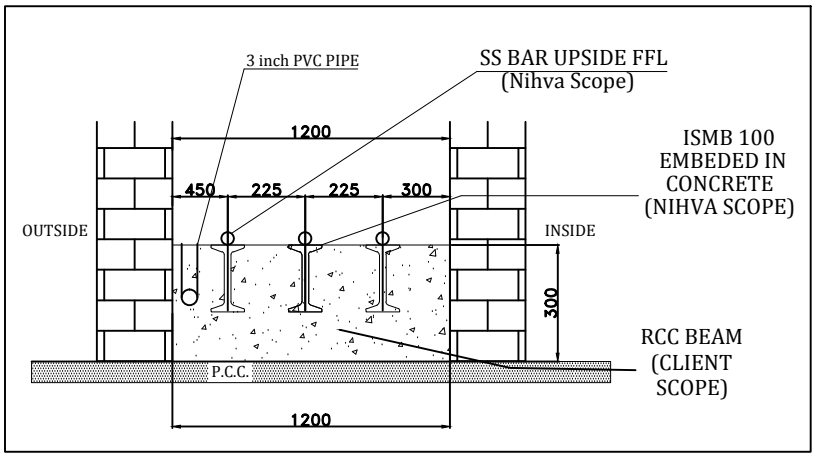

9.6m TELESCOPIC GATE FOUNDATION

This drawing & designing is the property of NIHVA TECHNOLOGIES. Not be sold or copy to any other concern.

TITLE: TELESCOPIC GATE FOUNDATION	ALL DIMENSION ARE IN mm		NIHVA TECHNOLOGIES PVT. LTD.
	SIGN	DATE	
CLIENT APPROVAL	DRAWN: OMKAR	29/06/16	CLIENT - LUPIN
	CHECK: ANIL	29/06/16	PROJECT -
	REV.		SITE -PUNE
	APPRD.		DWG. NO. - NIHVA/16-17/0033
	MFG		SCALE: NTS | WT: | SHEET: 01 OF 01
	Ref. No.		If any queries contact : projects@nihva.com

NIHVA TECHNOLOGY PVT. LTD. PUNE
Tel : 020 66304033
Email:- info@nihva.com
Website:- www.nihva.com