


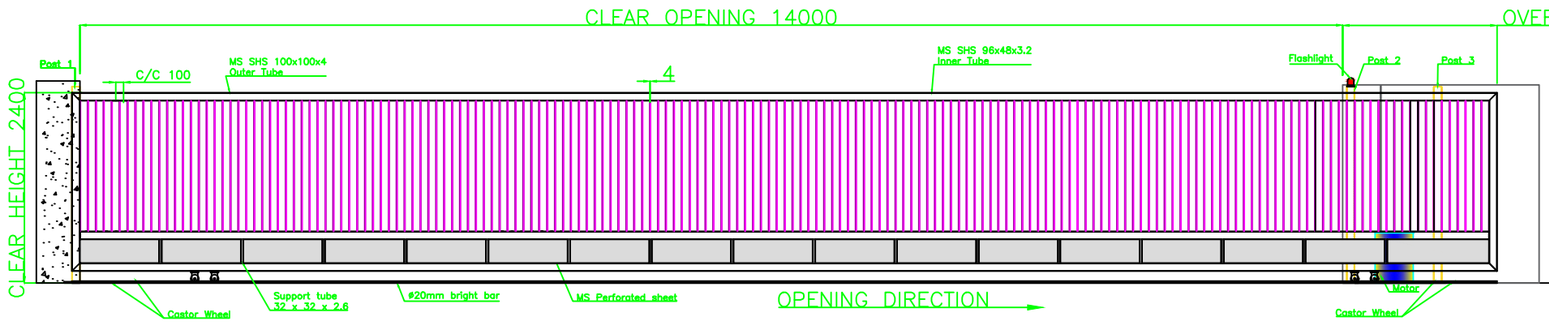


ELEVATION VIEW
(INSIDE)

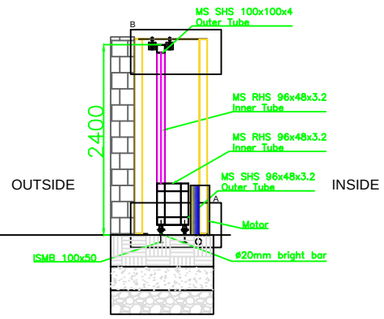


SIDE VIEW

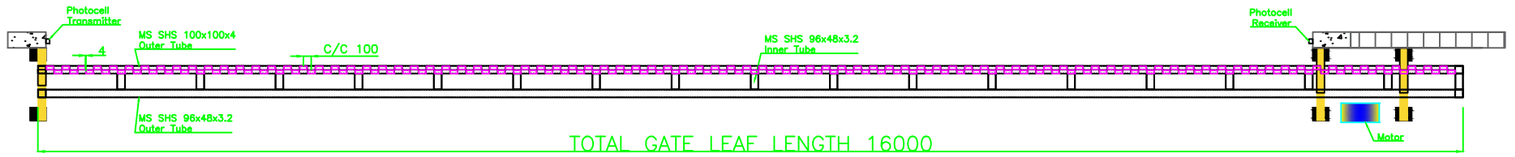

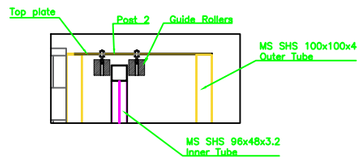

DETAIL B

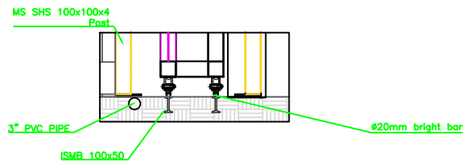

DETAIL A

Technical Specs of Motorized Sliding Gate

1. Opening length - 14000mm
2. Gate Height - 2400mm
3. Parking length required - 16200mm
4. Outer tube size - MS SHS 100x100x4mm
5. Inner tube size - MS RHS 96x48x3mm
6. Bottom Rail - Bright bar Ø20mm
7. Post size - MS SHS 100x100x4mm
8. T`Safety feature - Photocell and flashing light
9. Paint: RAL 7044

Note-

1. All dimension are in mm.
2. All civil work is under client scope.
3. 3" PVC pipe in the foundation to be provided by client.
4. 3PH power required near motor.

Rev 01- (23-02-2022)

1. Tube sizes changed from 100 x 50 to 96 x 48.
2. Tube mounting changed as per client requirement.
3. Distance between the roller increased for cladding.

Rev 02- (24-02-2022)

1. Mentioned the gap between the tube 4mm.
2. Mentioned the C/C distance 100mm.
3. Added RCC details in drawing

Rev 03- (05-03-2022)

1. Added RAL Shade.

Rev 04- (10-03-2022)

1. Clear opening changed 16000mm to 14000mm

This drawing & design is the property of NIHVA TECHNOLOGIES. Not to be sold or copied to any other concern.

TITLE
MOTORIZED SLIDING GATE

	NAME	SIGN	DATE
DRAWN	G.P.		23.02.22
CHECK	A.K.		23.02.22
APPRD.	V.T.		23.02.22

If any queries contact : design@nihva.com

ALL DIMENSION ARE IN mm

NIHVA
NIHVA TECHNOLOGIES PVT. LTD.

NIHVA TECHNOLOGIES PVT. LTD. PUNE
Tel : 020 66304033
Email:- info@nihva.com
Website:- www.nihva.com

CLIENT - SRF
LOCATION - INDORE
PRODUCT - MOTORIZED SLIDING GATE
NIHVA\21-22\CLT\344 | REV- 04
SCALE: NTS | QTY: 1NOS | SHEET: 02 OF 02