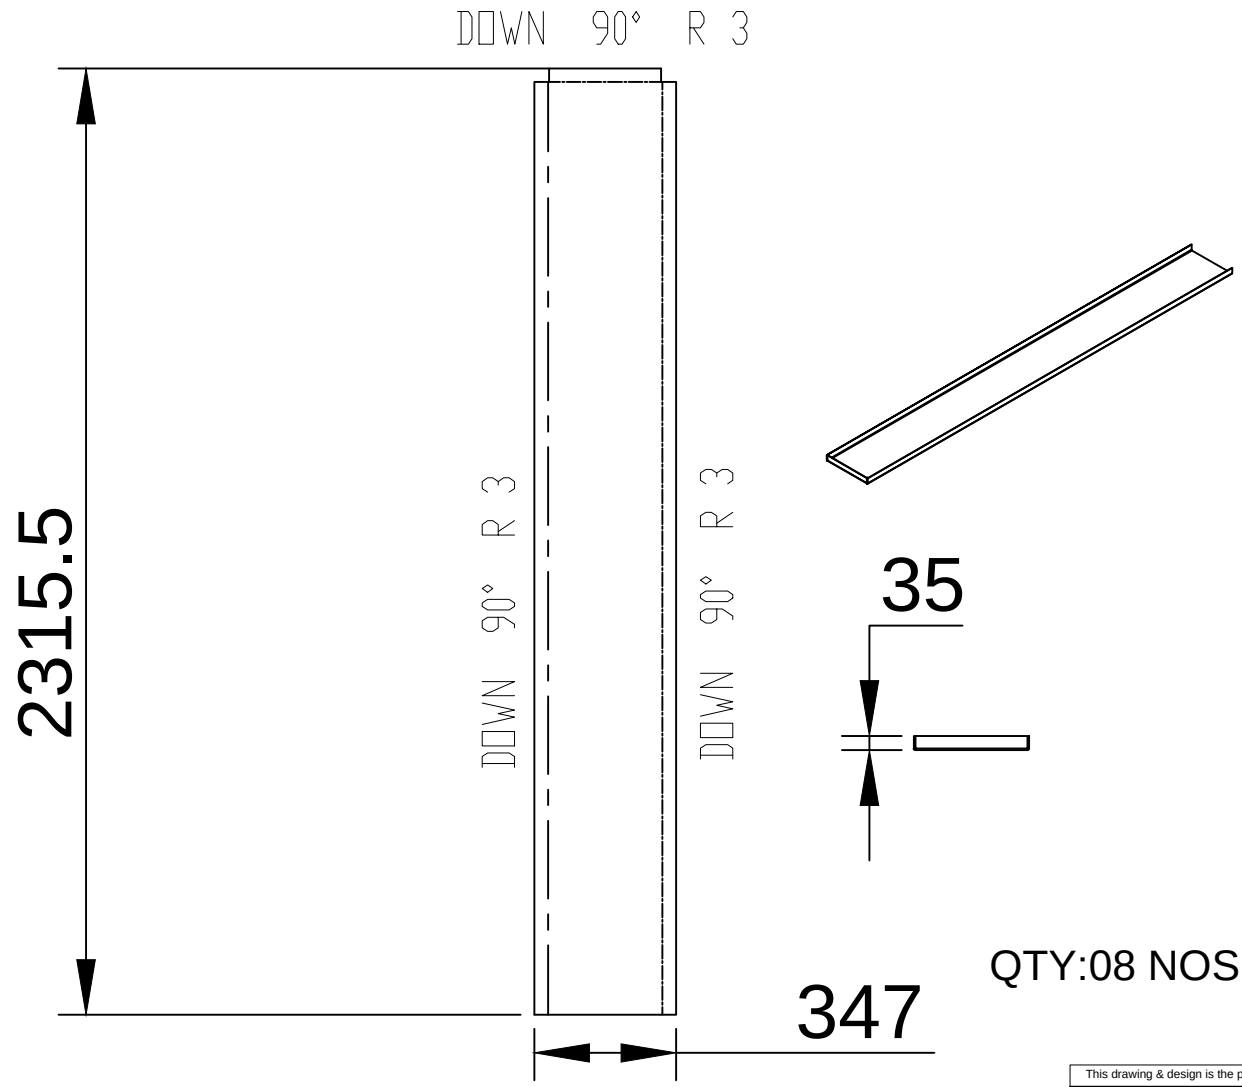

QTY:08 NOS

This drawing & design is the property of NIHVA TECHNOLOGIES. Not to be sold or copied to any other concern.

2 LEAF RIGHT SIDE
CRM DOOR 09

NIHVA TECHNOLOGIES PVT. LTD.

NIHVA TECHNOLOGIES
PVT. LTD. PUNE
Tel : 020 66304033
Email:- info@nihva.com
Website:- www.nihva.com

	NAME	DATE
DRAWN	KISHAN	16/05/2022
CHECK	M.SUTAR	16/05/2022
APPRD.	V.TARAK	16/05/2022

If any queries contact : design@nihva.com

ALL DIMENSION ARE IN mm

CLIENT - NIHVA TECHNOLOGIES PVT LTD
LOCATION -
PRODUCT - SLIDING DOOR
DWG NO:-NIHVA/22-23/CLT/
SCALE: NTS | SCALE:-- 1:1 | SHEET:

Rev No.	Revision	Date	Revised By