
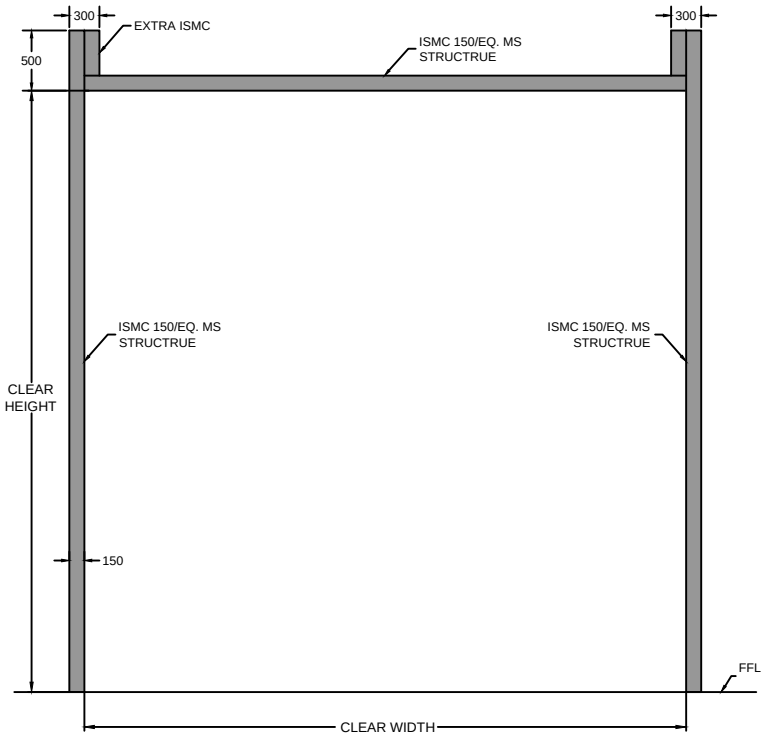


INSIDE ELEVATION

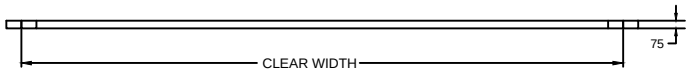

PLAN

TOLERANCE - ±10mm

SR NO.	CLEAR WIDTH	CLEAR HEIGHT	QUANTITY
1	2000 mm	2200 mm	01

This drawing & design is the property of NIHVA TECHNOLOGIES. Not to be sold or copied to any other concern.

TITLE: MS STRUCTURE FOR SECTIONAL DOOR

NIHVA TECHNOLOGIES PVT. LTD.

NIHVA TECHNOLOGIES PVT. LTD. PUNE
Tel : 020 66304033
Email:- info@nihva.com
Website:- www.nihva.com

	NAME	SIGN	DATE
DRAWN	SURAJ		25-06-2018
CHECK	PRADEEP		25-06-2018
APPRD.	PRADEEP		25-06-2018

CLIENT -MASTPRO CONSULTING ENGINEERS PVT. LTD.

PROJECT -MARS INTERNATIONAL PVT. LTD.

SITE LOCATION - PUNE

If any queries contact : design@nihva.com

DWG. NO. : NIHVA/18-19/0066 REV- 0

ALL DIMENSION ARE IN mm

SCALE: NTS WT: SHEET: 01 OF 01