
SR.NO	DESCRIPTION	QTY
1	CHEQ.SHEET 400 X 5 X 1800L	1 NO
2	FLAT 25 X 5 X 1800L	2 NOS
3	FLAT 25 X 5 X 300L	6 NOS

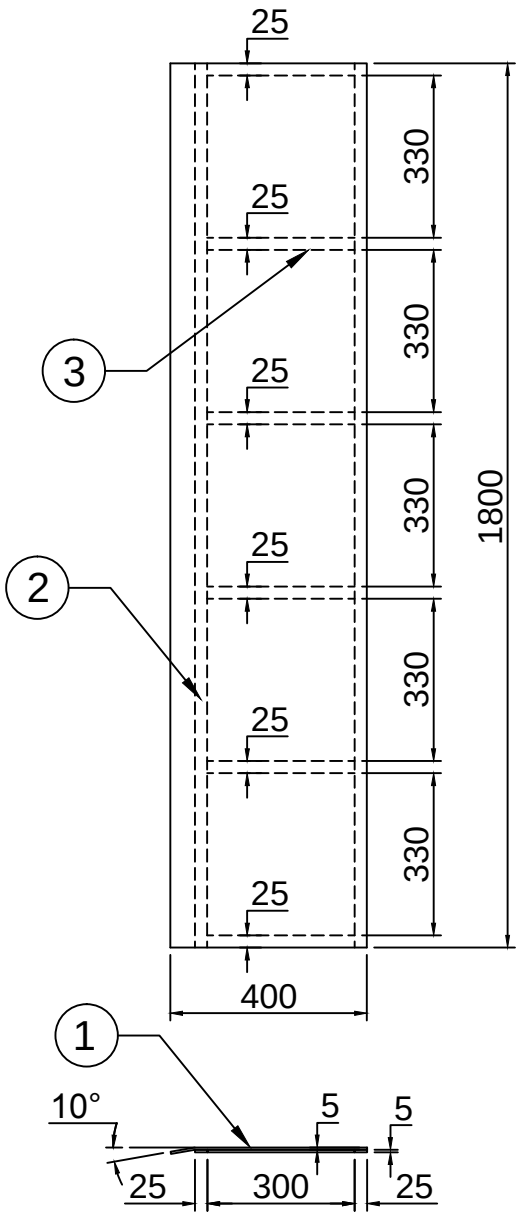

This drawing & design is the property of NIHVA TECHNOLOGIES. Not to be sold or copied to any other concern.

TITLE : -

LIP PLATE ASSLY

NIHVA TECHNOLOGIES PVT. LTD.

NIHVA TECHNOLOGIES PVT. LTD. PUNE
Tel : 020 66304033
Email:- info@nihva.com
Website:- www.nihva.com

	SIGN	DATE
DRAWN	P.A	03.05.2019
CHECK		
REV.		
APPROVAL		

CLIENT -

PROJECT -

SITE -

DWG. NO. : NIHVA/19-20/VDR/034

If any queries contact : projects@nihva.com

SCALE: NTS | WT: | SHEET: 01 OF 01

ALL DIMENSION ARE IN mm