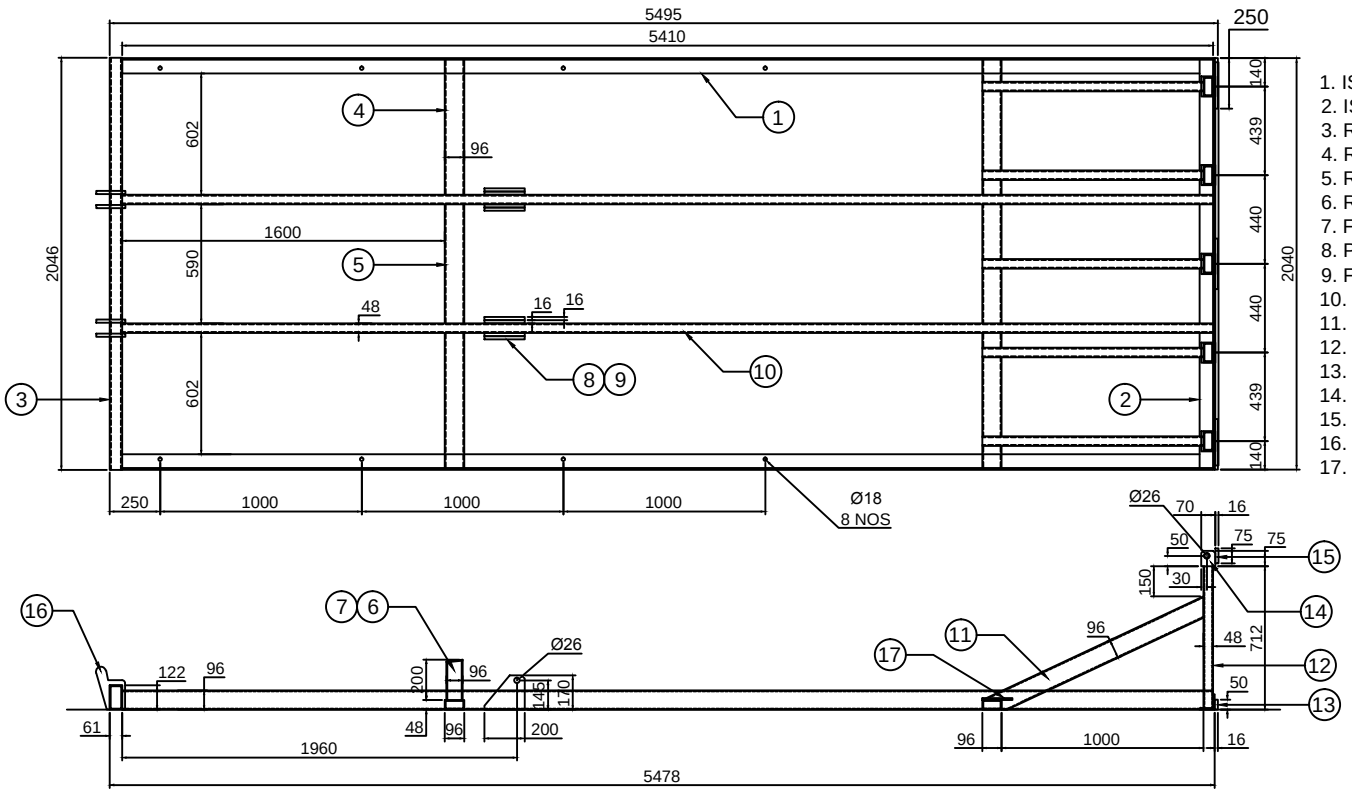


1. ISA 75 X 8 X 5410L = 2 NOS
2. ISA 75 X 8 X 2040L = 1 NO
3. R.TUBE 122 X 61 X 4.8 THK X 2046L = 1 NO
4. R.TUBE 96 X 48 X 4.8 THK X 668L = 4 NOS
5. R.TUBE 96 X 48 X 4.8 THK X 590L = 2 NOS
6. R.TUBE 96 X 48 X 4.8 THK X 195L = 2 NOS
7. FLAT 50 X 5 X 100L = 2 NOS
8. PROFILE 170 X 16 X 200L = 4 NOS
9. FLAT 75 X 16 X 200L = 4 NOS
10. R.TUBE 96 X 48 X 4.8 THK X 5410L = 2 NOS
11. R.TUBE 96 X 48 X 4.8 THK X 1210L = 5 NOS
12. R.TUBE 96 X 48 X 4.8 THK X 704L = 5 NOS
13. FLAT 50 X 16 X 250L = 3 NOS
14. FLAT 75 X 70 X 100L = 5 NOS
15. FLAT 75 X 16 X 2000L = 1 NO
16. PROFILE 16 MM THK = 4 NOS
17. FLAT 50 X 10 X 150L = 1 NO

TOLERANCE :- ± 10mm

This drawing & design is the property of NIHVA TECHNOLOGIES. Not to be sold or copied to any other concern.

TITLE	BASE FRAME ASSLY		
	NAME	SIGN	DATE
DRAWN	P.A		08.08.2020
CHECK	G.J		08.08.2020
APPRD.			

NIHVA TECHNOLOGIES PVT. LTD.
Website:- www.nihva.com
NIHVA TECHNOLOGIES PVT. LTD. PUNE
Tel : 020 66304033
Email:- info@nihva.com

CLIENT -

PROJECT -

SITE LOCATION -

If any queries contact : design@nihva.com

DWG. NO. : NIHVA/20-21/VDR/0029 | REV- R00

ALL DIMENSION ARE IN mm

SCALE: NTS | WT: | SHEET: 01 OF 01