

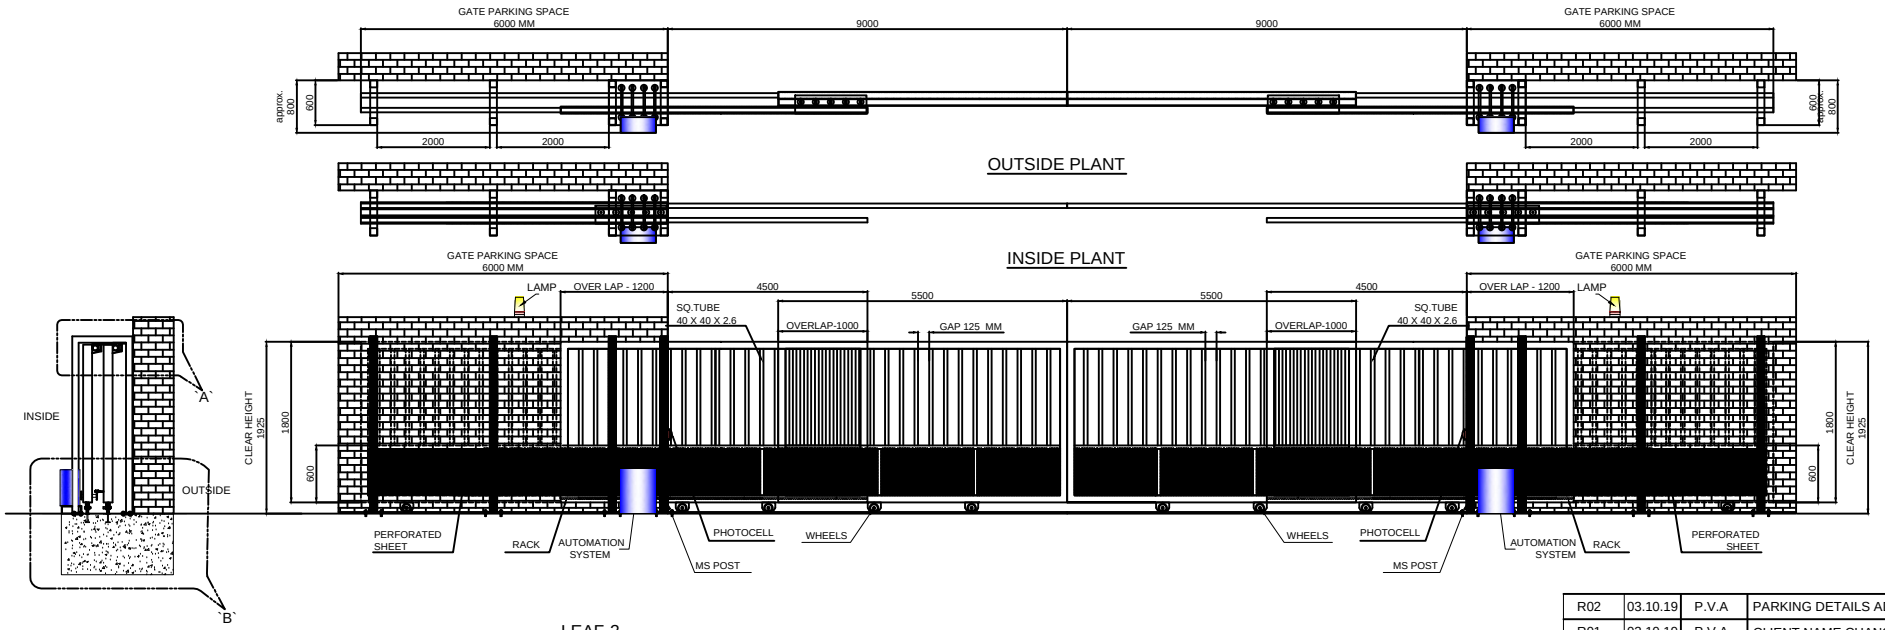


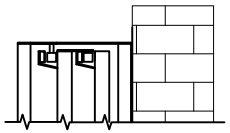

DETAIL -`A`

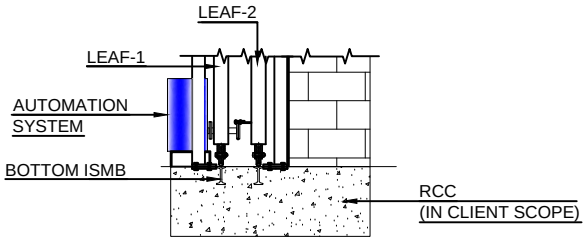

DETAIL- `B`

SR NO	DATE	DRAWN	REMARK
R02	03.10.19	P.V.A	PARKING DETAILS ADD
R01	03.10.19	P.V.A	CLIENT NAME CHANGE

This drawing & designing is the property of NIHVA TECHNOLOGIES. Not be sold or copy to any other concern.

TITLE
2 LEAF TELESCOPIC
BI-PARTING SLIDING GATE

	NAME	SIGN	DATE
DRAWN	P.V.A		26.09.2019
CHECK	G.J		26.09.2019
APPROVAL			

NIHVA TECHNOLOGY
PVT. LTD. PUNE
Tel : 020 66304033
Email:- info@nihva.com
Website:- www.nihva.com

CLIENT - ASHOK CONSTRUTION
PROJECT - JOHN DEERE
SITE LOCATION - RANJANGAON
DWG. NO. : NIHVA/19-20/0104/R02 | REV: R02
If any queries contact : projects@nihva.com | SCALE: 01 | WT: | SHEET: 01 OF 01
ALL DIMENSION ARE IN mm