
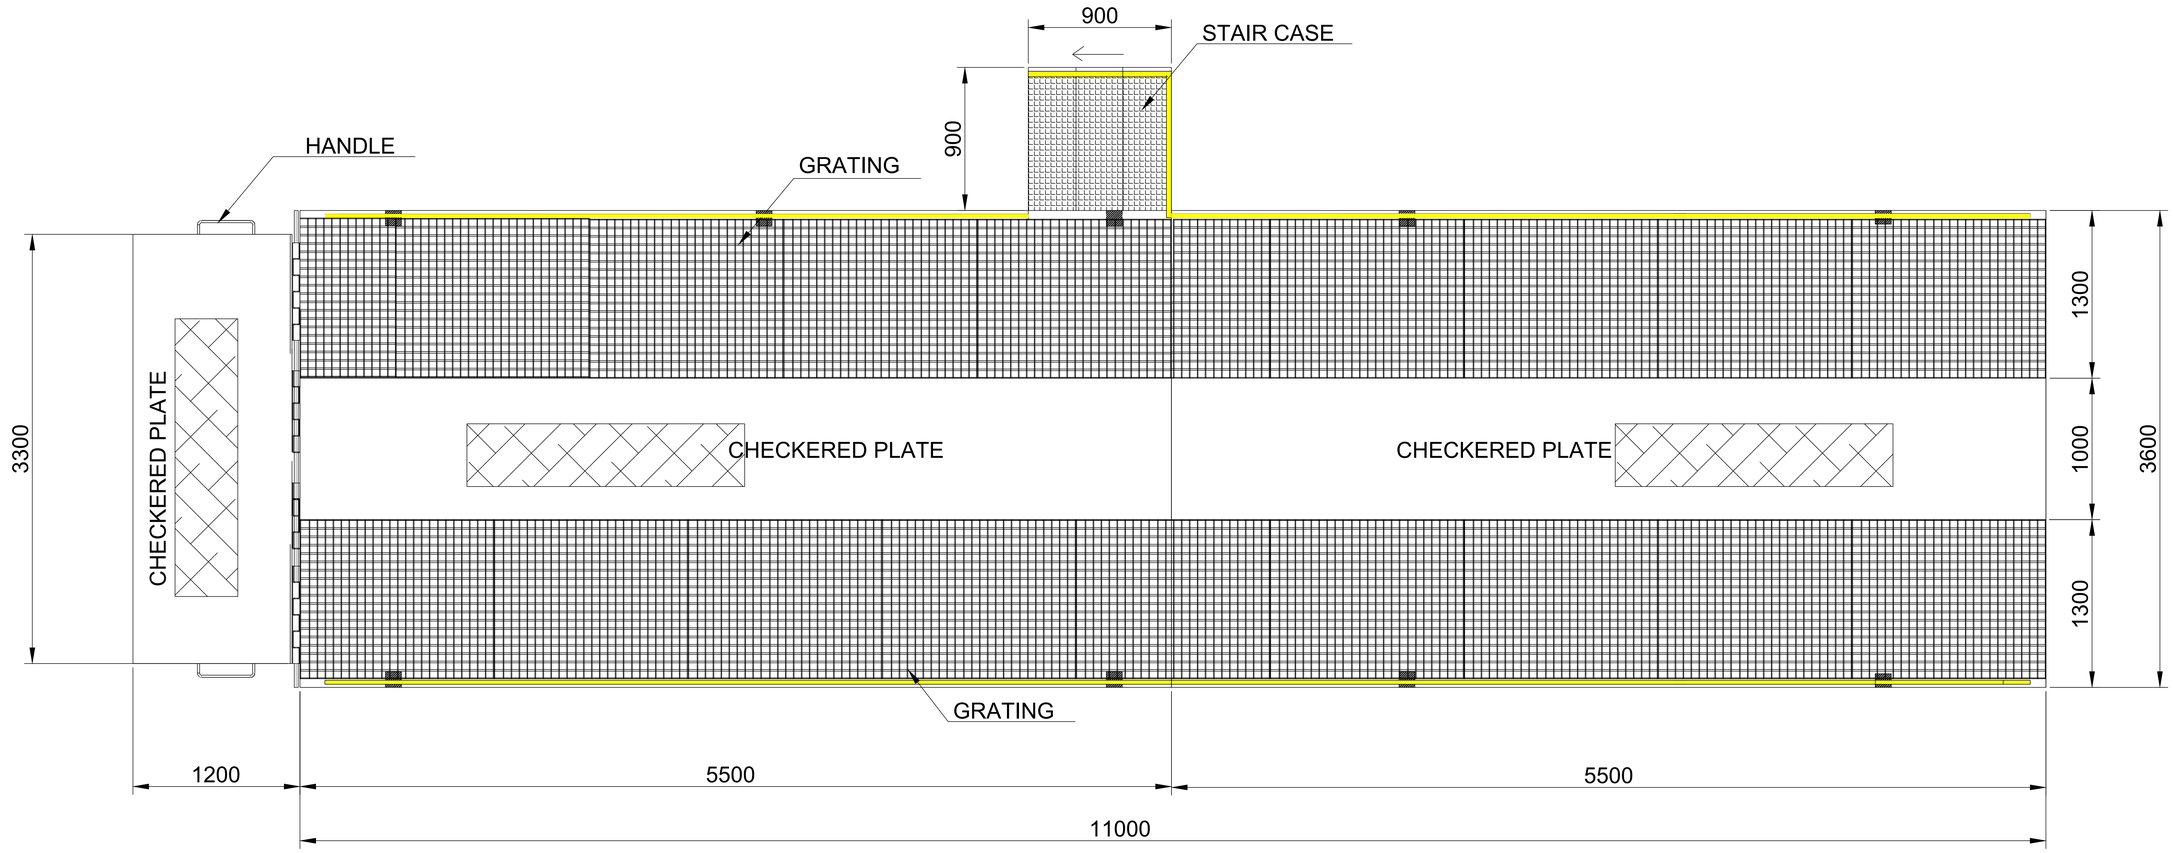


BOTH SIDE RAILING

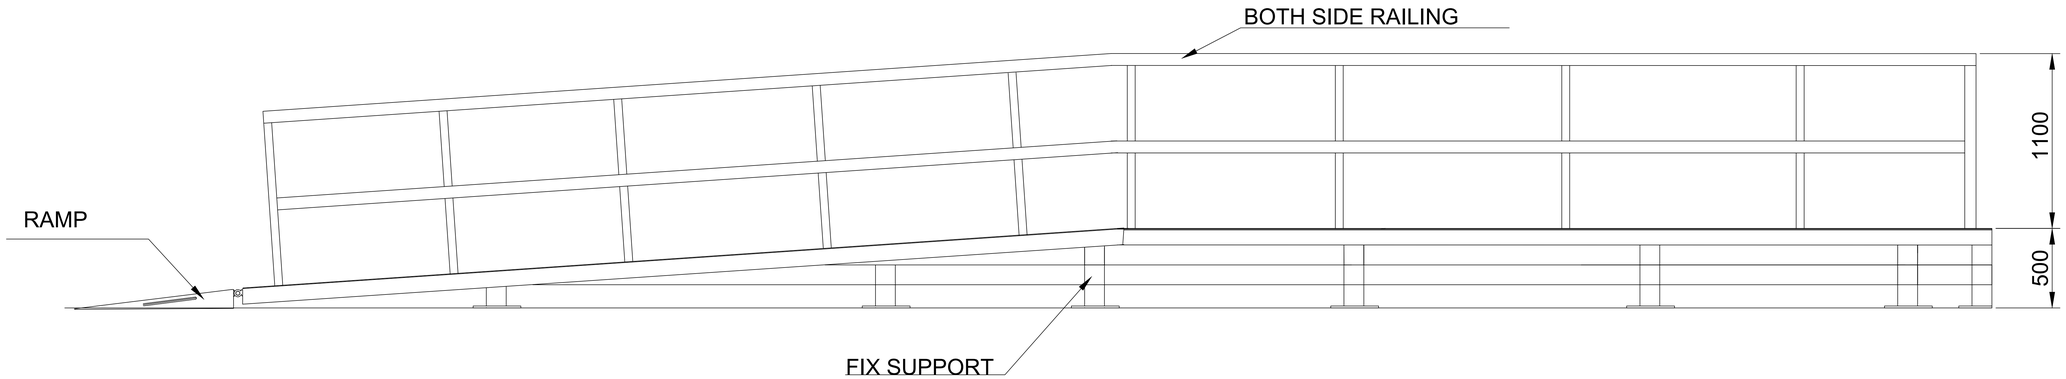

NOTE:-

1. ALL DIMENSIONS ARE IN MM
2. THES DRAWING IS FOR UNDERSTANDING PURPOSE

SR.NO	WIDTH (W)	LENGTH (L)	PLATFORM HEIGHT	RAILING HEIGHT	CAPACITY
1	3600	11000	500	1100	10 Ton

SR.NO	DESCRIPTION	REV.DATE	REV.NO
01	Platform slope width 3600mm to 3000mm	18.10.2024	R01
02	Stair Case position change & height adjustable to fix height	18.10.2024	R01
03	Platform slope width 3000 mm to 3600 mm	25.10.2024	R02

This drawing & design is the property of NIHVA TECHNOLOGIES. Not to be sold or copied to any other concern.

TITLE:- FIX DOCK RAMP

	NAME	DATE	SIGN
DRAWN	S.J.	30.08.24	
CHECK	S.W.	30.08.24	
APPRD.	V.T.	30.08.24	

If any queries contact : design2@nihva.com

ALL DIMENSION ARE IN mm

NIHVA TECHNOLOGIES PVT. LTD.

NIHVA TECHNOLOGIES PVT. LTD. PUNE
Tel : 020 66304033
Email:- info@nihva.com
Website:- www.nihva.com

CLIENT - FERRERO INDIA PVT LTD

LOCATION - BARAMATI

PRODUCT - FIX DOCK RAMP

DWG NO:-NIHVA/24-25/00XX | REV- 02

SCALE: NTS | SCALE:-- 1:1 | SHEET: 01 OF 01