



TOP VIEW

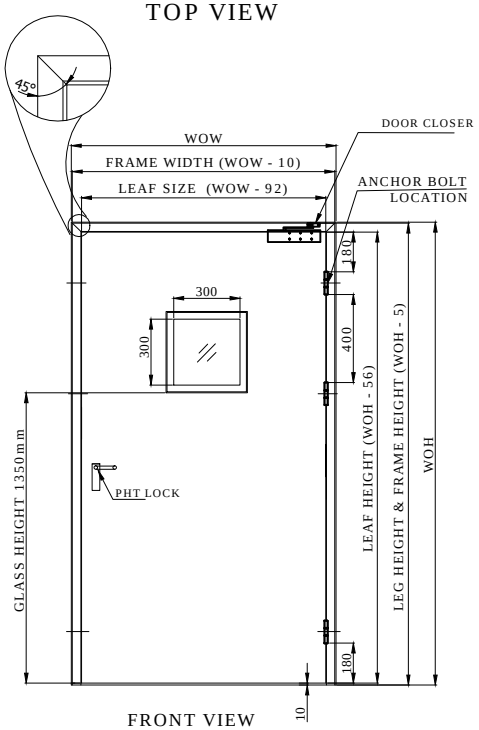


FRONT VIEW

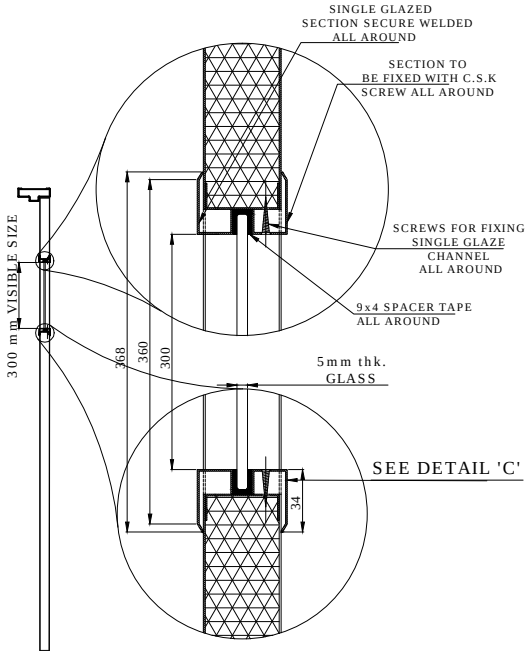

SIDE VIEW SECTION A-A'


SINGLE GLAZE FIXING DETAIL

NOTE :
1. DOOR HINGES : GEZE MAKE.
2. DOOR CLOSER : GEZE MAKE.
3. DOOR EXTERNAL TRIM : YELE MAKE.

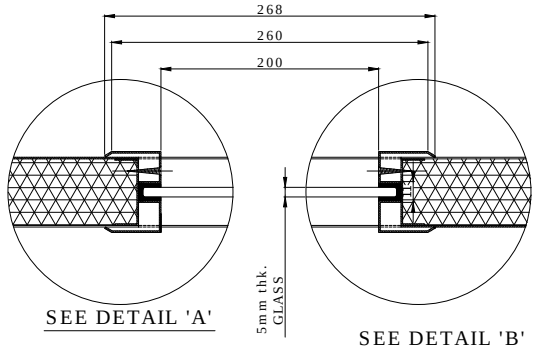



SEE DETAIL 'A'

SEE DETAIL 'B'

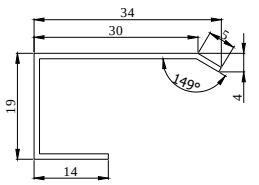


SEE DETAIL 'C'

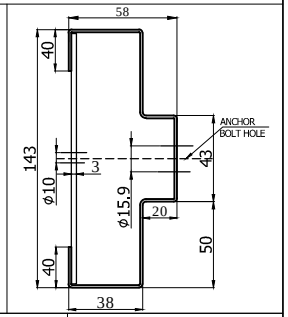

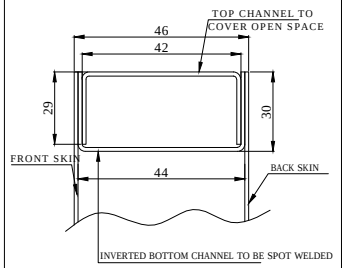

DOOR TOP SECTION DETAIL

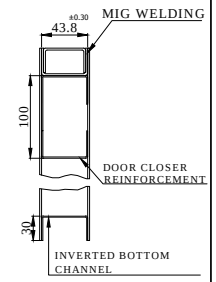

DOOR BOTTOM & TOP DETAIL

TOLERANCE - ±05mm

SR. NO	WALL OPENING WIDTH	WALL OPENING HEIGHT	QTY	RAL	LOCATION	HARDWARE
06	900	2375	01	9002	Block G - Security cabin - white colour	Single leaf metal door with Vision Panel, Hinges , Door closer ,with external trim
05	900	2380	01	9002	Block G - Security cabin - white colour	Single leaf metal door with Vision Panel, Hinges , Door closer ,with external trim
04	1200	2100	01	9002	Block B - Metering Kiosk (GD6B)	Hinges , Door closer , Non-Fire rated Glass 300X300mm
03	1200	2100	01	9002	Block D - Metering Kiosk (GD6B)	Hinges , Door closer , Non-Fire rated Glass 300X300mm
02	1200	2100	01	9002	Block C - Metering Kiosk (GD6B)	Hinges , Door closer , Non-Fire rated Glass 300X300mm
01	1200	2100	01	9002	RMU 2 (GD6B)	Hinges , Door closer , Non-Fire rated Glass 300X300mm

This drawing & design is the property of NIHVA TECHNOLOGIES. Not to be sold or copied to any other concern.

TITLE: SINGLE LEAF STEEL DOOR

	NAME	SIGN	DATE
DRAWN	P.V.A		21.03.2019
CHECK	V.M.T		21.03.2019
APPRD.			

If any queries contact : design@nihva.com

ALL DIMENSION ARE IN mm

NIHVA TECHNOLOGIES PVT. LTD.
NIHVA TECHNOLOGIES PVT. LTD. PUNE
Tel : 020 66304033
Email:- info@nihva.com
Website:- www.nihva.com

CLIENT - SYNERGY

PROJECT - EMBASSY

SITE LOCATION - CHAKAN, PUNE.

DWG. NO. : NIHVA/18-19/0296 | REV- R00

SCALE: NTS | WT: | SHEET: 01 OF 01