
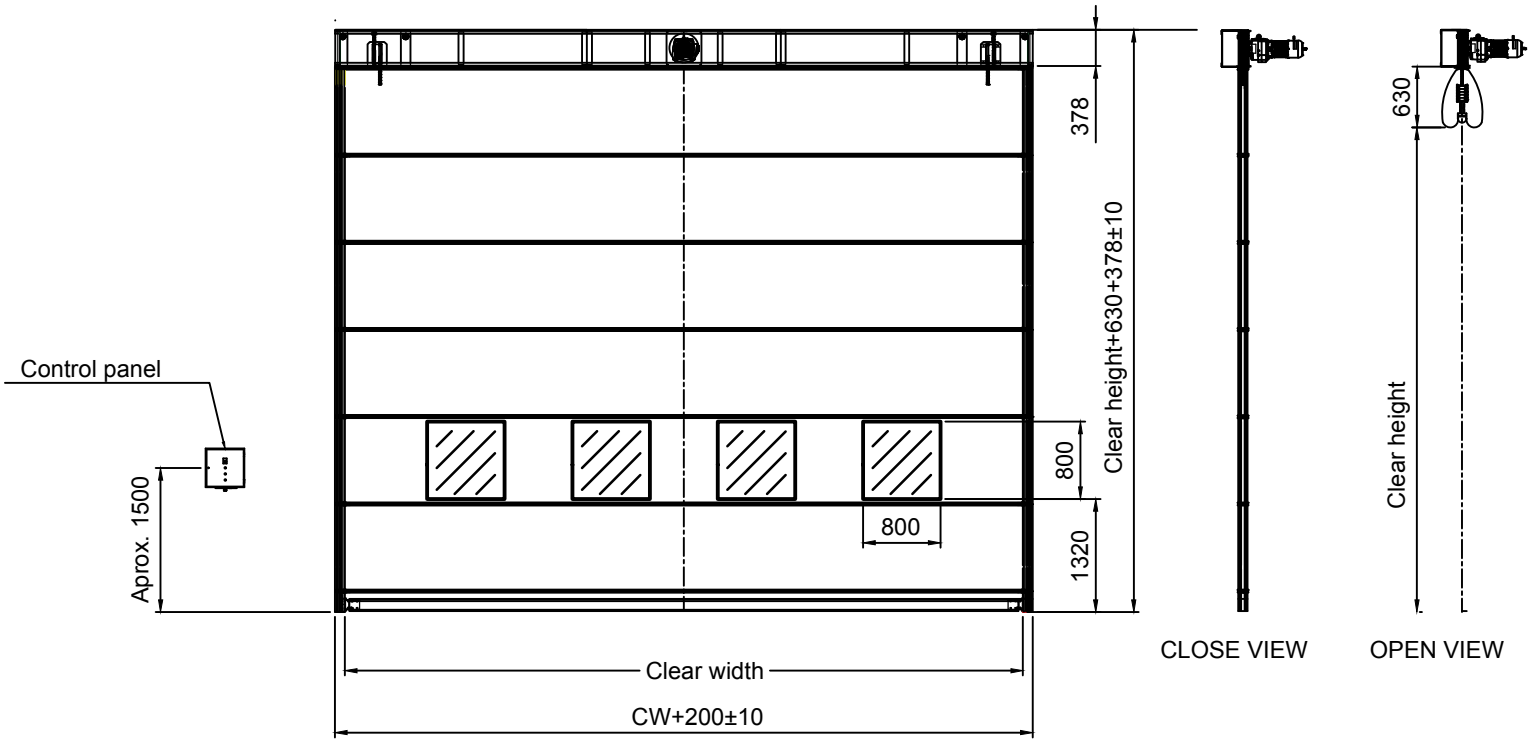



Door properties

1. The door designed to withstand a differencial pressure of1.15 kpa x 1.5 Fos
2. side profile- Aluminium
3. Fabric Colour-
   option 1- RAL 5013
   option 2- RAL 6002
   option 2- RAL 6026


Electrical-

1. One main control panel with plc control type.
2. Audible and visible alarm
3. Safety edge
4. Power -2.2 kw

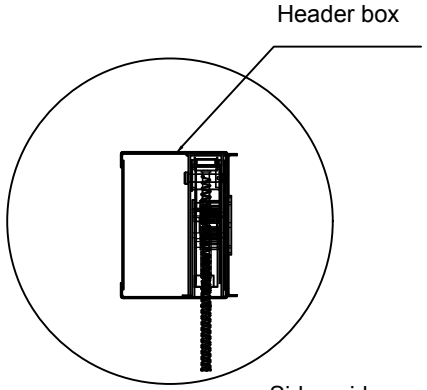


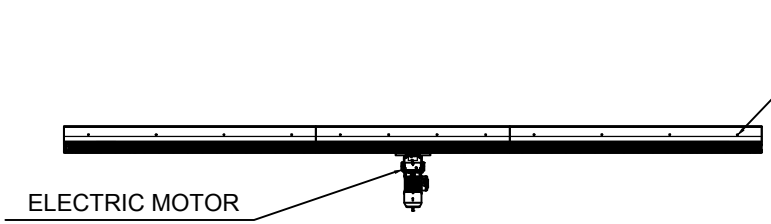


SR NO	DOOR NAME	SIZE CW X CH	QTY
1	ACL GATE 01	7000 X 5000	1
2	CRM DOOR 02	7000 X 5500	1

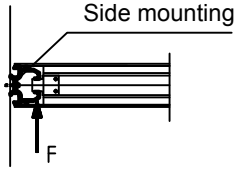

FOR GUIDE MONTING

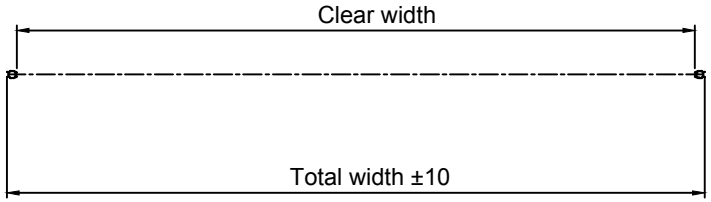

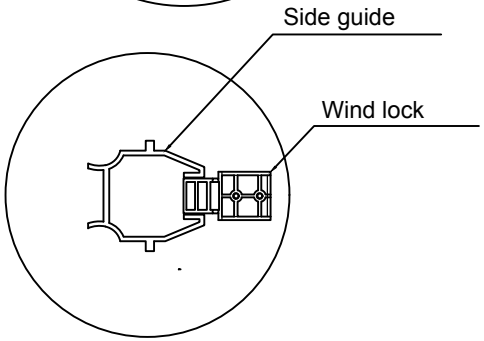

TITLE:- VERTICAL FABRIC DOOR				NIHVA TECHNOLOGIES PVT. LTD. PUNE Tel : 020 66304033 Email:- info@nihva.com Website:- www.nihva.com	
	NAME	DATE	SIGN		
DRAWN	KISHAN	19/05/2022		CLIENT - POSCO STEEL	
CHECK	P. JAIN	19/05/2022		LOCATION - MANGAON	
APPRD.	V. TARAK	19/05/2022		PRODUCT - VERTICAL FABRIC DOOR	
If any queries contact : design@nihva.com				DWG NO:-NIHVA/22-23/CLT/0043	REV- 0
ALL DIMENSION ARE IN mm				SCALE: NTS	SCALE:-- 1:1 | SHEET: 01 OF 01

Date	Revised By