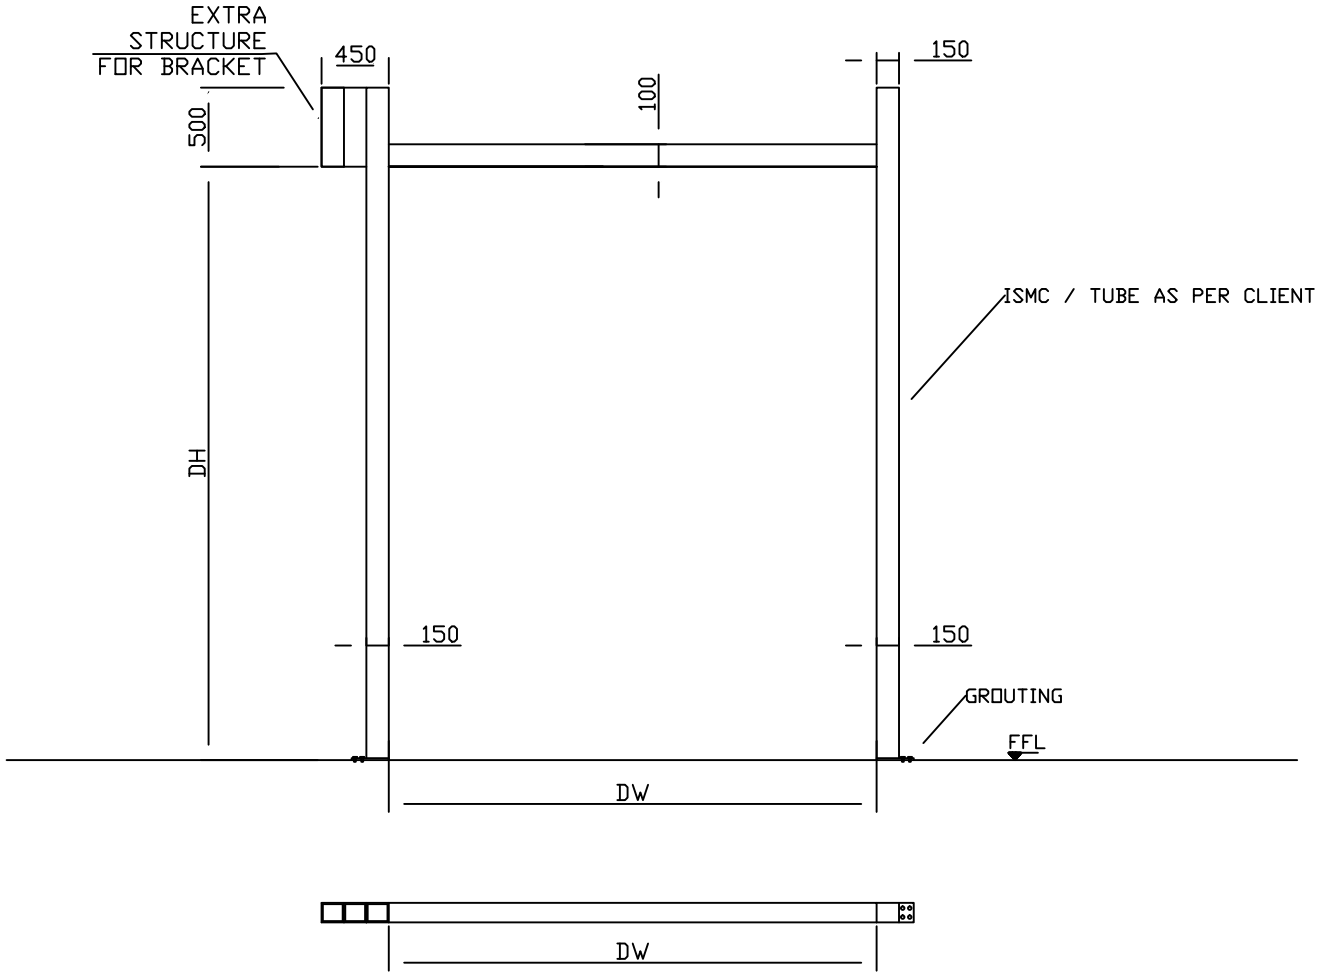


1	3000	4000	1
SR NO	DW	DH	QUANTITY
DOOR DIMENSION			

Tolerance ±3 mm (for all dimensions)

Dimensions in [ ] ==> clearance for installation

This drawing & design is the property of NIHVA TECHNOLOGIES. Not to be sold or copied to any other concern.

NOTE-
1. ALL CIVIL WORK WILL BE CLIENT'S SCOPE.
2. STRUCTURE REQUIRED FOR HIGH SPEED DOOR IS IN CLIENT'S SCOPE.
3. HIGH SPEED DOOR WILL BE ONLY INSTALLED AFTER STRUCTURE READINESS AS PER DRAWING PROVIDED.

TITLE - RR300 PLUS ALU HSD STRUCTURE

NIHVA TECHNOLOGIES PVT. LTD.
NIHVA TECHNOLOGIES PVT. LTD. PUNE
Tel : 020 66304033
Email:- info@nihva.com
Website:- www.nihva.com

	NAME	SIGN	DATE
DRAWN	S.M.S.		29.10.2020
CHECK	P.V.A.		29.10.2020
APPROVED			

CLIENT - HUHTAMAKI PPL LTD

PROJECT - HUHTAMAKI PPL LTD

LOCATION - KHOPOLI

If any queries contact:sales@nihva.com

DWG. NO. - NIHVA/20-21/0072 REV- 0

ALL DIMENSION ARE IN mm

SCALE: NTS WT: SHEET: