
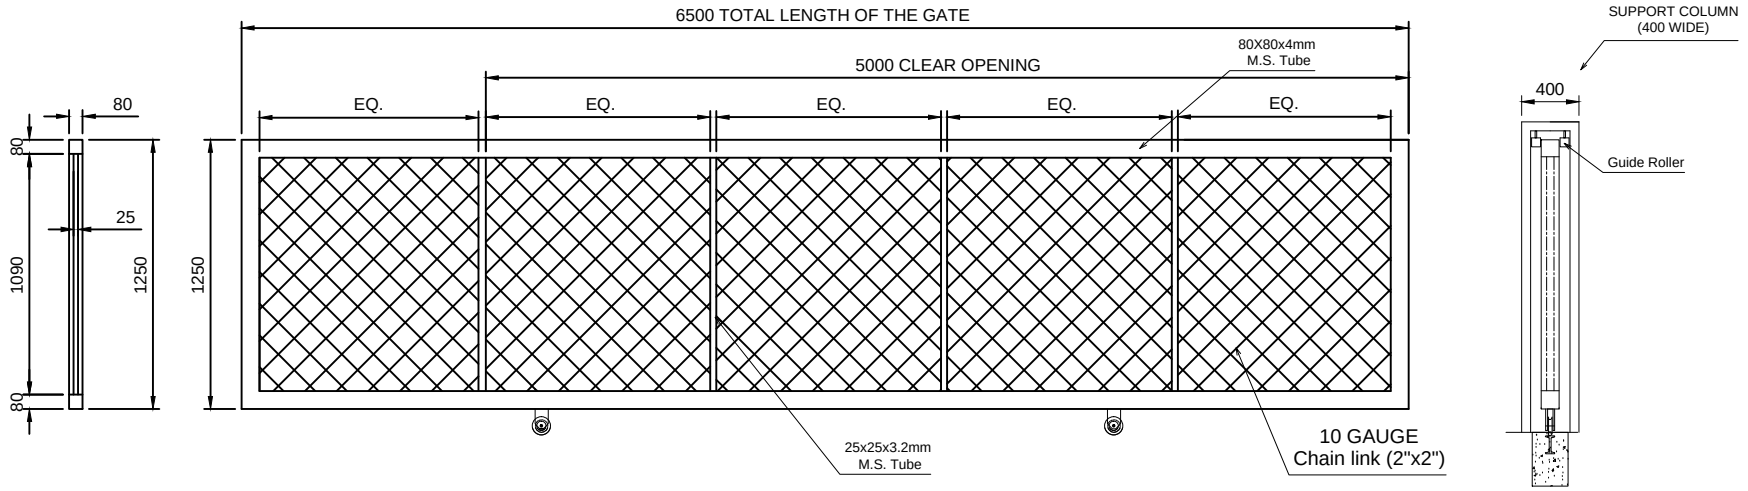



SLIDING DIRECTION

SIDE VIEW

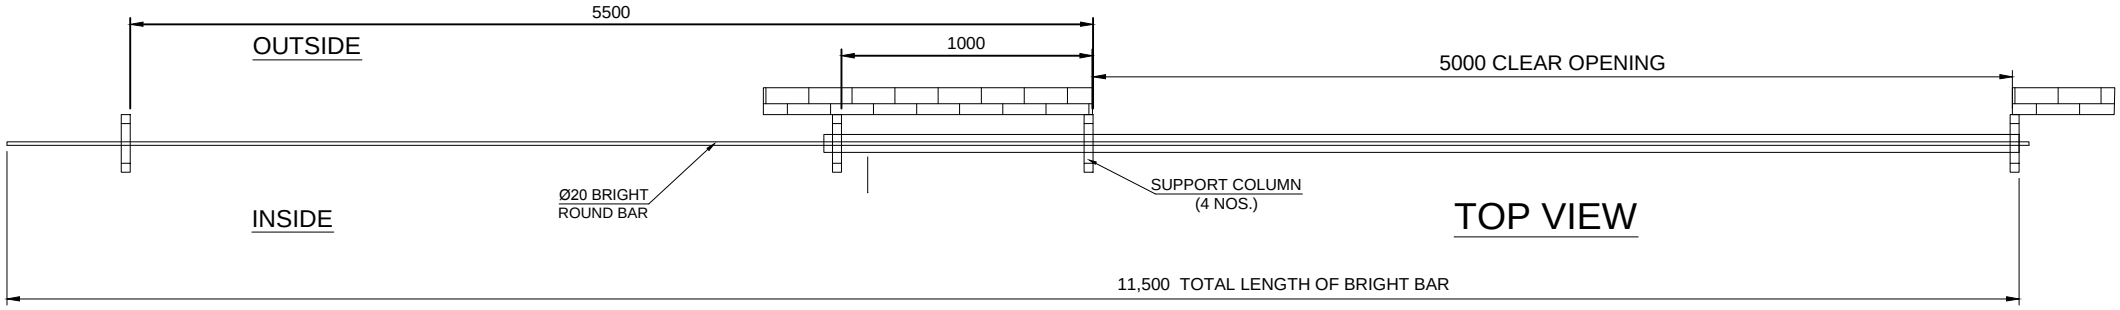


| | |
|---|---|
| Clear Opening size | - 5000X1350mm |
| Total length of gate | - 6500X1350mm |
| No. Of Column | - 4 nos. |

This drawing & designing is the property of NIHVA TECHNOLOGIES. Not be sold or copy to any other concern.

TITLE: FENCED SLIDING GATE

| | SIGN | DATE |
|---|---|---|
| DRAWN | SUBODH | 07/01/16 |
| CHECK | | |
| REV. | 00 | |
| APPROVAL | | |

NIHVA TECHNOLOGIES PVT. LTD.

NIHVA TECHNOLOGY PVT. LTD. PUNE
Tel : 020 66304033
Email:- info@nihva.com
Website:- www.nihva.com

CLIENT - REWARD CONSTRUCTION

PROJECT - GIVAUDAN

SITE - RANJANGAON MIDC

If any queries contact : projects@nihva.com

SCALE: -- | WT: | SHEET: 01 OF 01

ALL DIMENSION ARE IN mm