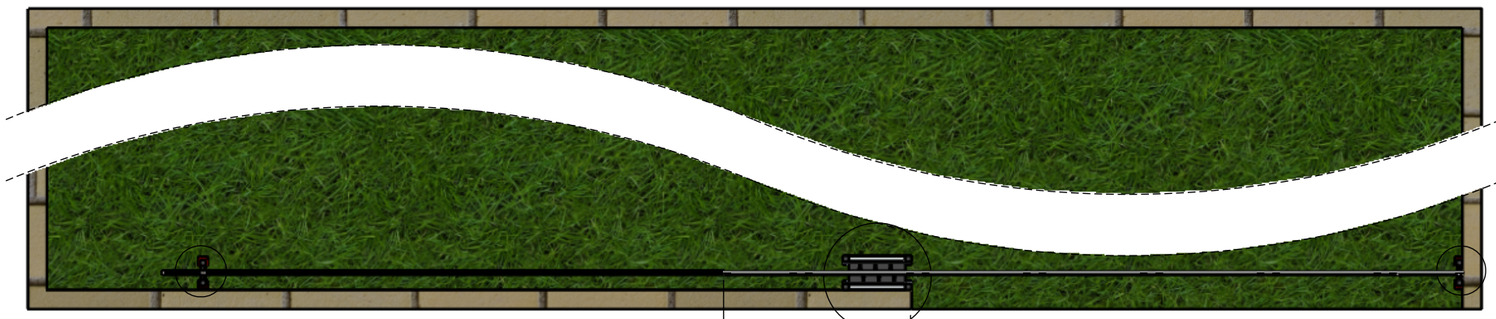


2440.00
OVERLLAPING DISTANCE

B

A

C

DETAIL C
SCALE 1 : 40

SQ MS TUBE
40*40*4MM THK

SLIDING DIRECTION


9640.00
TOTAL LEAF LENGTH



900.00


2440.00
LEAF HEIGHT

7200.00
CLEAR
OPENING

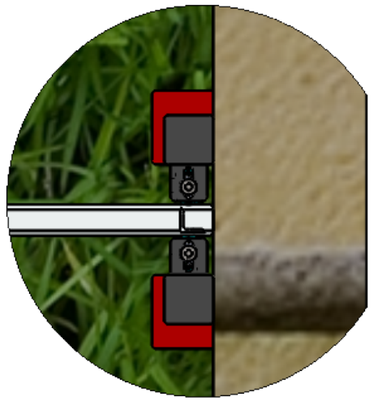

DETAIL A
SCALE 1 : 10


POST 1 AND NYLON
BEARING ASM

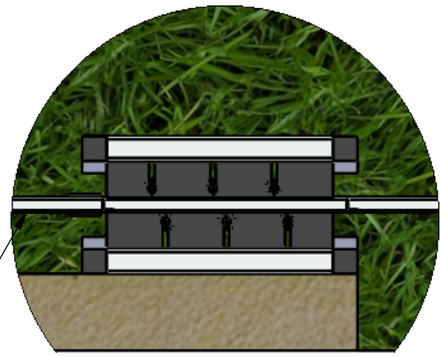

RECT MS TUBE
100*50*5MM THK

DETAIL B
SCALE 1 : 20

POST 2 AND NYLON
BEARING ASM

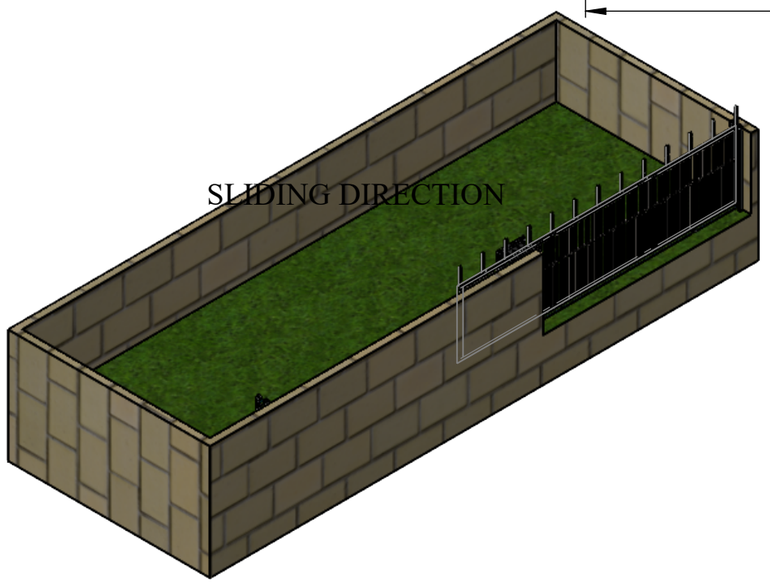

SLIDING DIRECTION

TITLE - GATE				NIHVA TECHNOLOGIES PVT.LTD.PUNE
DWG NO - NTPL-000-PM-001-00-00-00				Website - www.nihva.com
	NAME	SIGNATURE	DATE	PROJECT NO - NTPL-000-PM
DRAWN	V.W		02-05-2025	PRODUCT - SINGLE SLIDING GATE
CHK'D	S.W.		02-05-2025	SITE LOCATION - GUJARAT
APPV'D	V.T.		02-05-2025	
if any queries contact - supportautomation@nihva.com				REVISION - QTY - 1
ALL DIMENSION ARE IN mm		A3		SCALE SHEET 1 OF 1