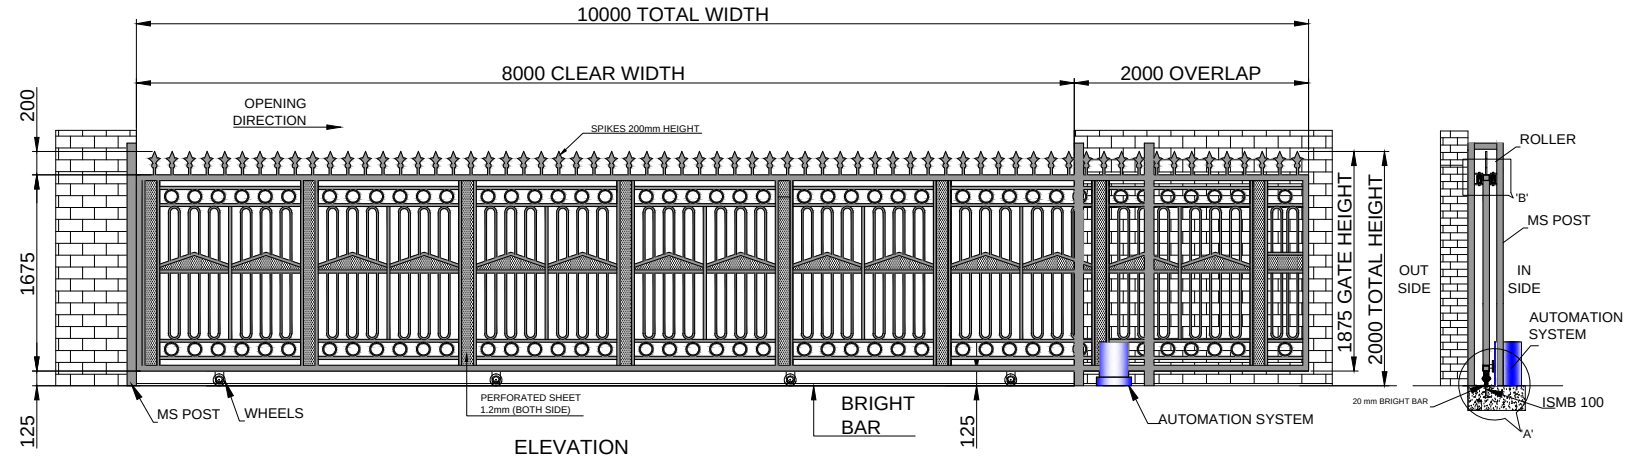
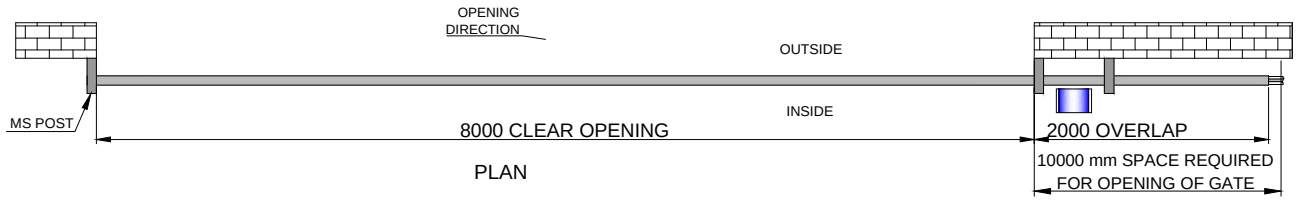
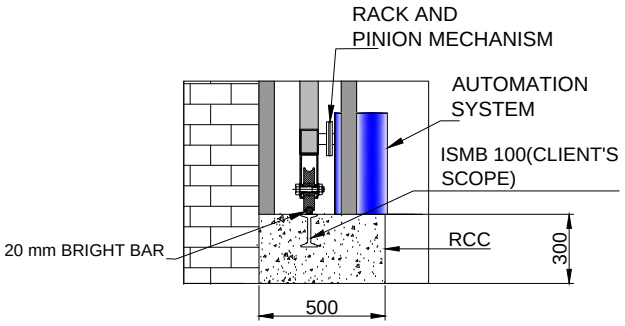


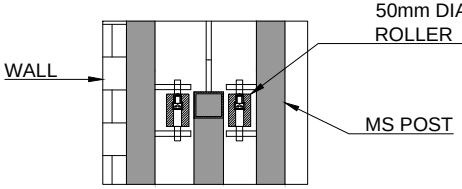

ELEVATION




PLAN




DETAIL VIEW OF A




DETAIL VIEW OF B

| SR NO | GATE SPECIFICATION | MATERIAL | |
|---|---|---|---|
| 1 | 100X50X3.2mm | MS | OUTER FRAME |
| 2 | 50X25X2mm | MS | INNER DESIGN |
| 3 | 25X25X2mm | MS | INNER DESIGN |
| 4 | 15mm Dia. round pipe | MS | INNER DESIGN |
| 5 | 1.2mm THK. perforated sheet | MS | INNER DESIGN |
| 6 | special spikes at top | MS | INNER DESIGN |

TOTAL NO OF POST ARE 6.

| CLEAR WIDTH | CLEAR HEIGHT |
|---|---|
| 8000mm | 2000mm |

TOLERANCE- ±10mm

DIMENSION :

| CLEAR WIDTH | CLEAR HEIGHT | QUANTITY |
|---|---|---|
| 8000mm | 2000mm | |

MATERIAL:

THICKNESS :

NOTE-
1. ALL REQUIRED CIVIL WORK WILL BE IN CLIENTS SCOPE.
2. ONE COAT OF RED OXIDE & TWO COAT OF APPROVED RAL SHADE WILL BE GIVEN TO THE GATE.
3.GATE LEAF WILL BE IN TWO PARTS FOR TRANSPORTATION & WILL BE WELD TOGETHER ON SITE.

NIHVA TECHNOLOGIES PVT. LTD.
NIHVA TECHNOLOGIES PVT. LTD. PUNE
Email:- info@nihva.com
Website:- www.nihva.com

TITLE:

# MOTORIZED SLIDING GATE PATTERN 2

CLIENT'S APPROVAL :

CLIENT - L&T CONSTRUCTION

PROJECT -

SITE LOCATION -KARNATAKA

DWG. NO. : NIHVA/17-18/0269 | REV-0

SCALE: NTS | WT: | SHEET:1 OF 1

DRAWN BY: OMKAR | DATE: 10-11-2017

CHECK BY : S.S. | DATE: 10-11-2017

APPROVED BY : S.S | DATE: 10-11-2017

If any queries contact : design@nihva.com

NOTE: ALL DIMENSIONS ARE IN mm

THIS DRAWING & DESIGN IS THE PROPERTY OF NIHVA TECHNOLOGIES. NOT TO BE SOLD OR COPIED TO ANY OTHER CONCERN.