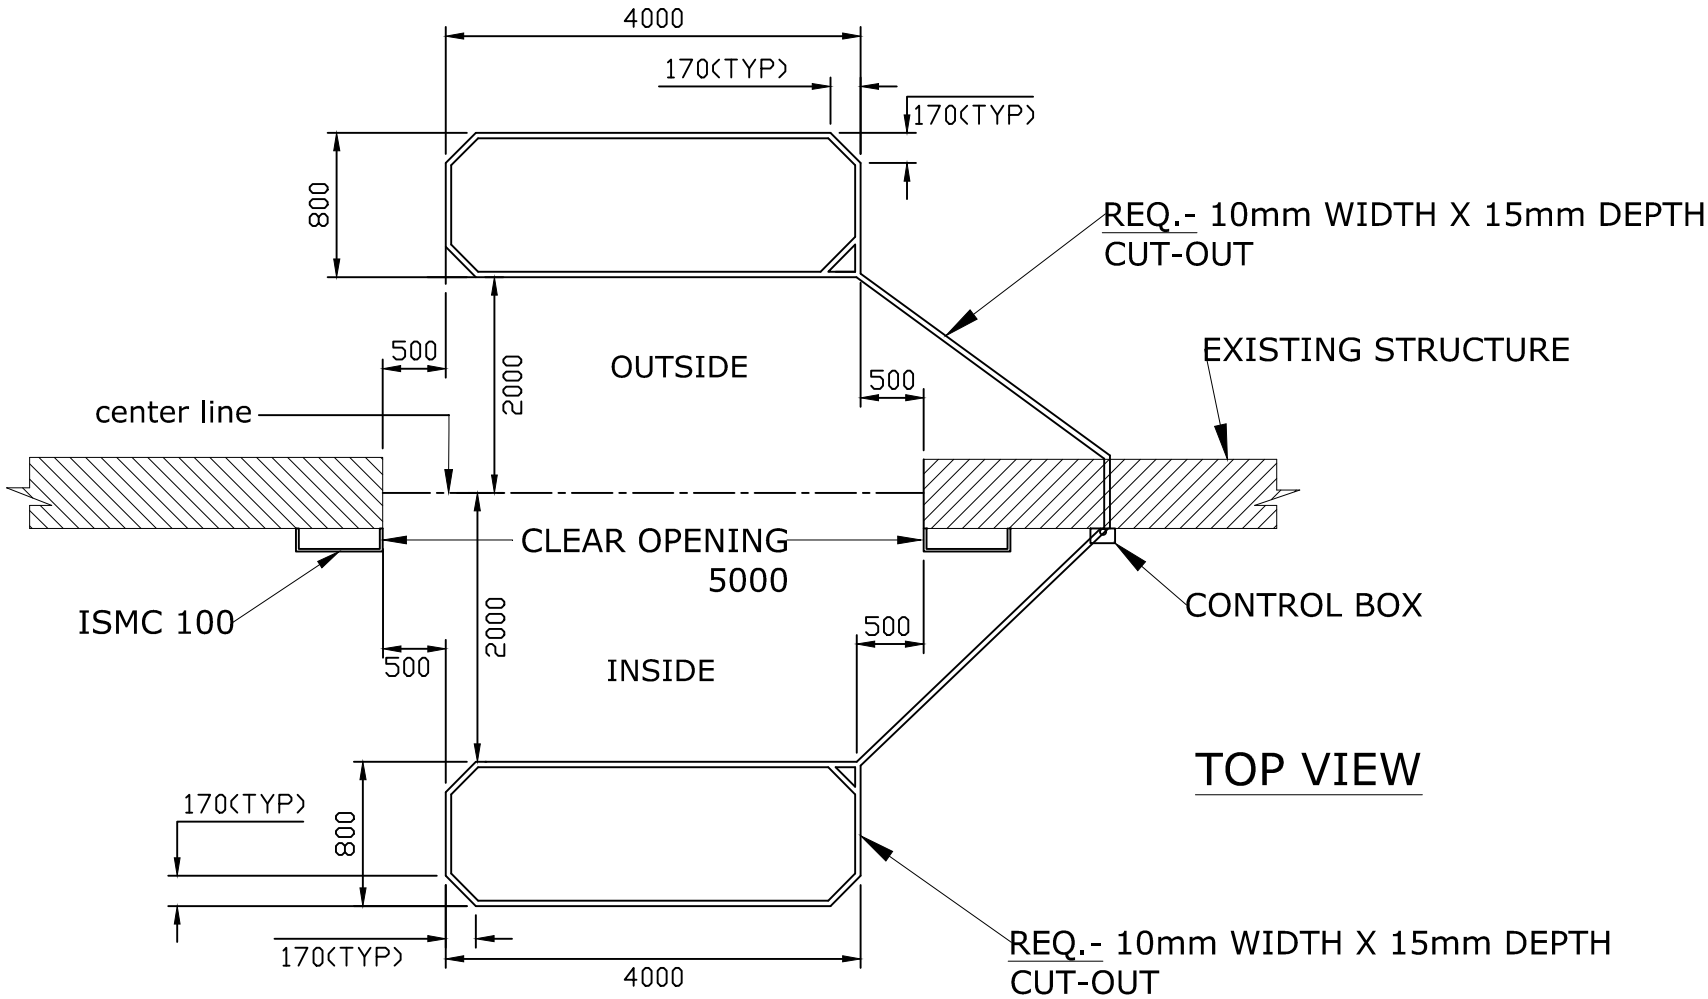


CLEAR WIDTH (CW)	CLEAR HEIGHT (CH)	QUANTITY
5000	5000	1

This drawing & designing is the property of NIHVA TECHNOLOGIES. Not be sold or copy to any other concern.

TITLE

FLOOR CUT-OUT FOR LOOP DETECTOR FOR HIGH SPEED DOOR (RR300+)

CLIENT APPROVAL

ALL DIMENSION ARE IN mm

	SIGN	DATE
DRAWN	SURAJ	18/01/17
CHECK	OMKAR	18/01/17
ENG		
APPRD.	R.K	18/01/17
MFG		
Ref. No.		

NIHVA TECHNOLOGIES PVT. LTD.

NIHVA TECHNOLOGY PVT. LTD. PUNE
Tel : 020 66304033
Email:- info@nihva.com
Website:- www.nihva.com

CLIENT -GE INDIA INDUSTRIAL PVT. LTD

PROJECT-

SITE - MIDC PHASE 2, CHAKAN

DWG. NO. - NIHVA/16-17/125

SCALE: NTS | WT: | SHEET: 01

If any queries contact : projects@nihva.com