
DRAWING :

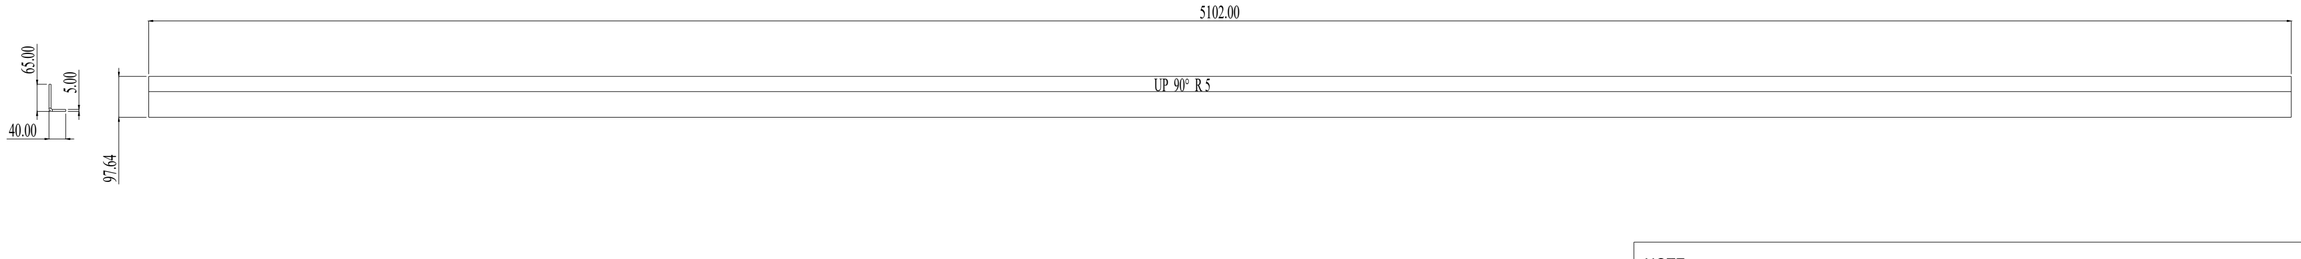

NOTE.:
NAME : TRACK
SIZE : W97.64 X L5102 MM
MTL : SS
THK : 5 MM
QTY : 04 NOS
OPERATION : BENDING

NOTE-
1. ALL CIVIL WORK WILL BE CLIENT'S SCOPE.
2.IF STRUCTURE REQUIRED FOR ROOF IS IN CLIENT'S SCOPE.

This drawing & design is the property of NIHVA TECHNOLOGIES PVT. LTD. Not to be sold or copied to any other concern

DIVISION - ROOF AUTOMATION				NIHVA Technologies Pvt. Ltd.	NIHVA TECHNOLOGIES PVT.LTD. PUNE WEBSITE - www.nihva.com
DWG NO-NTPL-000-PM-01					
	NAME	SIGNATURE	DATE	PRODUCT:SWIMMING POOL DECK	
DRAWN	V.W.		01-04-2026	DWG NO : NTPL-000-PM-01	REVISION NO.:
CHK'D	B.S.		03-04-2026	LOCATION :PUNE	
APPV'D	V.T.		03-04-2026	WEIGHT :19.926 KG	QTY : 04 NOS
If any queries contact: design2@nihva.com				PROJECTION METHOD	SCALE :
ALL DIMENSIONS ARE IN MM		A2			SHEET 1 OF 1