
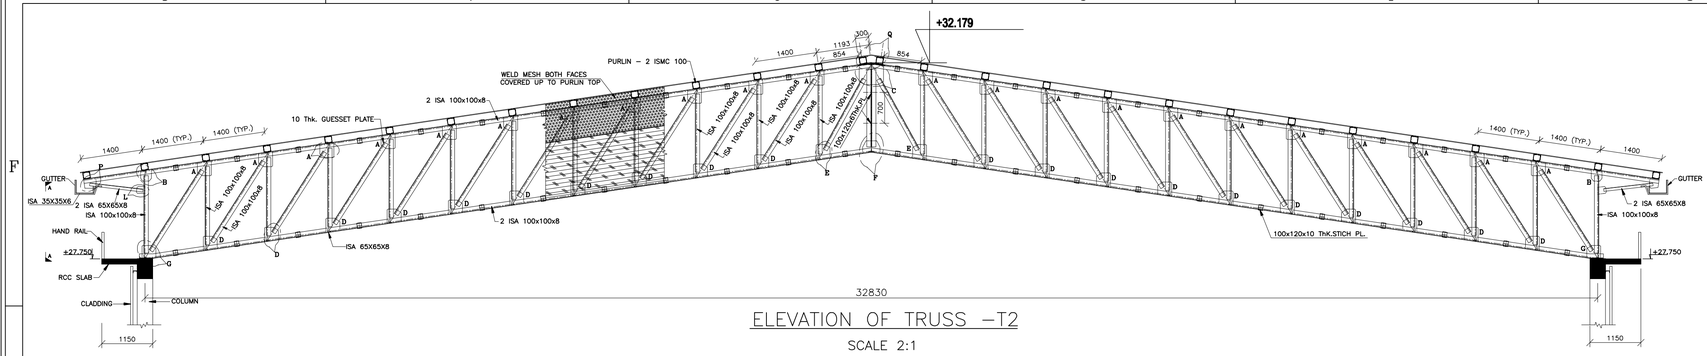


ELEVATION OF TRUSS –T2


SCALE 2:1

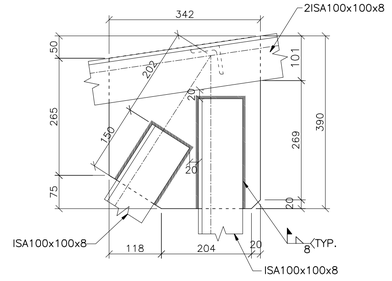

342X390X10 THK. PL.

DETAIL–A


SCALE 1:5

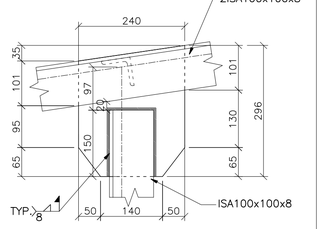

240X296X10 THK. PL.

DETAIL–B


SCALE 1:5

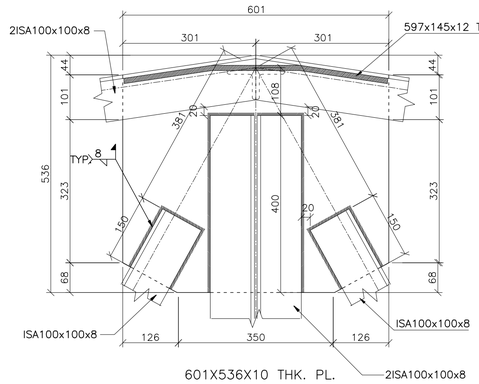

601X536X10 THK. PL.

DETAIL–C


SCALE 1:5

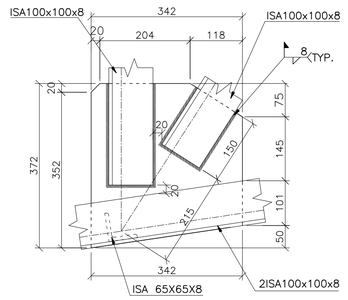

342X372X10 THK. PL.

DETAIL–D


SCALE 1:5

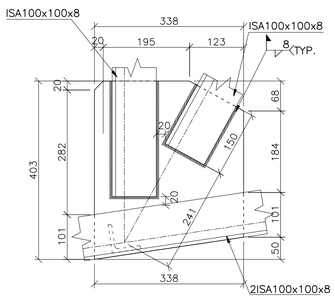

338X403X10 THK. PL.

DETAIL–E

SCALE 1:5

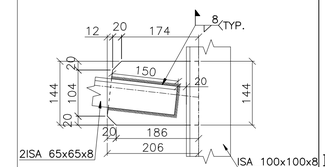

301X342X10 THK. PL.

DETAIL–P


SCALE 1:5

206X144X10 THK. PL.

DETAIL–L

SCALE 1:5


Item No	Description	Length in Mtr	breadth in Mtr	Nos. used	Weight of item	Total Weight in Kg
1	ISA 100x100x8	2.158	–	44	26.33	1158.52
2	ISA 100x100x8	1.824	–	4	22.25	89.00
3	ISA 100x100x8	1.764	–	52	21.52	1119.04
4	ISA 100x100x8	1.400	–	184	17.08	3142.72
5	ISA 100x100x8	1.193	–	16	14.56	232.96
6	ISA 65x65x8	1.204	–	8	9.27	74.17
7	ISA 65x65x8	0.900	–	52	6.93	360.36
8	ISA 65x65x8	1.131	–	24	8.71	209.04
9	ISA 65x65x8	1.417	–	26	10.91	283.68
10	ISA 50x50x6	16.593	–	4	74.67	298.67
11	10THK. PLATE	0.342	0.390	44	10.47	460.69
12	10THK. PLATE	0.240	0.296	4	5.57	22.30
13	10THK. PLATE	0.601	0.536	2	25.29	50.58
14	10THK. PLATE	0.342	0.372	40	9.98	399.48
15	10THK. PLATE	0.338	0.403	4	10.69	42.78
16	10THK. PLATE	0.390	0.300	2	9.18	18.36
17	10THK. PLATE	0.342	0.333	4	8.95	35.75
18	10THK. PLATE	0.243	0.366	24	6.98	165.55
19	10THK. PLATE	0.173	0.341	26	4.63	120.41
20	10THK. PLATE	0.173	0.331	28	4.50	125.87
21	10THK. PLATE	0.170	0.145	2	1.94	3.88
22	10THK. PLATE	0.206	0.144	4	2.32	9.31
23	10THK. PLATE	0.241	0.390	24	7.37	177.08
24	10THK. PLATE	0.170	0.145	2	1.94	3.88
25	10THK. PLATE	0.261	0.279	2	5.71	11.43
26	10THK. PLATE	0.301	0.342	4	8.08	32.32
27	10THK. PLATE	0.597	0.145	2	6.79	13.58
28	20THK. BASEPLT.	0.400	0.250	4	15.70	62.80
29	CHEQRED PLT.	16.593	0.900	2	703.38	1406.75
30	STICH PL.10TK.	0.100	0.120	96	0.94	90.43
31	STICH PL.6TK.	0.100	0.120	4	0.57	2.28
	TOTAL FOR 1 TRUSS					10121.39
	TOTAL FOR 8 TRUSS					80971.12

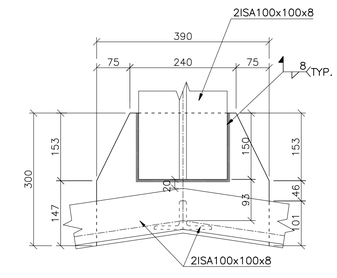

390X300X10 THK. PL.

DETAIL–F


SCALE 1:5

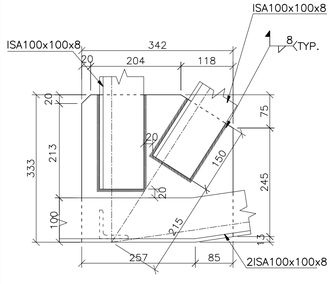

342X333X10 THK. PL.

DETAIL–G


SCALE 1:5

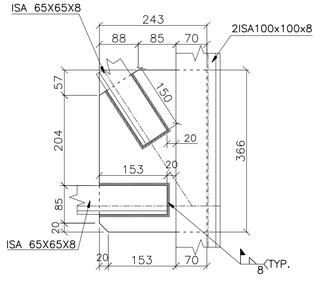

243X366X10 THK. PL.

DETAIL–H


SCALE 1:5

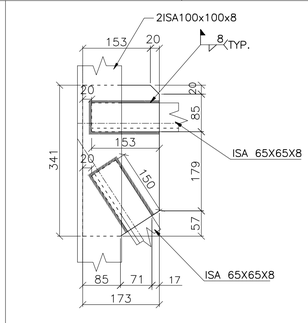

173X341X10 THK. PL.

DETAIL–I


SCALE 1:5

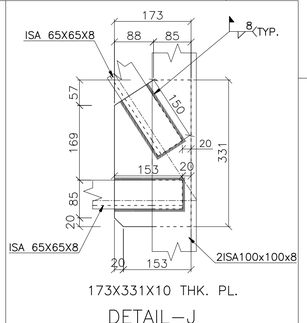

173X331X10 THK. PL.

DETAIL–J


SCALE 1:5

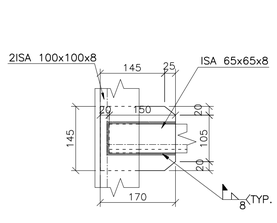


170X145X10 THK. PL.

DETAIL–K


SCALE 1:5

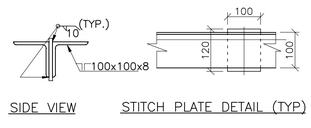


SIDE VIEW STITCH PLATE DETAIL (TYP)

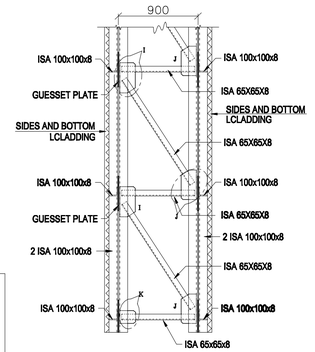


TOP CHORD DETAIL

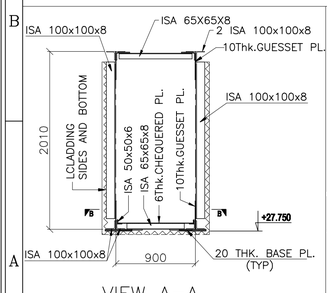

VIEW A–A

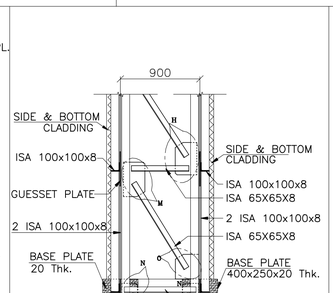


VIEW B–B

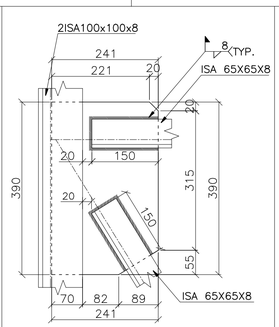

241X390X10 THK. PL.

DETAIL–M


SCALE 1:5

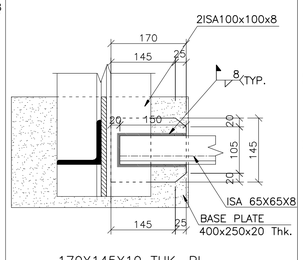

170X145X10 THK. PL.

DETAIL–N


SCALE 1:5

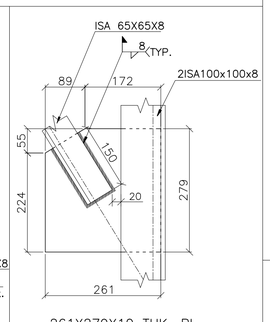

261X279X10 THK. PL.

DETAIL–O

SCALE 1:5

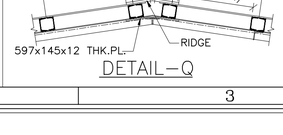

DETAIL–Q

REV.	DESCRIPTION	DATE	DRAWN	CHECKED	APPROVED

Aarbin Engineers Pvt.Ltd.

KOCHI

	NAME	DATE
DESIGN	DM	21/02/09
DRAWN	VPL	26/02/09
CHECKED	DM	26/02/09
APPROVED	AHF	06/03/09

CLIENT : M.D.ESTHAPPAN INFRASTRUCTURE (P) LTD.

CONSULTANTS : KITCO Ltd.

DETAILS : DETAILS OF TRUSS -T2 (32.83M SPAN). AIRCRAFT MAINTANANCE HANGER.

SCALE : NTS REV.

DRG NO :- ARB/B/MDE/2