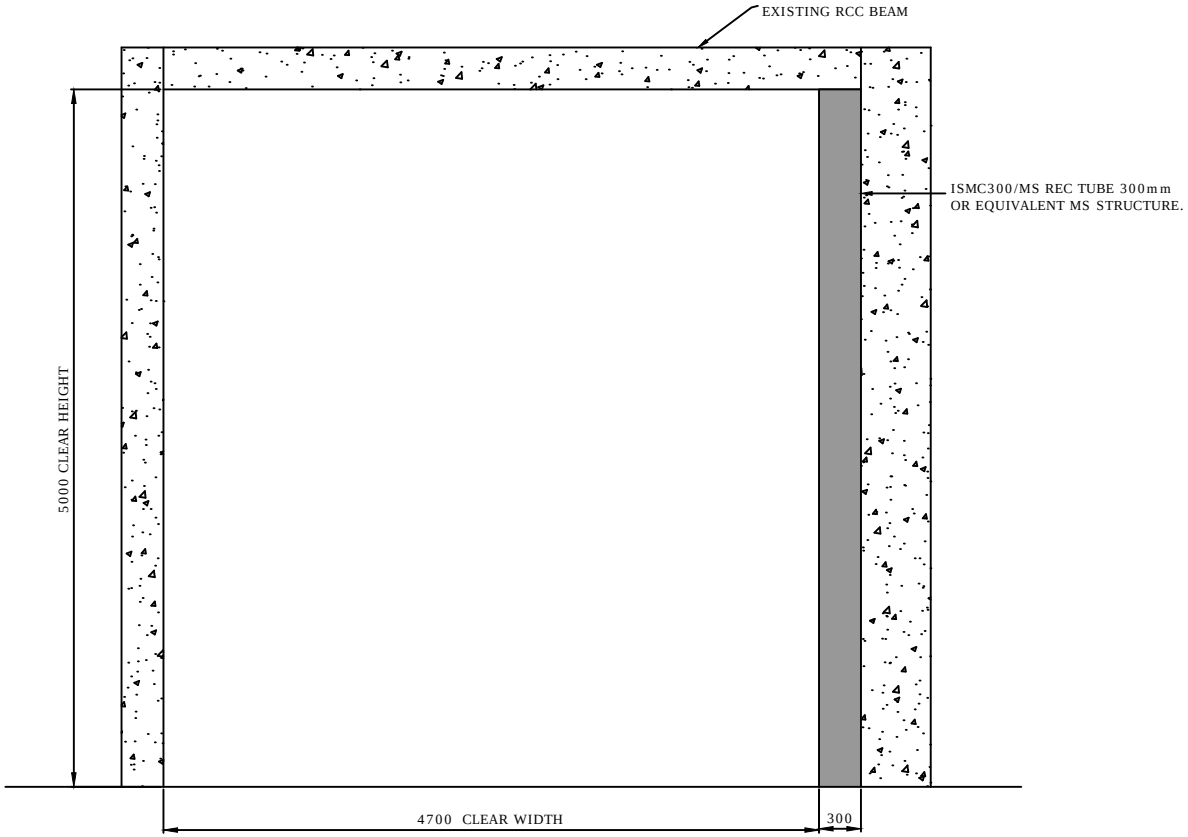

ELEVATION

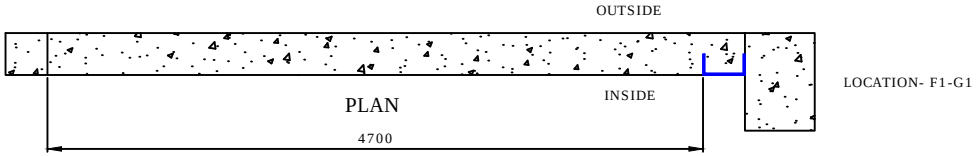

PLAN

LOCATION- F1-G1

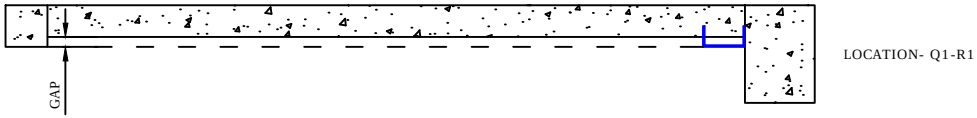

LOCATION- Q1-R1

NOTE- FOR Q1-R1 LOCATION REQUIRE HORIZONTAL STRUCTURAL SUPPORT ON COLUMN TO MINIMIZE GAP.

SHUTTER TYPE	CLEAR WIDTH (CW)	CLEAR HEIGHT (CH)	QUANTITY	LOCATION	INSTALLATION
RS5	4700	5000	1	F1-G1	INSIDE
RS5	4700	5000	1	Q1-R1	INSIDE

DIMENSION :

CLEAR WIDTH	CLEAR HEIGHT	QUANTITY
4700	5000	2

MATERIAL:

THICKNESS :

NOTE:
1.REQUIRED STRUCTURE FOR ROLLING SHUTTER WILL BE CLIENT'S SCOPE.
2.ONE COAT OF RED OXIDE PRIMER WILL BE GIVEN TO THE SHUTTER.
3.FOR FINAL FINISH CLIENT SHOULD MENTION COLOR SHADE FOR ROLLING SHUTTER.

NIHVA TECHNOLOGIES PVT. LTD.
NIHVA TECHNOLOGIES PVT. LTD. PUNE
Email:- info@nihva.com
Website:- www.nihva.com

TITLE:

STRUCTURE FOR GEAR OPERATED ROLLING SHUTTER

CLIENT'S APPROVAL :

CLIENT - SCON

PROJECT - BEKAERT INDUSTRIES PVT. LTD.

SITE LOCATION - RANJANGAON

DWG. NO. : NIHVA/16-17/210

SCALE: NTS	WT:	SHEET:1 OF 1

DRAWN BY: SURAJ	DATE: 1-04-2017
CHECK BY : SAGAR P.	DATE: 1-04-2017
APPROVED BY : R.K	DATE: 1-04-2017

If any queries contact : projects@nihva.com

NOTE: ALL DIMENSIONS ARE IN mm

THIS DRAWING & DESIGN IS THE PROPERTY OF NIHVA TECHNOLOGIES. NOT TO BE SOLD OR COPIED TO ANY OTHER CONCERN.