

GRS1 – Grilled Rolling Shutter. – 3000mm x 3000mm.

23/01/2015

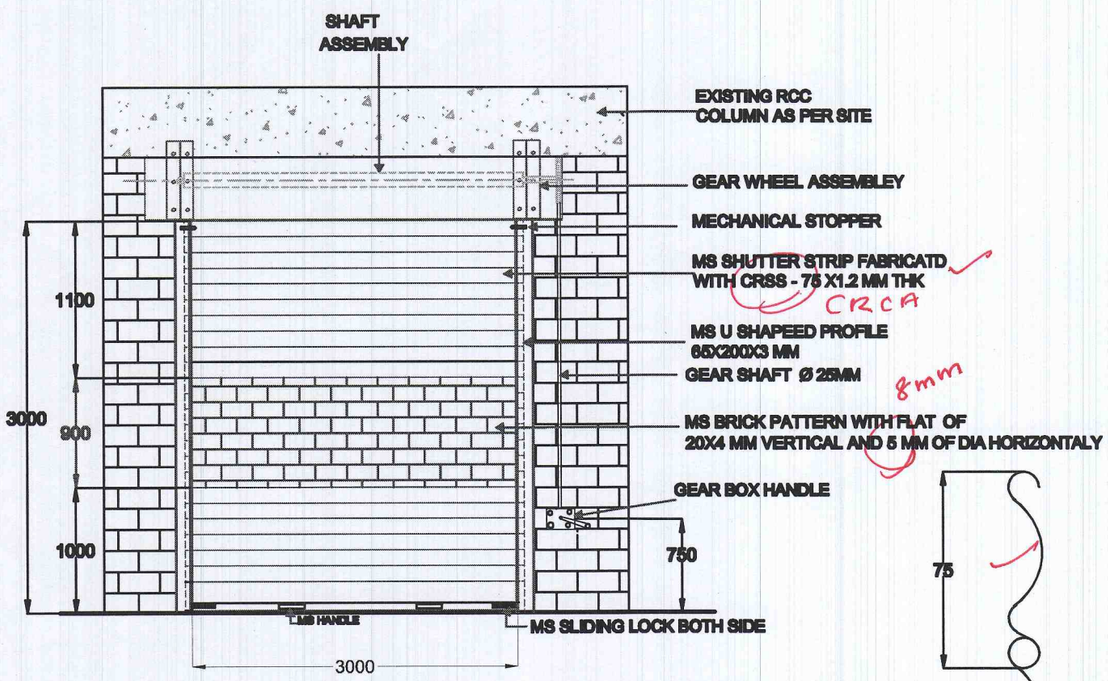


INSIDE ELEVATION


Clear Opening size:-
(W)3.0m x (H)3.0m

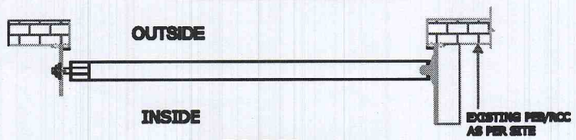


PLAN

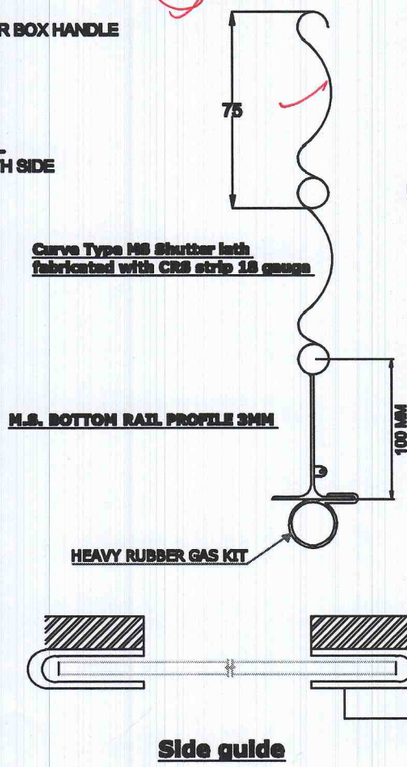

Side guide

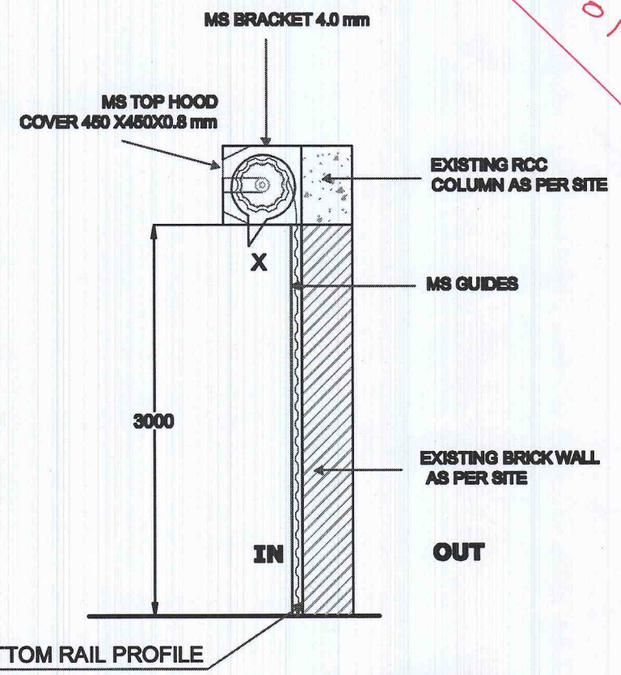

SIDE VIEW

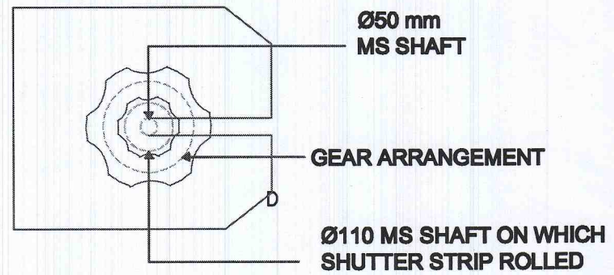

Bracket

Location :- Substation
Size :- 3.0m(W) X 3.0M (H)

THIS PRINT IS THE PROPERTY OF NIHVA TECHNOLOGIES PVT LTD
RETURNED UPON REQUSETHIS PART MUST NOT BE SOLD TO ANY OTHER CONCERN

TITLE:	Grilled Manual Gear Operated Rolling Shutter - GRS 1	DO NOT SCALE DRAWING	
CLIENTS APPROVEL:–		SIGN / DATE	
		DRAWN: ABHIJIT 20/01/15	
		CHECK: Anil 20/01/15	
		ENG:	
		APPRD.:	
ALL DIMENSION ARE IN M.M.		PROD:	
		MFG:	
		Ref. No.:	

NIHVA TECHNOLOGIES PVT. LTD.
NIHVA TECHNOLOGIES PVT. LTD. Pune:-411044
Tel :- 020 66304033
Email :- info@nihva.com

CLIENT: REWARD CONSTRUCTION
PROJECT / SITE: IR PROJECT/ NAROL - AHEMDABAAD
PRODUCT NAME:
DWG. NO.: NVA/REWARD/01/R2
REV.: 0
SCALE: NTS WT: SHEET: 1 OF 1