UTILITY ROOM
FASCIA (TYP.)
RAIN WATER PIPE (TYP.)
GUTTER
CANOPY(TYP.)
PRE COLOR COATED STANDING SEAM ROOF SHEETING (TYP.)
ROOF MONITOR (TYP.)
7500
1
2
3
4
5
6
7
8
9
10
11
12
13
J
H
G
F
E
D
C
B
A

2 ROOF PLAN
SCALE 1:250

PANEL ROOM
WORKER FACILITY
OTTA FOR UTILITY
HT ROOM
TR
TR
STORE ROOM
WORKER FACILITY
230MM THK.3500 MM HT. BRICK WALL AND ABOVE CLADDING SHEET (TYP.)
600X1800MM WIDE DOOR CANOPY
RAIN WATER PIPE (TYP.)
WINDOW CANOPY(TYP.)
D101
W101
RS101
RAMP UP
HRM SHED
7500
705
6395
6300
322500
±323910
1
2
3
4
5
6
7
8
9
10
11
12
13
14
15
16
17
18
19
20
21
22
23
J
H
G
F
E
D
C
B
A

1 GROUND FLOOR PLAN
SCALE 1:250

THIS DRAWING & DESIGN IS THE SOLE PROPERTY OF VMS & SHALL NOT BE COPIED, TRACED OR REPRODUCED BY ANY MEANS WITHOUT PRIOR WRITTEN CONSENT OF THE FIRM.

GENERAL NOTES :

1. ALL THE DIMENSIONS ARE UNFINISHED DIMENSIONS.
2. ALL DIMENSIONS ARE IN MM AND LEVELS ARE IN MT, UNLESS OTHERWISE MENTIONED.
3. ALL THE DIMENSIONS SHALL BE READ & NOT TO BE MEASURED.
4. IN CASE OF ANY DISCREPANCY, BRING IT TO THE NOTICE OF THE ARCHITECT IMMEDIATELY.
5. DETAIL DRAWING PRECEDES THE GENERAL DRAWING

SCHEDULE OF OPENINGS:

MKD.	SIZE	SILL HT.	LINTEL HT.	TOTAL NO.	REMARKS
D101	1200x2400	----	2400	26	FIRE DOOR
RS101	4000x4500	----	4500	2	ROLLING SHUTTER
W101	3000x1500	900	2400	62	ALU. FRAME WITH FIXED GLASS & ALU. LOUVER WINDOW

FOR TENDER

NO.	DATE	DESCRIPTION	DRAWN BY	CHECKED BY
R0	-	-	-	-

REVISION HISTORY

KEY PLAN
SCALE : N.T.S.

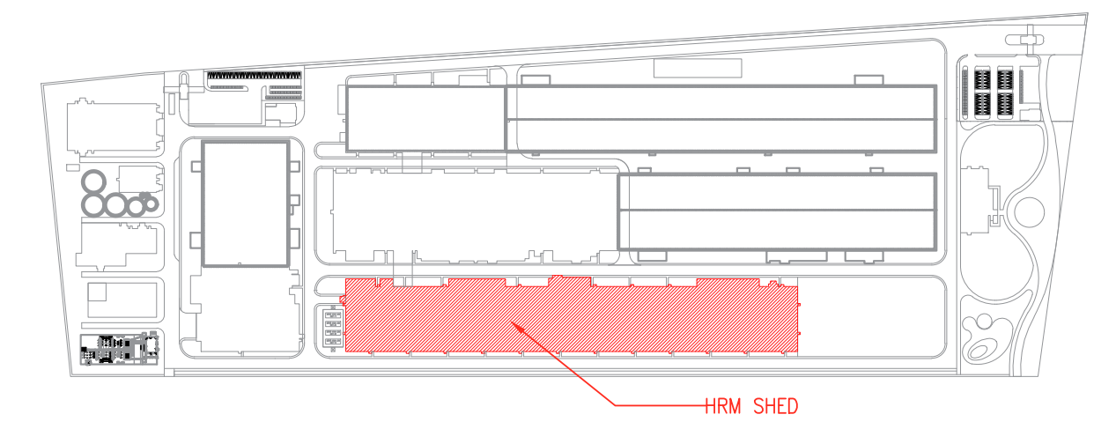

REFERENCE DRAWINGS :
01. ARCHITECTURAL : -
02. STRUCTURAL : -
03. HVAC : -
04. ELECTRICAL : -
05. UTILITIES : -

GROUND FLOOR & ROOF PLAN

HRM SHED

AGRAWAL METAL WORKS(P) LTD.

PROJECT NO.	SCALE :	DRAWN :	SURENDER Y.
3824	AS SHOWN	CHECKED:	BHAKTI B.
	DATE : 03-12-2024	APPROVED:	DARSH D.
		COORDINATION CHECKED:	DARSH D.

VMS
ENGINEERING + ARCHITECTURE
VMS ENGINEERING & DESIGN SERVICES (P) LTD.
CHITRAKOOT FLATS, B/H TIMES OF INDIA, OFF ASHRAM ROAD,
AHMEDABAD-380 009. PHONE: +91 (079) 2658-8829, 4023-6236
WWW.VMSCONSULTANTS.COM

SHEET SIZE	DRAWING NO.	TENDER	REVISION:
600x 1800	T.A.2.101	T	R0