

DRAWING


REV DESCRIPTION	DATE	REV NO
	05-06-2026	REV 00
1. CUTOUT LENGTH INCREASES 20,000MM TO 20,220MM	16-06-2026	REV 01

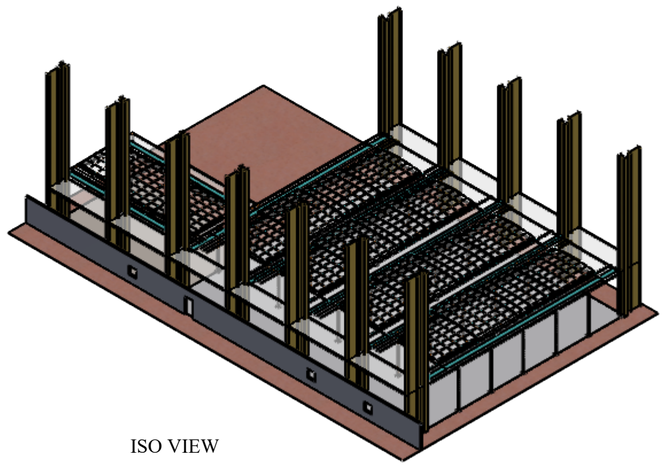


ISO VIEW

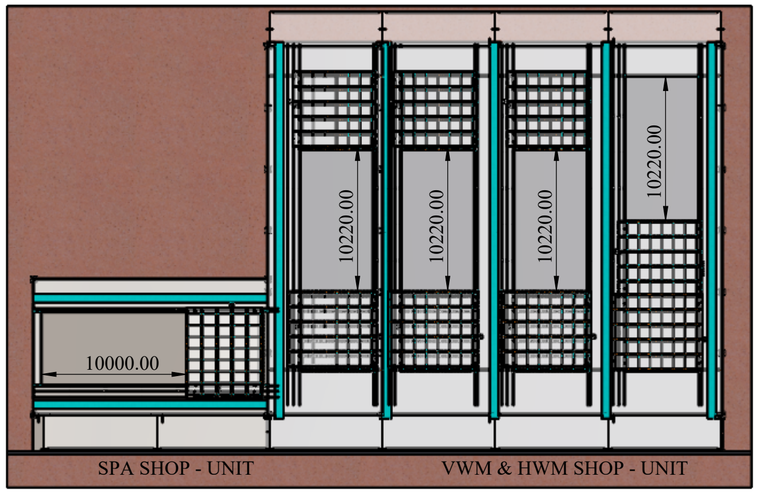


OPEN VIEW 1 T.V

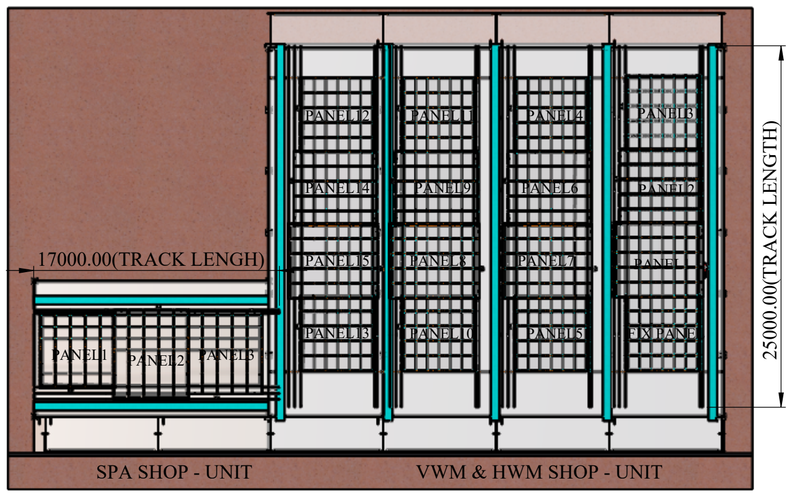


CLOSE VIEW

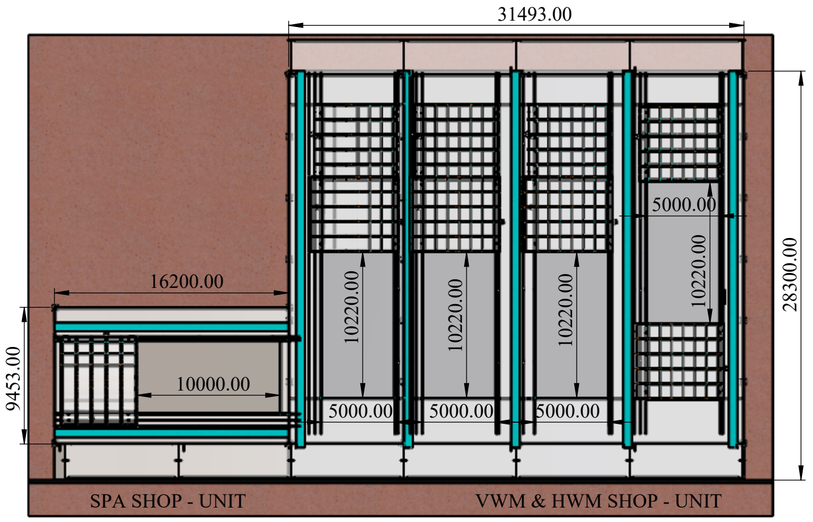


OPEN VIEW 2 T.V

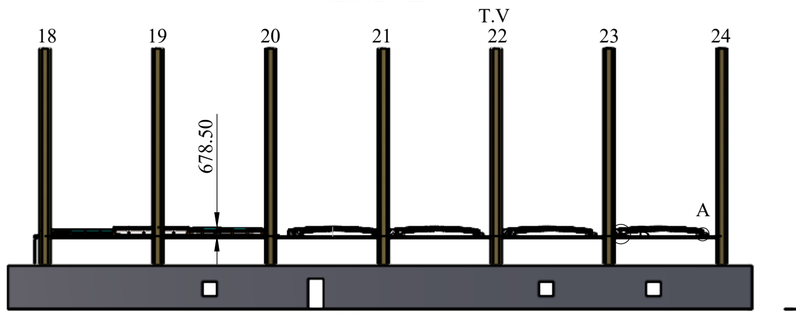


F.V

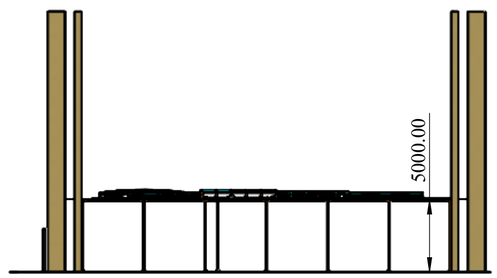

S.V

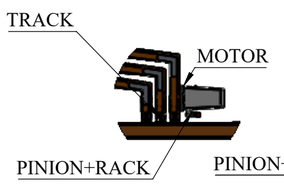

DETAIL A
SCALE 1 : 30

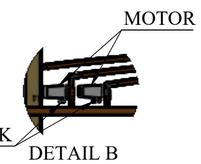

DETAIL B
SCALE 1 : 50

NOTE :

THIS DRAWING IS FOR CLIENT SCOPE
BASE STRUCTURE IN CLIENT SCOPE.

SPECIAL INSTRUCTION'S :

This drawing & design is the property of NIHVA TECHONOLOGIES PVT. LTD. Not to be sold or copied to any other concern

TITLE - ROOF AUTOMATION


DWG NO - NTPL-401-PM-01

NIHVA TECHNOLOGIES PVT.LTD.PUNE
Website - www.nihva.com

	NAME	SIGNATURE	DATE
DRAWN	V.W.		05-06-2026
CHK'D	S.P.		06-06-2026
APPV'D	V.T.		06-06-2026

PRODUCT - RETRACTABLE ROOF
PROJECT NO - NTPL-000-PM | REVISION - 00
SITE LOCATION - HYDRABAD
MATRIAL - | QTY - 1
If any queries contact - info@nihva.com
PROJECTION METHOD:
SCALE :
ALL DIMENSION ARE IN mm | A2
SHEET 1 OF 2

DRAWING

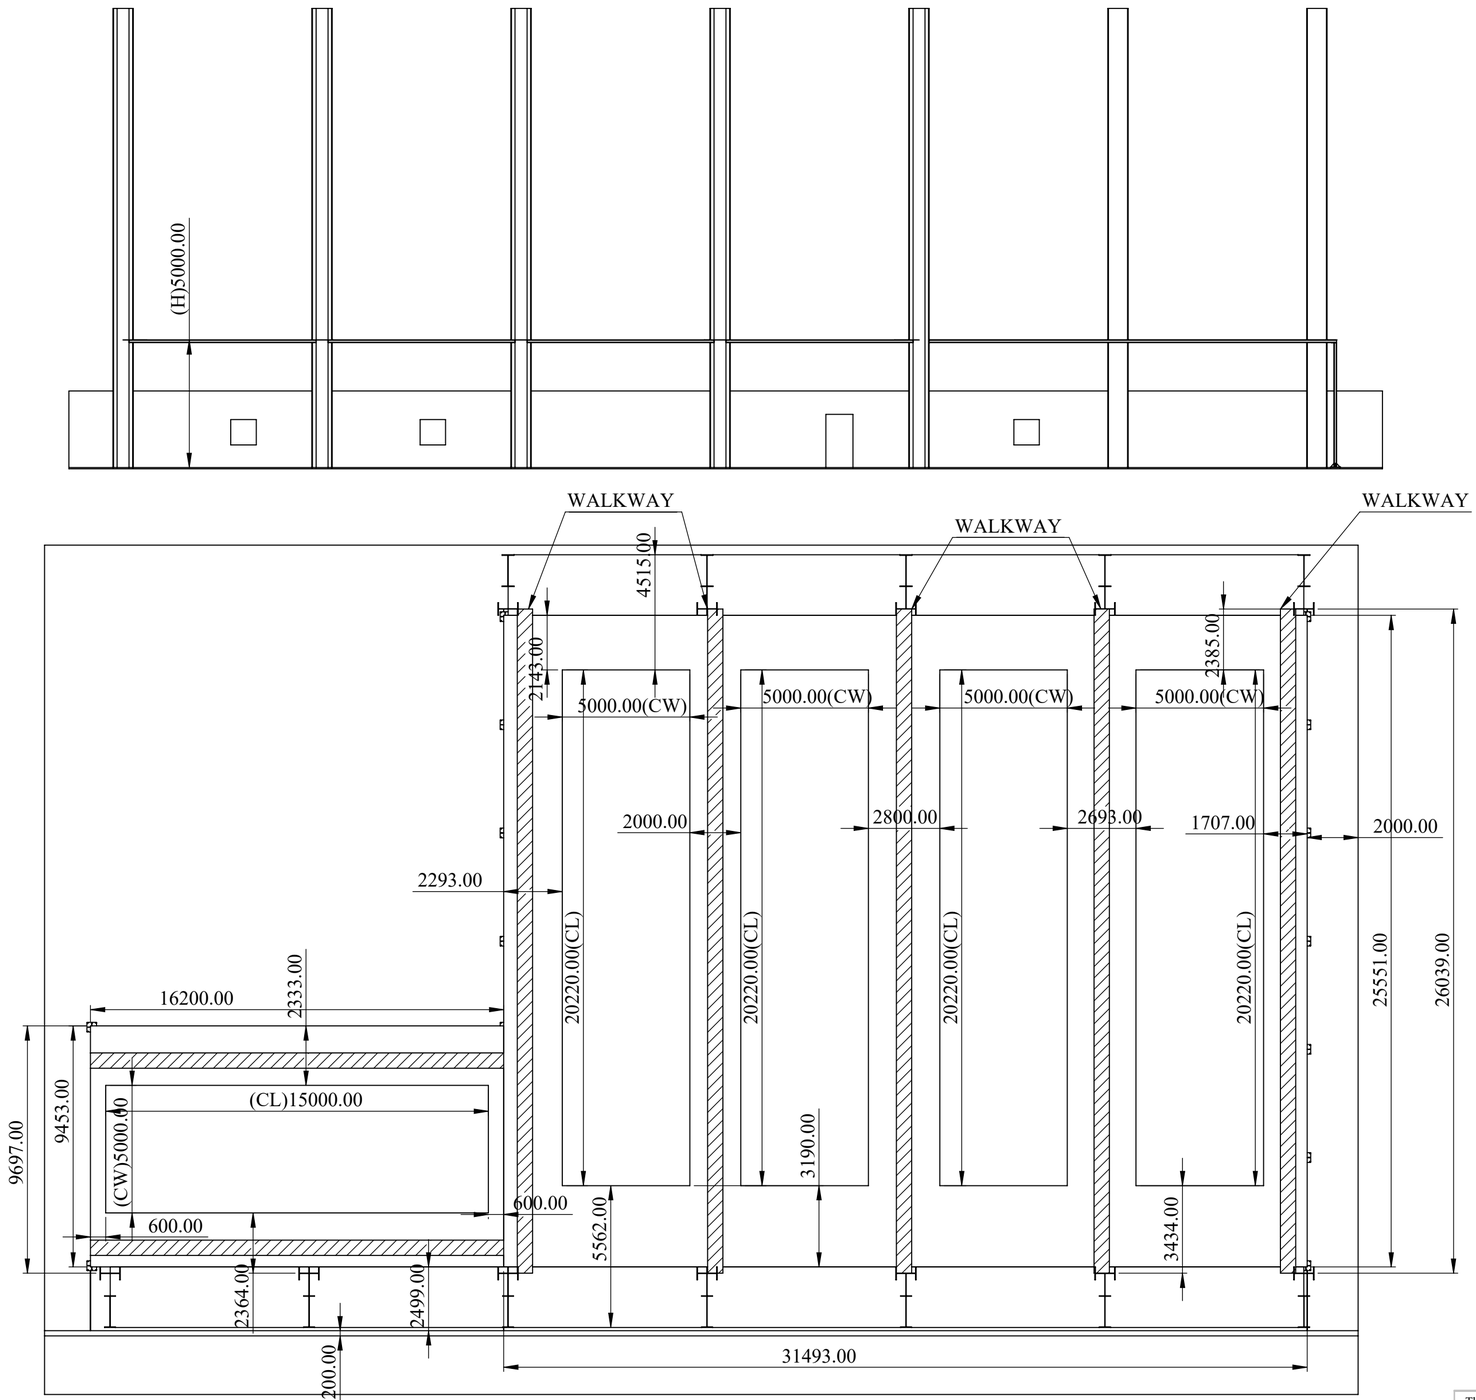

REV DESCRIPTION	DATE	REV NO
	05-06-2026	REV 00
1.		

NOTE :

BASE STRUCTURE IN CLIENT SCOPE

SPECIAL INSTRUCTION'S :

This drawing & design is the property of NIHVA TECHONOLOGIES PVT. LTD. Not to be sold or copied to any other concern

TITLE - ROOF AUTOMATION

DWG NO - NTPL-000-PM-001

NIHVA TECHNOLOGIES PVT.LTD.PUNE
Website - www.nihva.com

	NAME	SIGNATURE	DATE
DRAWN	V.W.		05-06-2026
CHK'D	S.P.		06-06-2026
APPV'D	V.T.		06-06-2026

PRODUCT - RETRACTABLE ROOF

PROJECT NO - NTPL-000-PM | REVISION - 00

SITE LOCATION - | WEIGHT -

MATRIAL - | QTY - 1

If any queries contact - info@nihva.com

ALL DIMENSION ARE IN mm | A2

PROJECTION METHOD:

SCALE :

SHEET 2 OF 2